
REV.	DESCRIPTION.	REVISED BY	SIGN	DATE
000	RELEASED GA DWG FOR APPROVAL	MAHESH S.		19.11.22
001	MODIFIED ROOF PER SITE VISIT CHANGES & STRUCTURE	MAHESH S.		24.11.22
002	MODIFIED STRUCTURE PER CLIENT CHANGES	MAHESH S.		08.12.22


PROPOSED PLAN LAYOUT

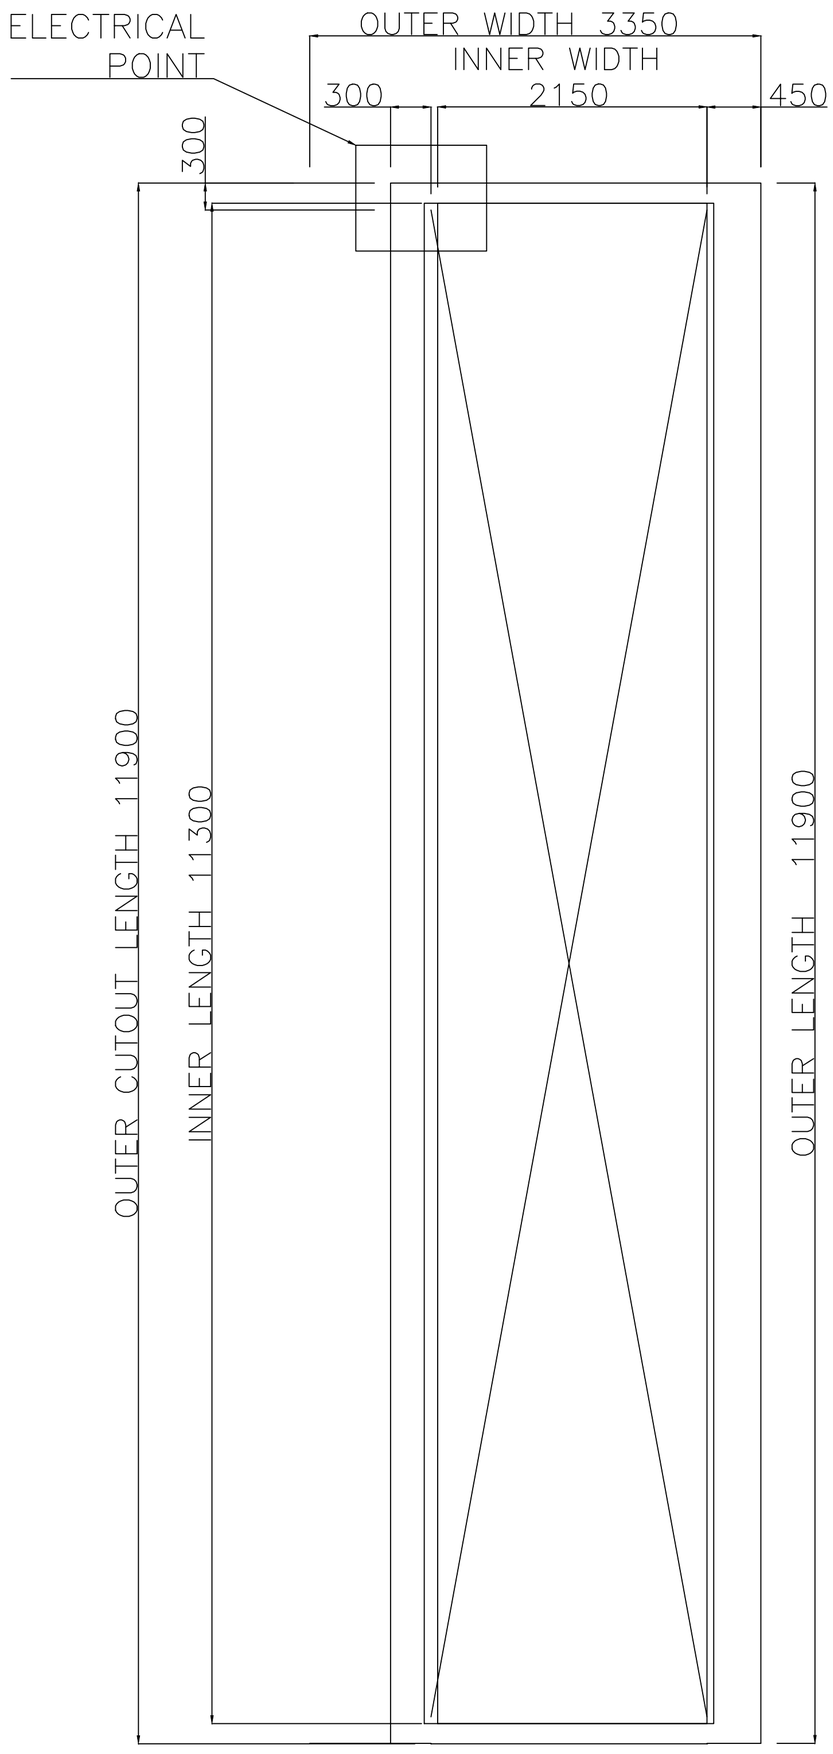

PROPOSED PLAN


L BRACKET (CLIENT SCOPE)
- FOR TRACK MNTG .
MS 450 X 150 H X 16 MM THK

SUPPORTS - SPACING 1500 MM
RECT. TUBE 60 X 40 X 3.2 THK

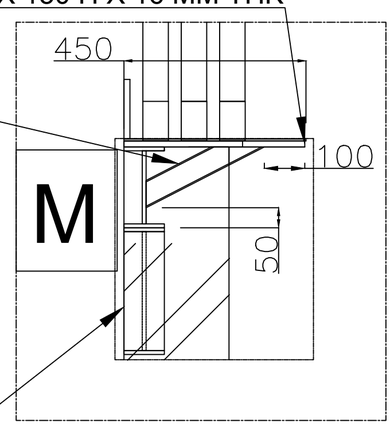

HEIGHT AS PER SITE
(WINDOW HT)

DETAIL VIEW "A"

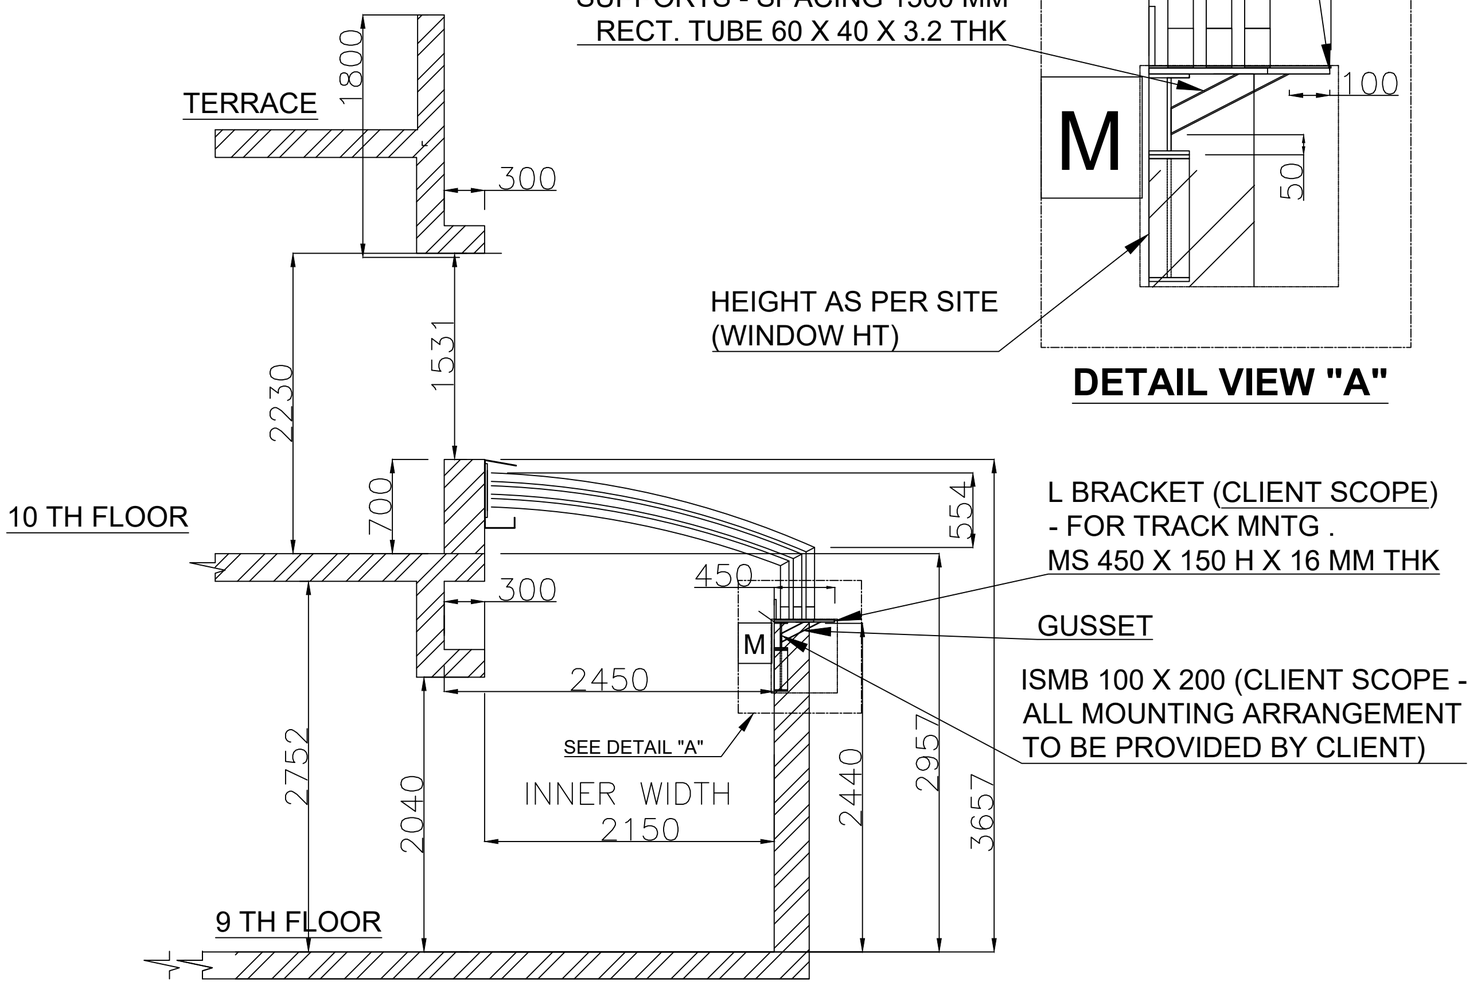

L BRACKET (CLIENT SCOPE)
- FOR TRACK MNTG .
MS 450 X 150 H X 16 MM THK

GUSSET

ISMB 100 X 200 (CLIENT SCOPE -
ALL MOUNTING ARRANGEMENT
TO BE PROVIDED BY CLIENT)

SECTION VIEW

1. THE STRUCTURE AROUND THE CUT OUT SHOULD BE OF FLAT SURFACE FOR PROPER FASTENING OF ROOF.
2. TOP SURFACE SHOULD BE OF PARALLEL / FLAT FOR SMOOTH FUNCTIONING OF ROOF.
3. ROOF EXTENSION IS SHOWN FOR ONLY REFERENCE. IT CAN BE MODIFIED AS PER THE WORK UNDERTAKEN.
4. GRADIENT OF 150MM X 16 MM PLATE NEED TO BE PROVIDED ALONG THE OUTER LENGTH TO AVOID WATER STAGNANCY IN GUIDE RAIL.
5. AL PROFILE - POWDER COATED
6. GASKET - EPDM
7. MOTOR - ITALIAN/GERMAN MAKE
8. ELECTRICAL REQUIREMENT -
9. ALL DIMENSION IN MM.
10. ALL CIVIL WORK / TRACK MOUNTING ARRANGEMENT IS IN CLIENT SCOPE.

This drawing & design is the property of NIHVA TECHNOLOGIES. Not to be sold or copied to any other concern.

TITLE				
PROPOSED PLAN LAYOUT				
	NAME	SIGN	DATE	
DRAWN	MAHESH S.		19.11.22	CLIENT - MR. SAMEER MEHTA
CHECK	MAHESH S.		19.11.22	PROJECT - RETRACTABLE ROOF
APPRD.	VIJAY T.		19.11.22	SITE LOCATION- JAMUNA NIKETAN
If any queries contact : projectsautomation@nihva.com				NIHVA\22-23\00XX / REV- 0
ALL DIMENSION ARE IN mm				SCALE: NTS / SHEET: 01 OF 01

NIHVA TECHNOLOGIES PVT. LTD.
NIHVA TECHNOLOGIES PVT. LTD. PUNE
Tel : 020 66304033
Email:- info@nihva.com
Website:- www.nihva.com