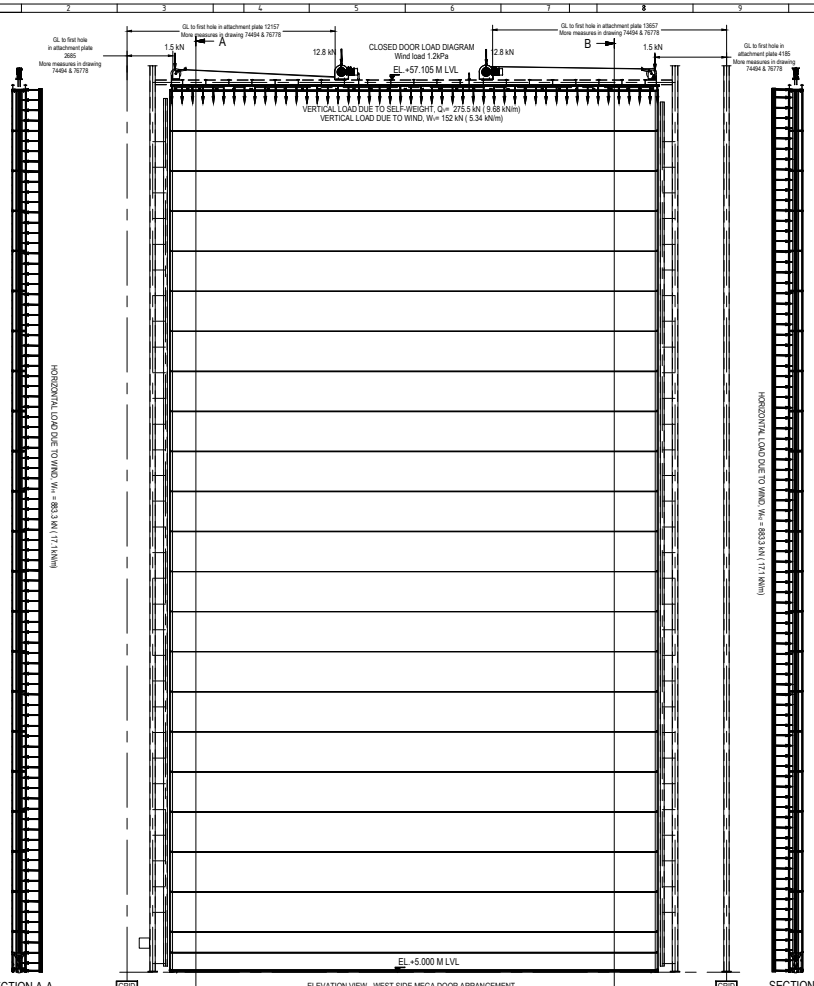



| Revision | Date | By |
|---|---|---|
| A Costumer steel and measures added. | 2022-01-14 | FV |
| B Clear height was 47500. | 2022-01-20 | FV |

NOT INCLUDED IN DOOR SUPPLY:

1. Design and supply of all door supporting structural components.
2. Design and supply of all closure between door and adjacent steel.
3. Design and supply of coverage, such as roofing or enclosure, for door components at door head.
4. Door jambs adjustable for overall door width and true to plumb.
5. Paint job after completed door installation.
6. Any frameworks being provided by ASSA ABLOY will be clearly indicated as "by ASSA ABLOY".

REQUIREMENTS ON BUILDING:

7. Door head support must be straight within 1/600 of span in the in/out direction and free from protrusions of any kind.
8. For a single door leaf, door head support should be horizontal and straight within 1/600 of span at distributed full door load.
9. Door side jambs must be smooth, straight and parallel, out of plumb must not exceed 2mm/m (total deviation at full length 5 mm) in any direction.
10. Any footings at bottom of jamb columns must not interfere with installation of guide rails at floor level.
11. At time of installation, finished floor, free from obstructions, out to a distance of 2 m on each side of door centreline must be available.
12. Bracket/attachment plate for hoist should be flat within 5mm/m.

DOOR PROPERTIES:

13. The door is designed to withstand a differential pressure of 1.2kPa.
14. Guide rails, top- and intermediate beams in extruded aluminium with natural finish.
15. Environmental category: C5 according to ISO 12944-2
16. Bottom beam in carbon steel painted: Light grey (RAL7047)
17. Colored clamp strips on both sides: Grey
18. The door fabric is a UV stabilized, flame retardant, self-extinguishing, PVC coated polyester fabric with fire technical properties Euroclass B-s2, d0 (according to EN 13501-1:2007).
19. Colour of fabric: GREY (NCS 3500, RAL 7004)

ELECTRICAL:

20. One main control panel provided of PLC type.
21. Control mode : Impulse up / Constant contact down.
22. Cables are included.
23. Back-up power socket & switch.
24. Audible & visual alarm.
25. Wind-lock indication.
26. Approx. size of main control panel: WxHxD (600x600x210 mm),
27. Location of main control panel: Please specify location.
28. Aux. Voltage 24VDC
29. Power supply: 415V /3Ph /50Hz
30. Power: 50.4kW
31. Nom. current: 94A
32. Start. current: 624A
33. (max. allowed voltage drop at start: 5%)

DOOR IDENTITY NUMBER: 84704001-004
INTERFACE, ref. to drwng. no. 74494

| | | | |
|---|---|---|---|
| DESIGNED FV | UNIT A1F | SCALE 1:100 | Seabird Karwar |
| CODE 84704 | If not otherwise stated: Dimensions acc. to ISO 13920-B | | India |
| ITEM NO | Surface class acc. to EN 12944-5 | | Megadoor 28000 x 47264 |
| DATE 2021-11-03 | Steel class acc. to EN 10277-5 | | Load diagram & Notes |
| ASSA ABLOY | Surface finish Smooth raw surface | DRAWING NO 74495 | REVISION B |

The information contained in this drawing is the property of ASSA ABLOY Entrance Systems AB and/or its subsidiaries. Reproduction, use or disclosure to third parties without express authority is strictly forbidden.