

NOTE : ~ PLEASE MAINTAIN 7 MM GAP BETWEEN TWO LIP BUSHES.

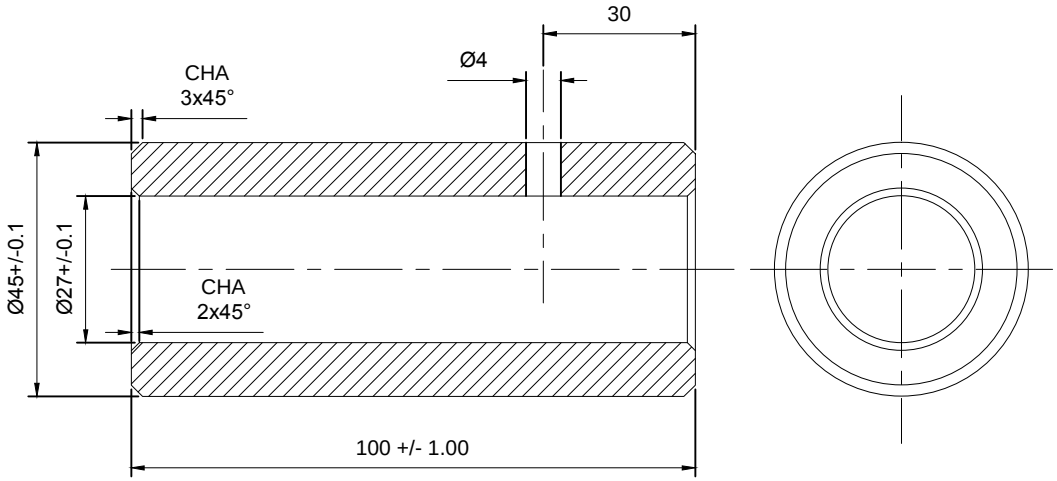


NOTE:~ MTL : MS

BUSH Ø45 X 103L = 18 NOS

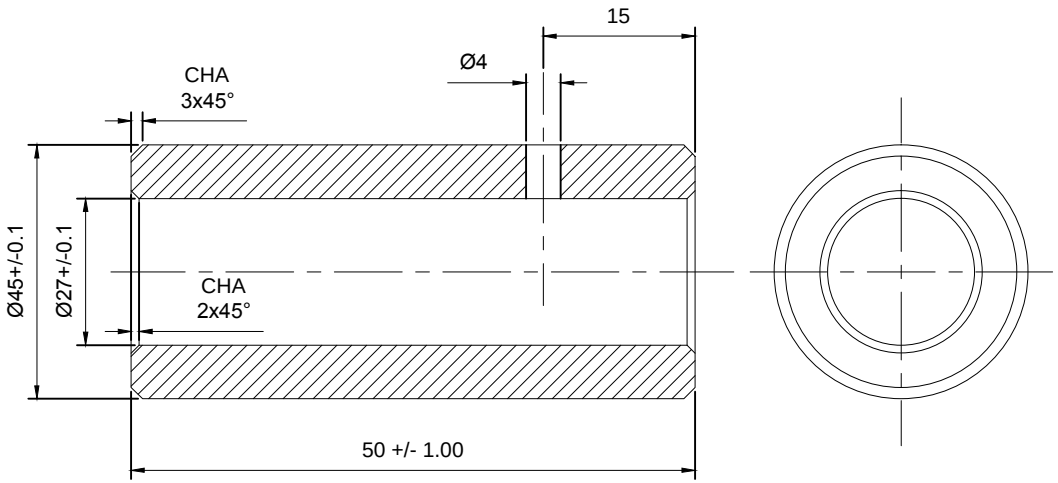


NOTE:~ MTL : MS

BUSH Ø45 X 53L = 08 NOS

This drawing & design is the property of NIHVA TECHNOLOGIES. Not to be sold or copied to any other concern.

| | | | |
|---|---|---|---|
| TITLE: LIP MOUNTING BUSH | | | NIHVA TECHNOLOGIES PVT. LTD. PUNE<br>Tel : 020 66304033<br>Email:- info@nihva.com<br>Website:- www.nihva.com |
| | NAME | SIGN | DATE |
| DRAWN | P.V.A | | 17.10.2019 |
| CHECK | V.M.T | | 17.10.2019 |
| APPRD. | | | |
| If any queries contact : design@nihva.com | | | |
| ALL DIMENSION ARE IN mm | | | |

CLIENT -

PROJECT - NDL451

SITE LOCATION -

DWG. NO. : NIHVA/19-20/VDR/183

SCALE: NTS | WT: | REV- 0