
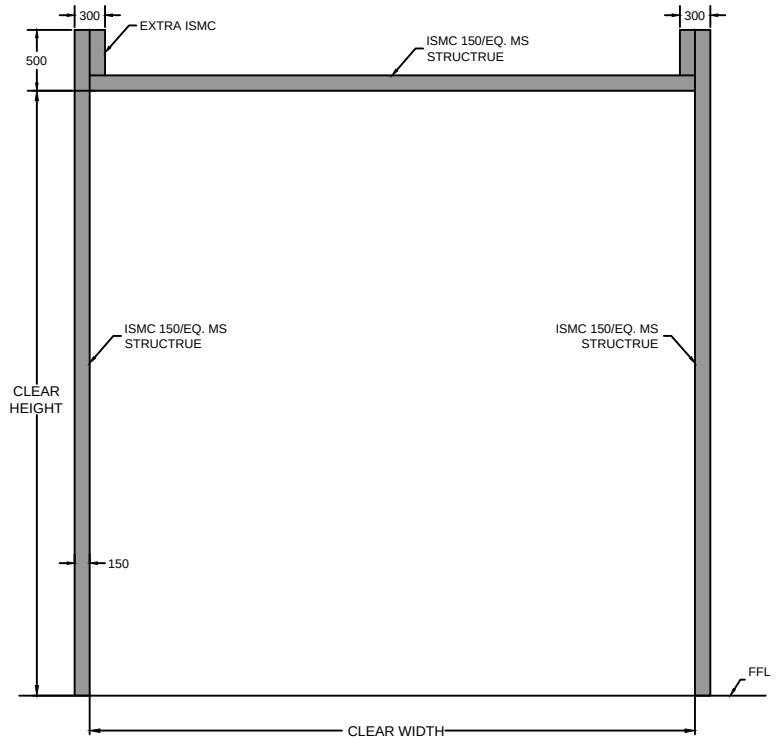


INSIDE ELEVATION

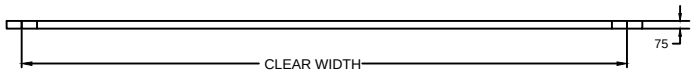

PLAN

TOLERANCE - ±10mm

SR NO.	CLEAR WIDTH	CLEAR HEIGHT	QUANTITY
1	2500 mm	3000 mm	04

This drawing & design is the property of NIHVA TECHNOLOGIES. Not to be sold or copied to any other concern.

TITLE: MS STRUCTURE FOR SECTIONAL DOOR

NIHVA TECHNOLOGIES PVT. LTD.

NIHVA TECHNOLOGIES PVT. LTD. PUNE
Tel : 020 66304033
Email:- info@nihva.com
Website:- www.nihva.com

	NAME	SIGN	DATE
DRAWN	SURAJ		06-03-2018
CHECK	OMKAR		06-03-2018
APPRD.	SHEKHAR		06-03-2018

CLIENT - PACKTIME INNOVATIONS PVT. LTD.

PROJECT -

SITE LOCATION - PUNE

If any queries contact : design@nihva.com

DWG. NO. : NIHVA/17-18/ 0392 | REV- 0

ALL DIMENSION ARE IN mm | SCALE: NTS | WT: | SHEET: 01 OF 01