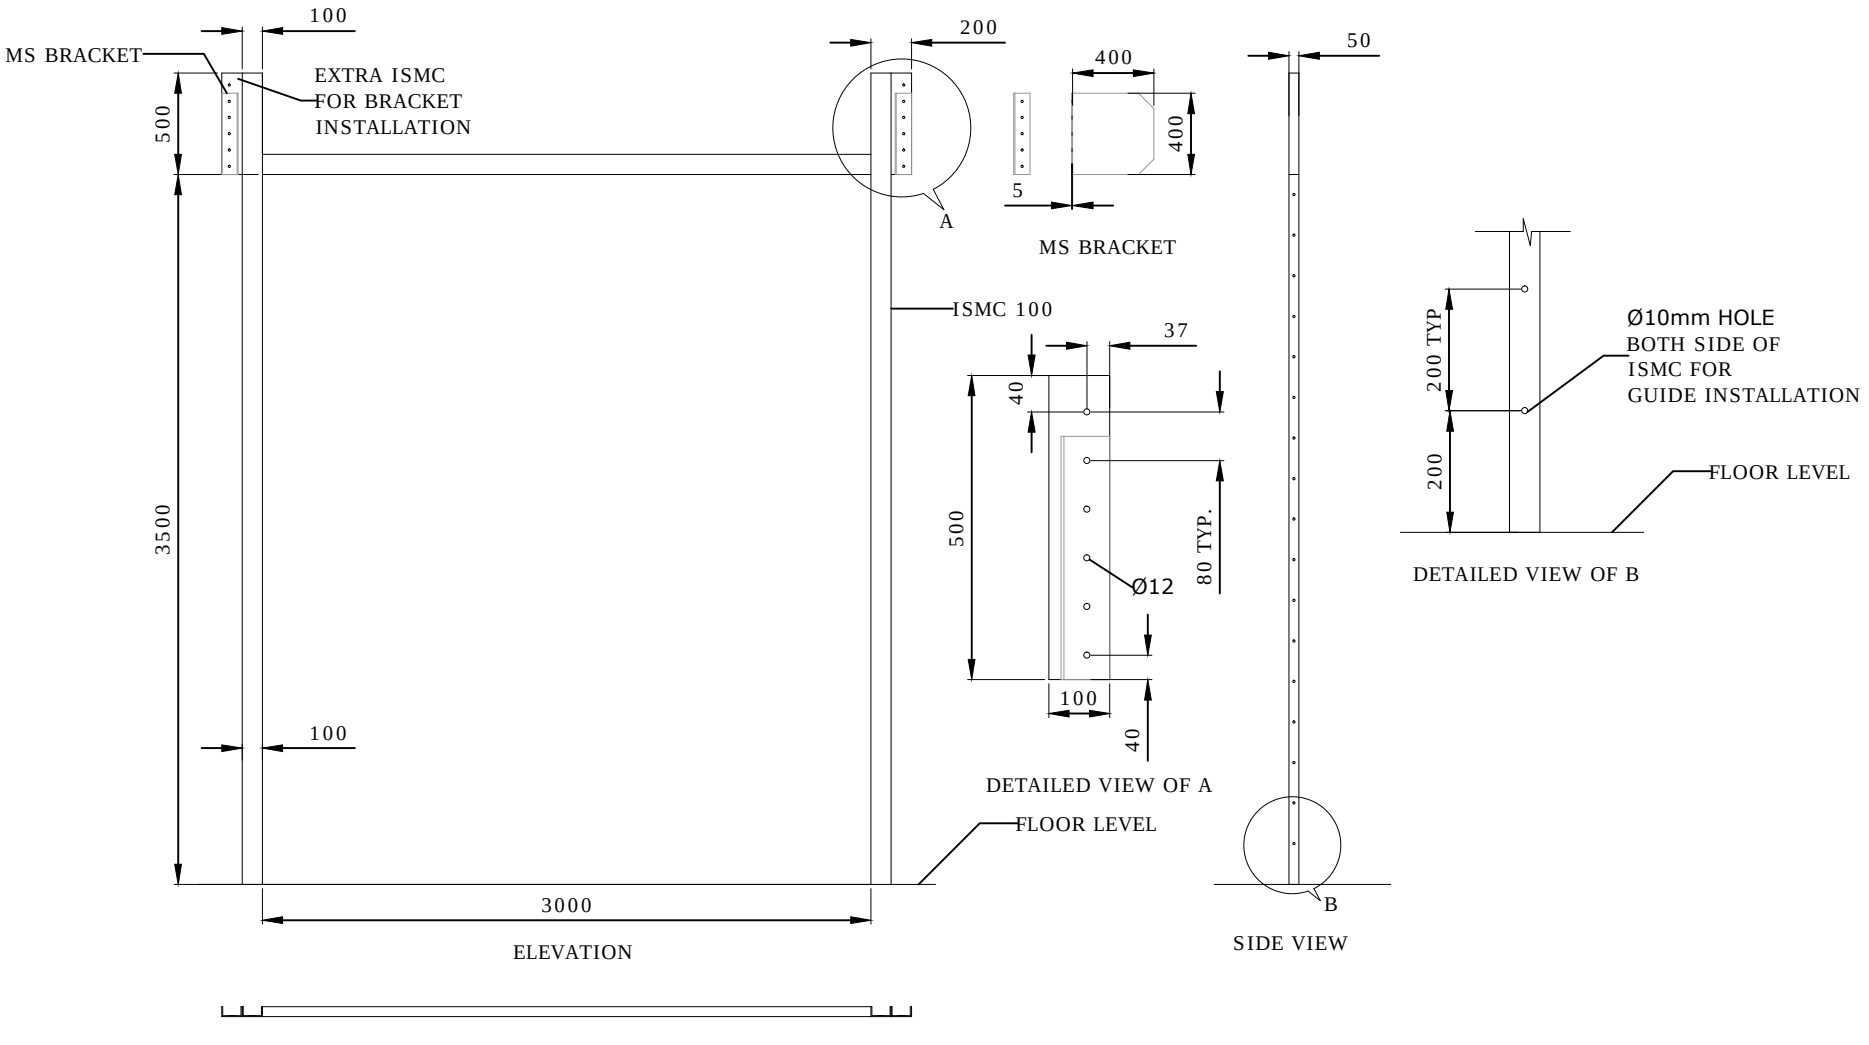

CLEAR WIDTH (CW)	CLEAR HEIGHT (CH)	QUANTITY
3000	3500	7

This drawing & designing is the property of NIHVA TECHNOLOGIES. Not to be sold or copied to any other concern.

TITLE
STRUCTURE DETAILS FOR ROLLING SHUTTER

NIHVA TECHNOLOGIES PVT. LTD.
NIHVA TECHNOLOGIES PVT. LTD. PUNE
Tel : 020 66304033
Email:- info@nihva.com
Website:- www.nihva.com

	SIGN	DATE
DRAWN	OMKAR	21/11/17
CHECK	SHEKHAR	21/11/17
APPROVAL	SHEKHAR	21/11/17
MFG.		

If any queries contact : design@nihva.com

ALL DIMENSION ARE IN mm

CLIENT - MITTAL PRECISION HITECH STEEL PVT.LTD

PROJECT -

SITE - CHAKAN,PUNE

DWG. NO. : NIHVA/17-18/0285 | REV-0

SCALE: NTS | WT: | SHEET: 01 OF 01