
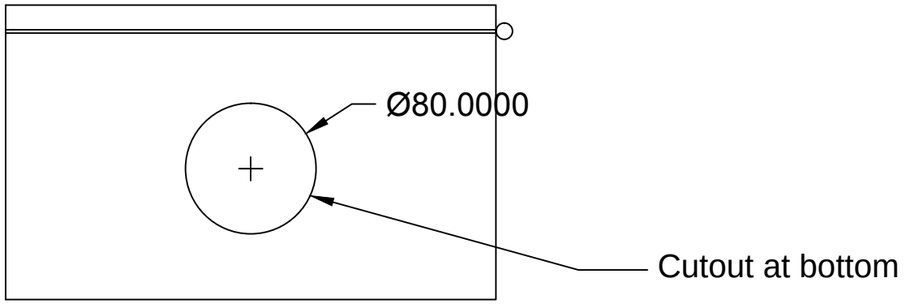


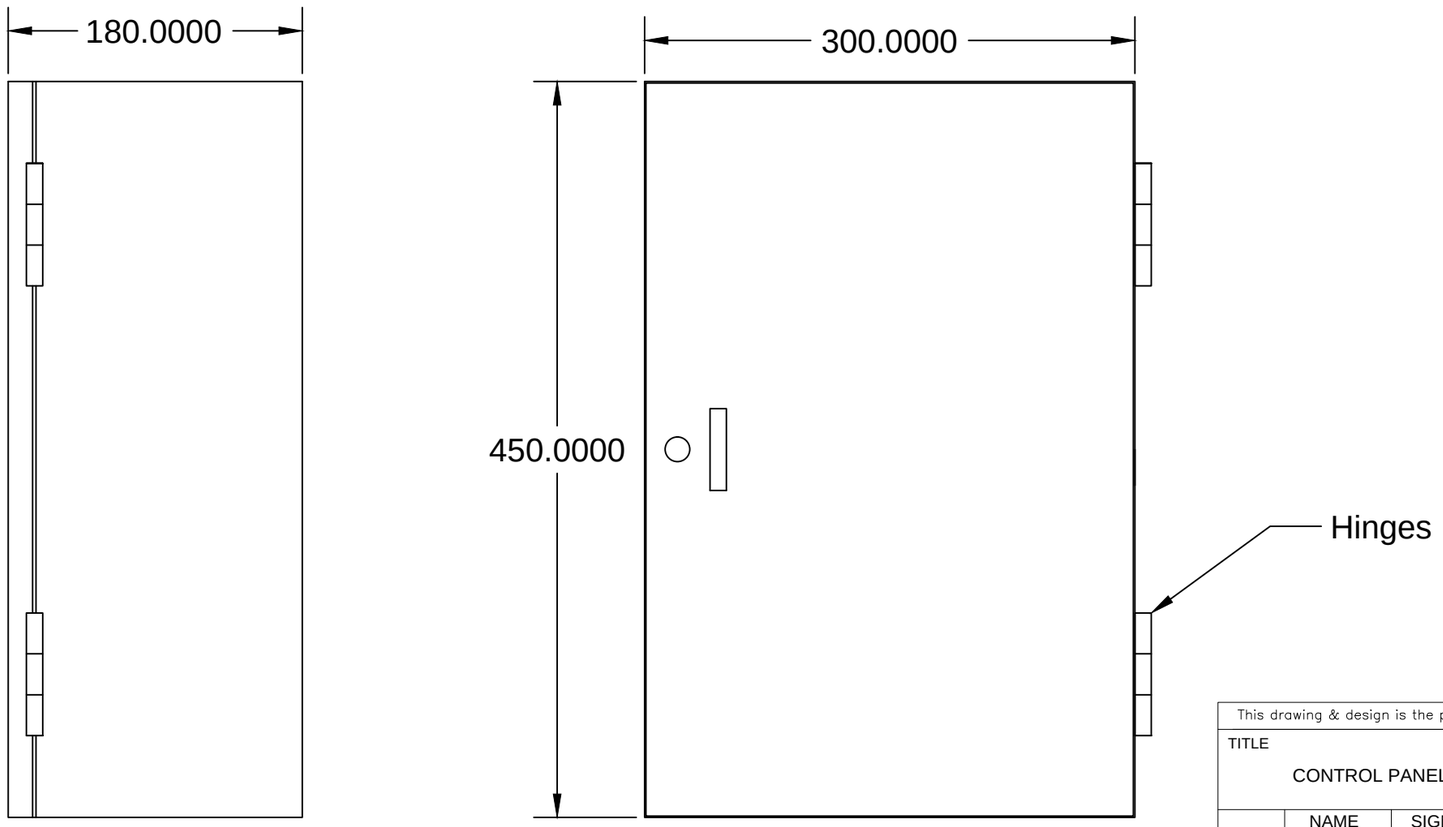

NOTE:
1. Material: SS
2. Thickness: 1 mm
3. Quantity: 1 nos
4. Opening- LHS

This drawing & design is the property of NIHVA TECHNOLOGIES. Not to be sold or copied to any other concern.

TITLE: CONTROL PANEL COVER

	NAME	SIGN	DATE
DRAWN	G.I.P.		14.01.22
CHECK	A.K.		14.01.22
APPRD.			

NIHVA TECHNOLOGIES PVT. LTD.
NIHVA TECHNOLOGIES PVT. PUNE
Tel : 020 66304033
Email:- info@nihva.com
Website:- www.nihva.com

CLIENT -
PROJECT- HIGH SPEED DOOR
SITE LOCATION -
If any queries contact : design@nihva.com
DWG. NO. : NIHVA/21-22/MFG/014
ALL DIMENSION ARE IN mm
SCALE: NTS
WT:
REV- 0