

REV.	DESCRIPTION.	REVISED BY	SIGN	DATE
000	RELEASED GA DWG FOR APPROVAL	MAHESH S.		19.11.22
001	MODIFIED ROOF PER SITE VISIT CHANGES & STRUCTURE	MAHESH S.		24.11.22

PROPOSED PLAN LAYOUT

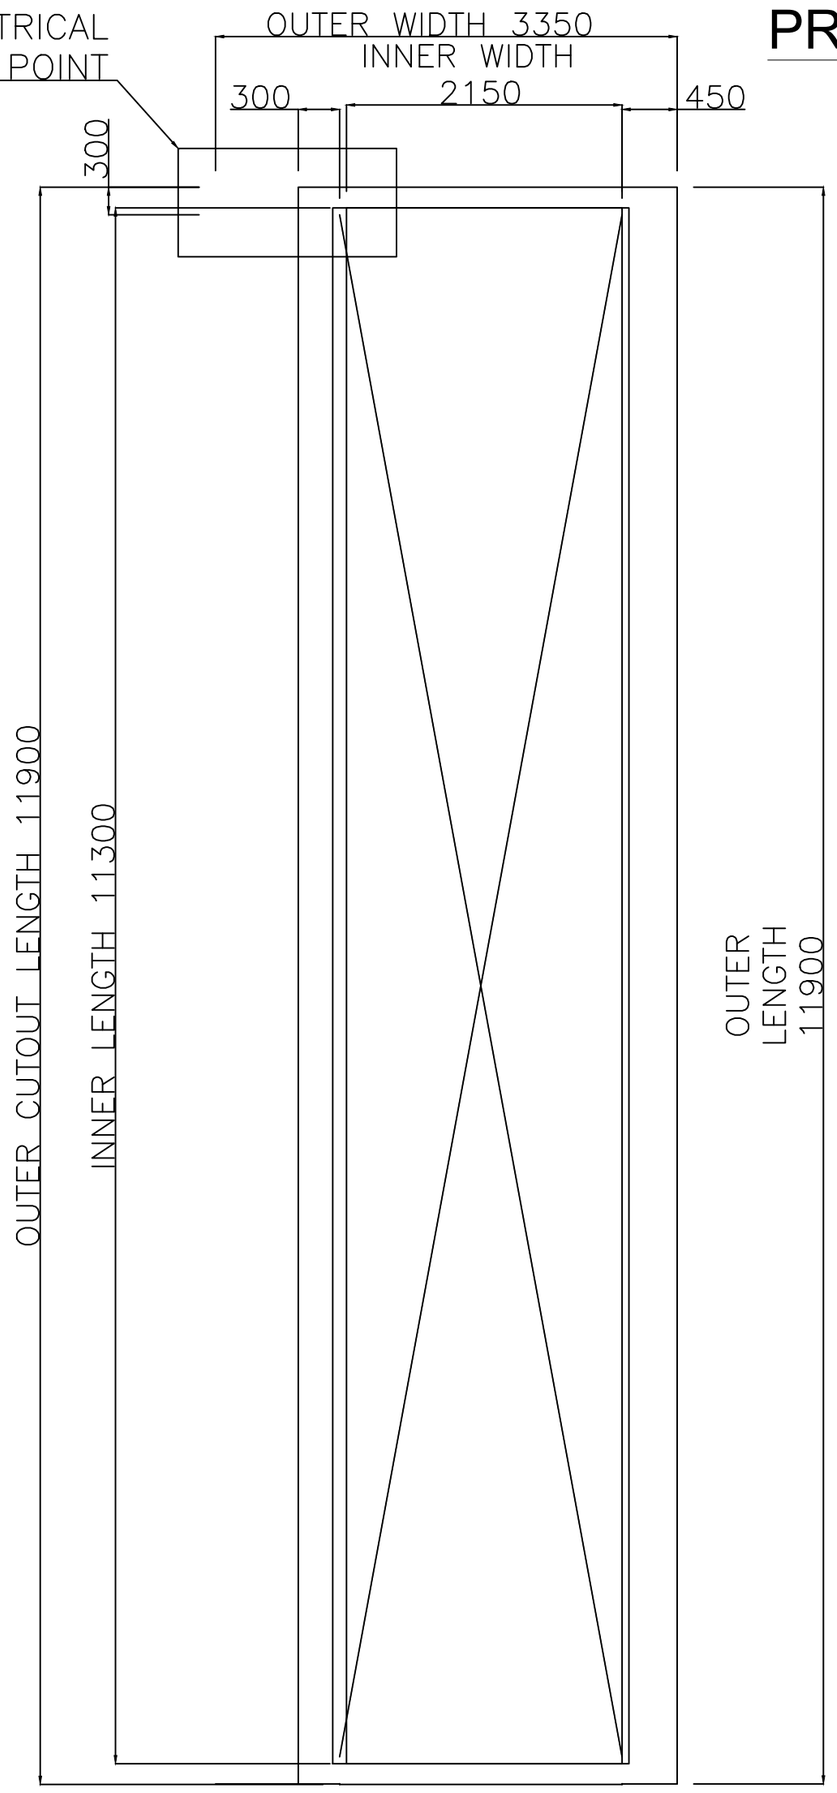

PROPOSED PLAN

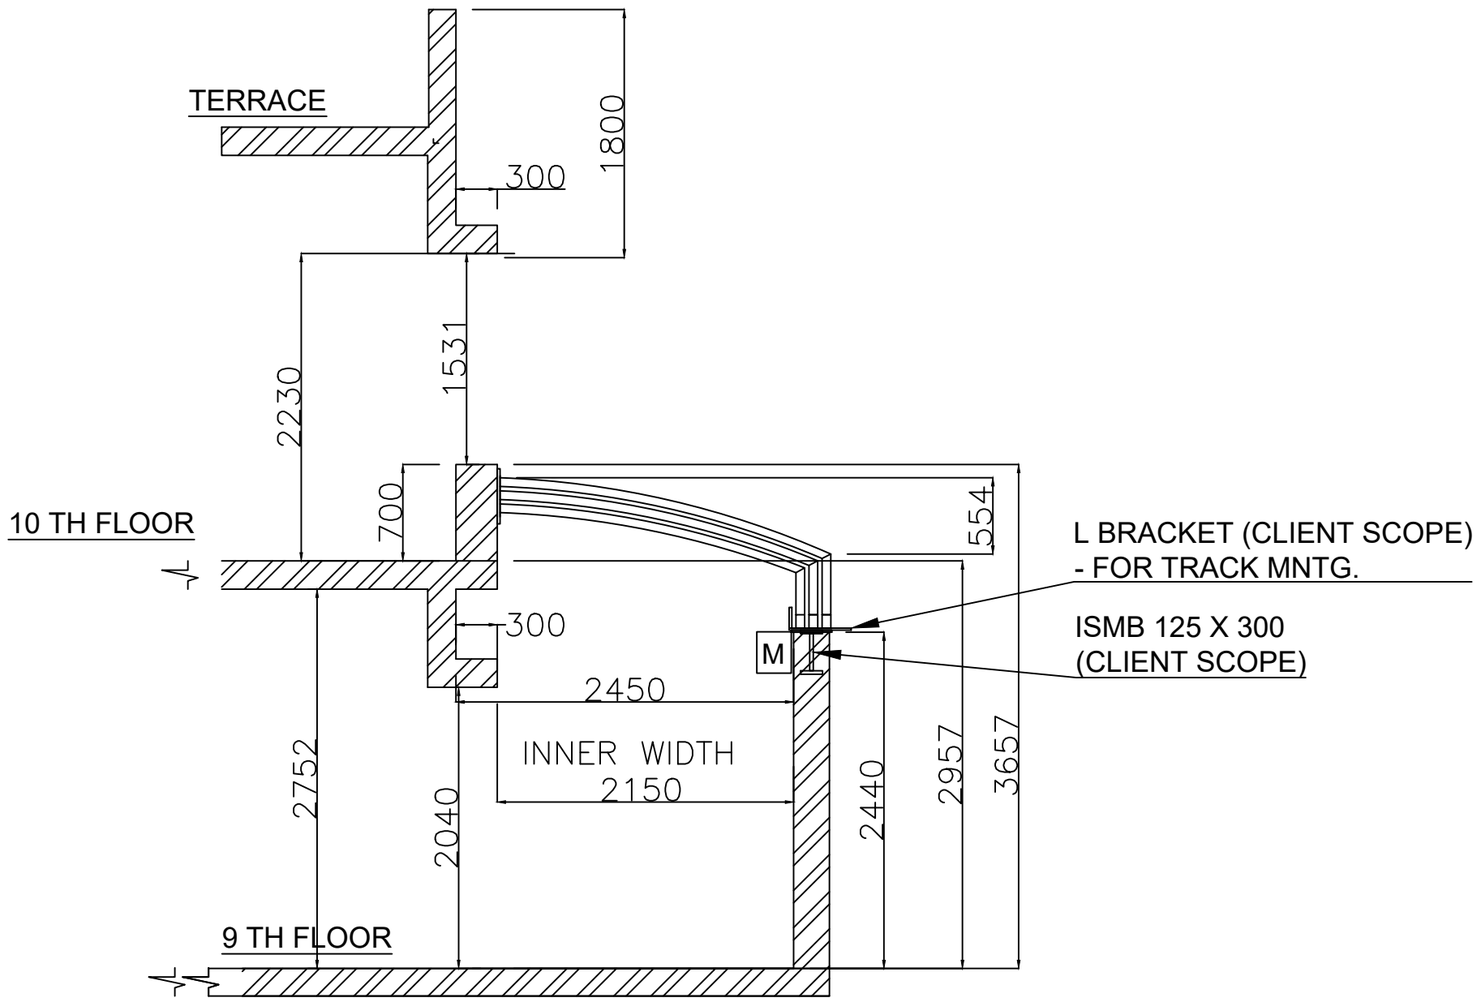

SECTION VIEW

1. THE STRUCTURE AROUND THE CUT OUT SHOULD BE OF FLAT SURFACE FOR PROPER FASTENING OF ROOF.
2. TOP SURFACE SHOULD BE OF PARALLEL / FLAT FOR SMOOTH FUNCTIONING OF ROOF.
3. ROOF EXTENSION IS SHOWN FOR ONLY REFERENCE. IT CAN BE MODIFIED AS PER THE WORK UNDERTAKEN.
4. GRADIENT OF 50MM X 20 MM PLATE NEED TO BE PROVIDED ALONG THE OUTER LENGTH TO AVOID WATER STAGNANCY IN GUIDE RAIL.
5. AL PROFILE - POWDER COATED
6. GASKET - EPDM
7. MOTOR - ITALIAN/GERMAN MAKE
8. ELECTRICAL REQUIREMENT -
9. ALL DIMENSION IN MM.
10. ALL CIVIL WORK / TRACK MOUNTING ARRANGEMENT IS IN CLIENT SCOPE.

This drawing & design is the property of NIHVA TECHNOLOGIES. Not to be sold or copied to any other concern.

TITLE
PROPOSED PLAN LAYOUT

	NAME	SIGN	DATE
DRAWN	MAHESH S.		19.11.22
CHECK	MAHESH S.		19.11.22
APPRD.	VIJAY T.		19.11.22

If any queries contact : projectsautomation@nihva.com

ALL DIMENSION ARE IN mm

NIHVA
NIHVA TECHNOLOGIES PVT. LTD.

NIHVA TECHNOLOGIES
PVT. LTD. PUNE
Tel : 020 66304033
Email:- info@nihva.com
Website:- www.nihva.com

CLIENT - MR. SAMEER MEHTA
PROJECT - RETRACTABLE ROOF
SITE LOCATION- JAMUNA NIKETAN
NIHVA\22-23\00XX | REV- 0
SCALE: NTS | SHEET: 01 OF 01