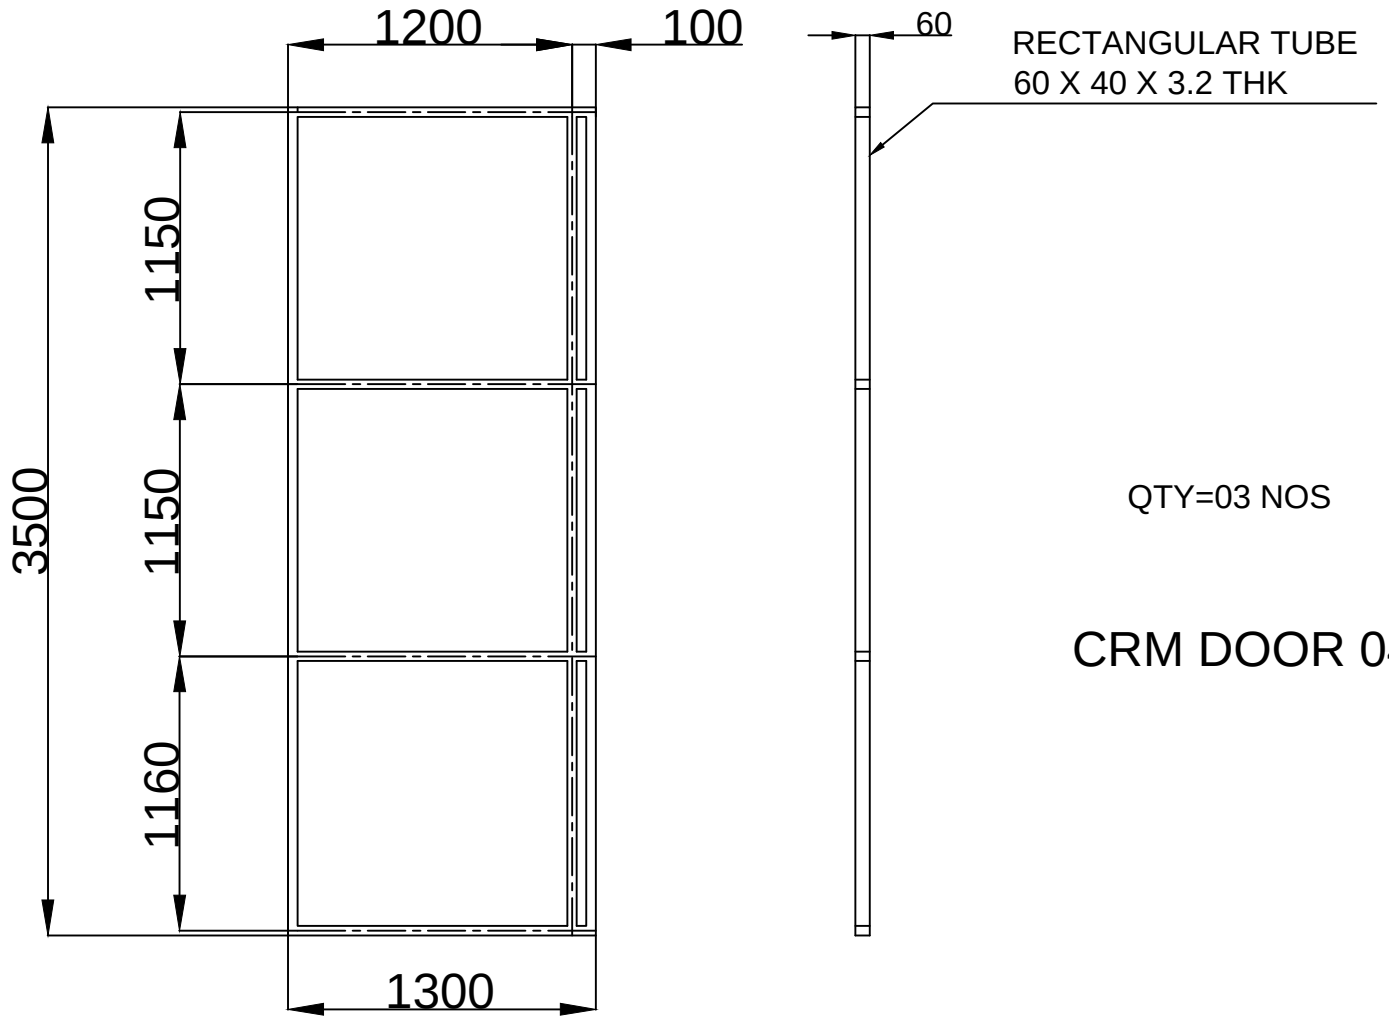

QTY=03 NOS

CRM DOOR 04

This drawing & design is the property of NIHVA TECHNOLOGIES. Not to be sold or copied to any other concern.

TITLE:- 3 LEAF CRM DOOR 04			
	NAME	DATE	SIGN
DRAWN	KISHAN	03/05/2022	
CHECK	M.SUTAR	03/05/2022	
APPRD.			
If any queries contact : design@nihva.com			
ALL DIMENSION ARE IN mm			

NIHVA TECHNOLOGIES PVT. LTD.
NIHVA TECHNOLOGIES PVT. LTD. PUNE
Tel : 020 66304033
Email:- info@nihva.com
Website:- www.nihva.com

CLIENT - NIHVA TECHNOLOGIES PVT.LTD		
LOCATION -		
PRODUCT - SLIDING DOOR		
DWG NO:-NIHVA/22-23/VDR/0015		REV- 0
SCALE: NTS	SCALE:-- 1:1	SHEET: 01 OF 01

	Date	Revised By