
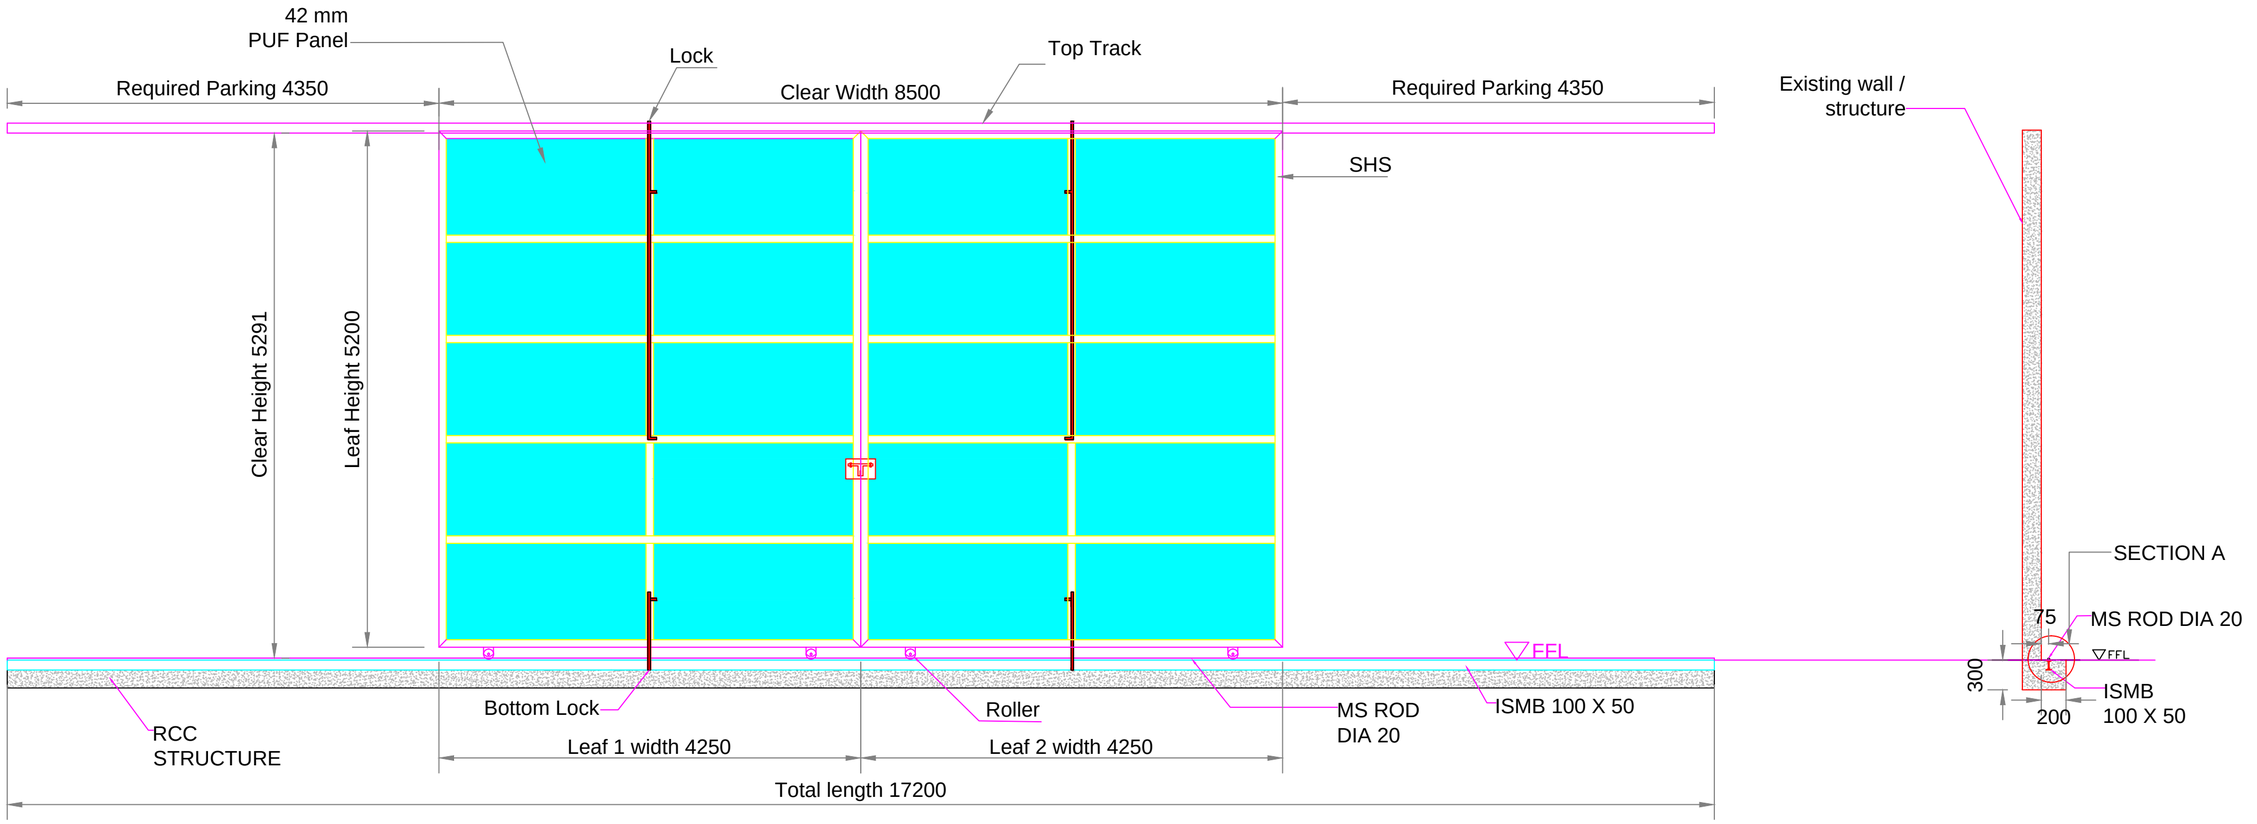


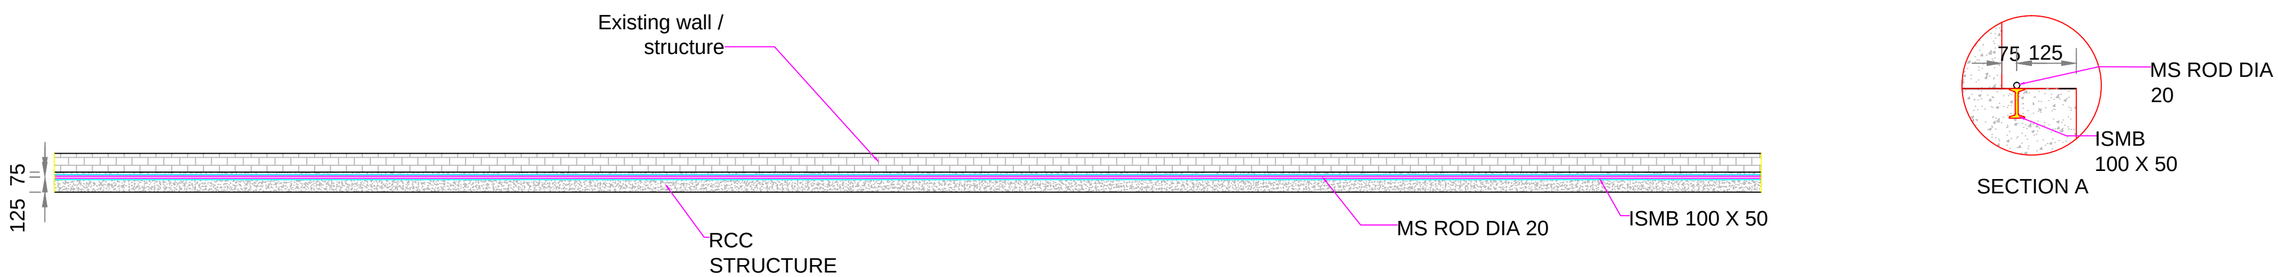

Technical Specs of Sliding Door

1. Parking length required - 4350mm on both sides
2. Bottom Rail - Bright bar Ø20mm
3. ISMB 100 X 50 positioned in the foundation.

Note-

1. All dimension are in mm.
2. All civil work is under client scope.

CLEAR WIDTH(DW)	CLEAR HEIGHT(DH)	QTY
8500mm	5200mm	15 NO

This drawing & design is the property of NIHVA TECHNOLOGIES. Not to be sold or copied to any other concern.

TITLE	SLIDING DOOR WITH FOUNDATION			NIHVA TECHNOLOGIES PVT. LTD. PUNE Tel : 020 66304033 Email:- info@nihva.com Website:- www.nihva.com
	NAME	SIGN	DATE	
DRAWN	G.P.		11.11.21	CLIENT :- Lestech Engineering India Pvt. Ltd.
CHECK	A.K.		11.11.21	PROJECT :- POSCO
				LOCATION :- Mangaon
If any queries contact : design@nihva.com				DWG. NO. :- NIHVA/21-22/0262 / REV:- R00
ALL DIMENSION ARE IN mm				SCALE:NTS / WT: / SHEET:01 OF 01