

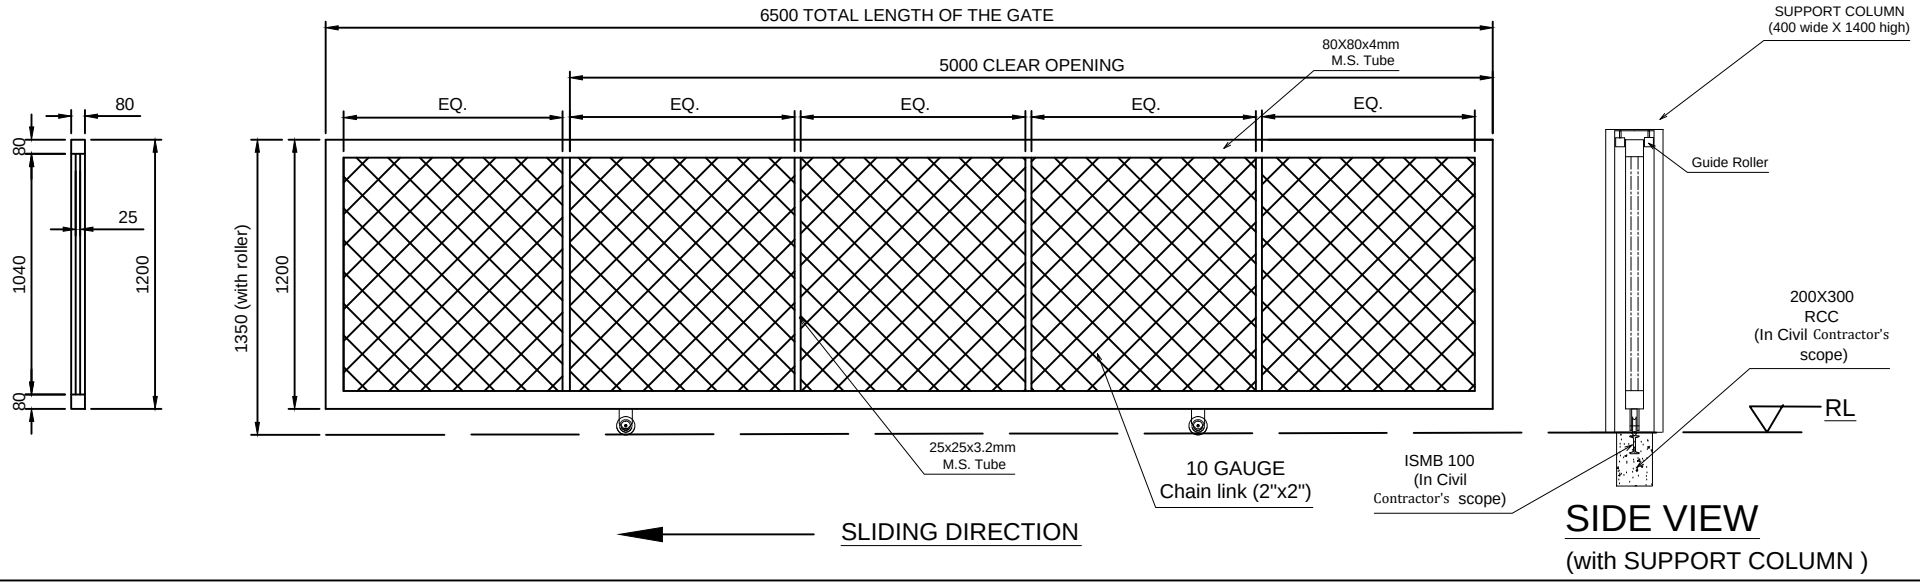


Clear Opening size - 5000X1350mm
Total length of gate - 6500X1350mm
No. Of Column - 4 nos.
Factory paint finish - Red oxide primer coat with Enamel paint Finish
NOTE :- *ALL REQ. CIVIL WORK WILL BE IN YOUR CONTRACTOR'S SCOPE.
NOTE:- As per calculation only 2 wheels are required for Sliding Gate.

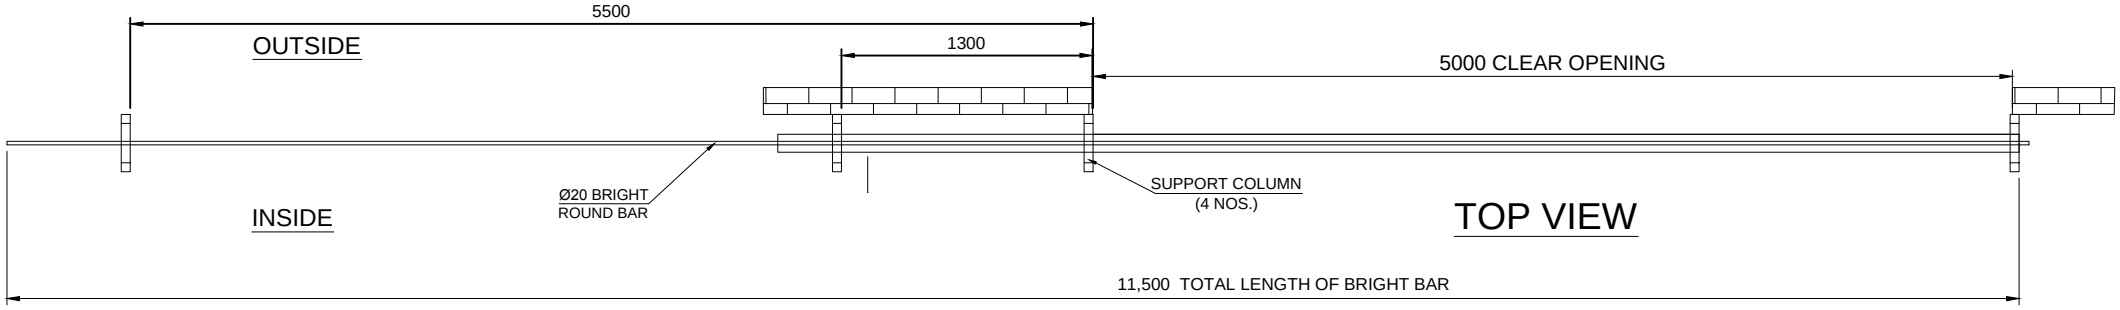

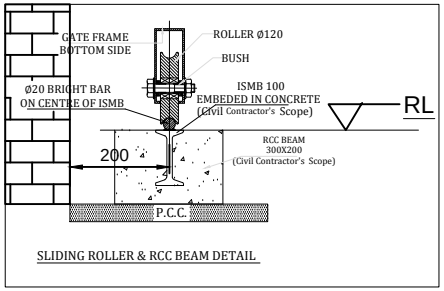

This drawing & designing is the property of NIHVA TECHNOLOGIES. Not be sold or copy to any other concern.

TITLE	FENCED SLIDING GATE		NIHVA TECHNOLOGY PVT. LTD. PUNE
	SIGN	DATE	NIHVA TECHNOLOGIES PVT. LTD.
DRAWN	SUBODH	07/01/16	CLIENT - REWARD CONSTRUCTION
CHECK	ANIL	07/01/16	PROJECT - GIVAUDAN
REV.	00		SITE - RANJANGAON MIDC
APPROVAL	R.Kulkarni	08/01/16	

Tel : 020 66304033
Email:- info@nihva.com
Website:- www.nihva.com

If any queries contact : projects@nihva.com	SCALE: --	WT:	SHEET: 01 OF 01
ALL DIMENSION ARE IN mm			