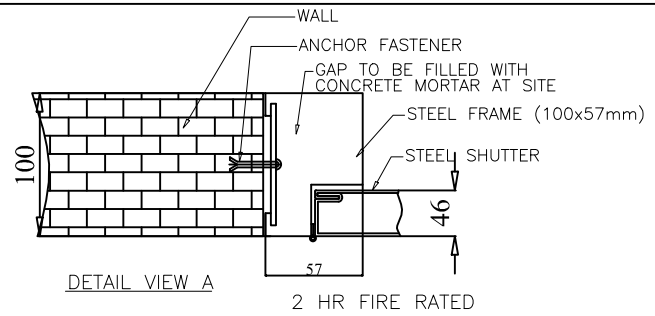


DETAIL VIEW A

2 HR FIRE RATED

NOTES:–

ALL DIMENSIONS ARE IN MM.

A. ABBREVIATION

Wall Opening Width : WOW
Wall Opening Height : WOH
Frame Opening Height : FOH
Frame Opening Width : FOW
Shutter Opening Height : SOH
Shutter Opening Width : SOW

MATERIAL OF CONSTRUCTION
2HRS FIRE RATED
REF STD: IS 3614 PART–2: BS: 476

FRAME : G.I. 1.60mm Sheet
SHUTTER : G.I. 1.20mm Sheet

DOOR THICKNESS : 46mm


FRAME PROFILE : 100 x 57mm (Single Ribet)

INFILL MATERIAL : Rock Wool

PAINT: One Side Red Colour – One Side White

SCHEDULE OF HARDWARE

1) S.S. Ball Bearing Hinges (Yale Make) - 6 Nos.
2) Panic Bar for Double Leaf Door (Yale Make) - 1 Nos.
3) Heavy Duty Door Closer - 2 Nos.
4) Vision Panel with Fire Rated Glass of Size : 200 x 300mm (6mm Thick Fire Glass) - 2 Nos.

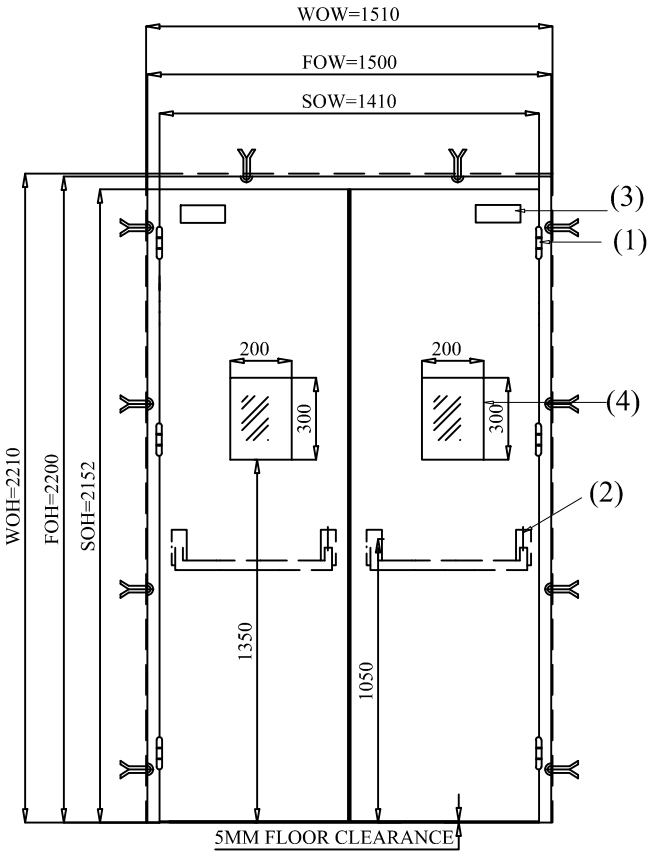

This drawing & design is the property of NIHVA TECHNOLOGIES. Not to be sold or copied to any other concern.

TITLE	1500mm (W) x 2200mm (H) Double Leaf Fire Door			NIHVA TECHNOLOGIES PVT. LTD. PUNE Tel : 020 66304033 Email:- info@nihva.com Website:- www.nihva.com	
	NAME	SIGN	DATE		
DRAWN	S.M.S.		24.11.2020	CLIENT -	
CHECK				PROJECT -	
APPRD.				SITE LOCATION -	
If any queries contact : projectsupport@nihva.com				DWG. NO. : NIHVA/20-21/VDR/0079	REV- R00
ALL DIMENSION ARE IN mm				SCALE: NTS	WT: SHEET: