

DRAWING

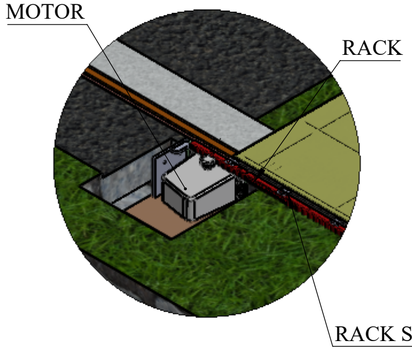





DETAIL A
SCALE 1 : 20

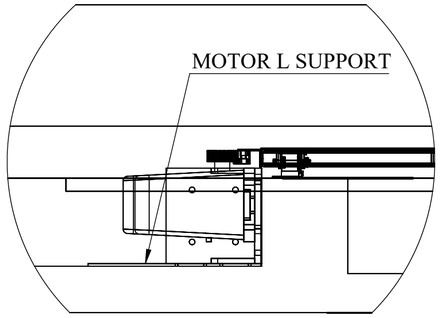

DETAIL B
SCALE 1 : 10

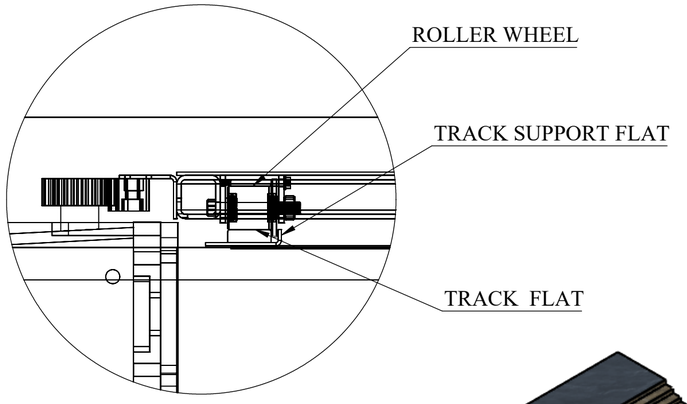

DETAIL C
SCALE 1 : 4

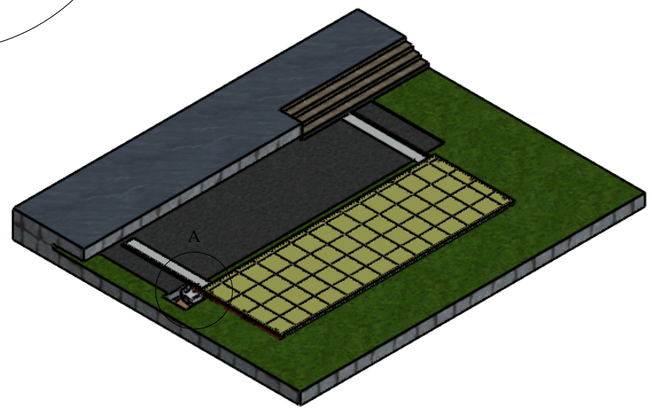





REV DESCRIPTION	DATE	REV NO
	29-07-2025	REV 00
1.		


NOTE :


Keep track clean before the panel movement.

SPECIAL INSTRUCTION'S :

TITLE - SWIMMING POOL ENCLOSER				NIHVA Technologies Pvt. Ltd.	NIHVA TECHNOLOGIES PVT.LTD.PUNE Website - www.nihva.com
DWG NO - NTPL-000-PM-001-00-00-00					
	NAME	SIGNATURE	DATE	PRODUCT - SWIMMING POOL DECK	
DRAWN	V.W.		29-07-2025	PROJECT NO - NTPL-000-PM	REVISION - 00
CHK'D	P.M.		30-07-2025	SITE LOCATION -	WEIGHT -
APPV'D	V.T.		30-07-2025	MATRIAL -	QTY - 1
If any queries contact - design.nihva@gmail.com				PROJECTION METHOD:	SCALE :
ALL DIMENSION ARE IN mm			A2		SHEET 1 OF 7


DRAWING

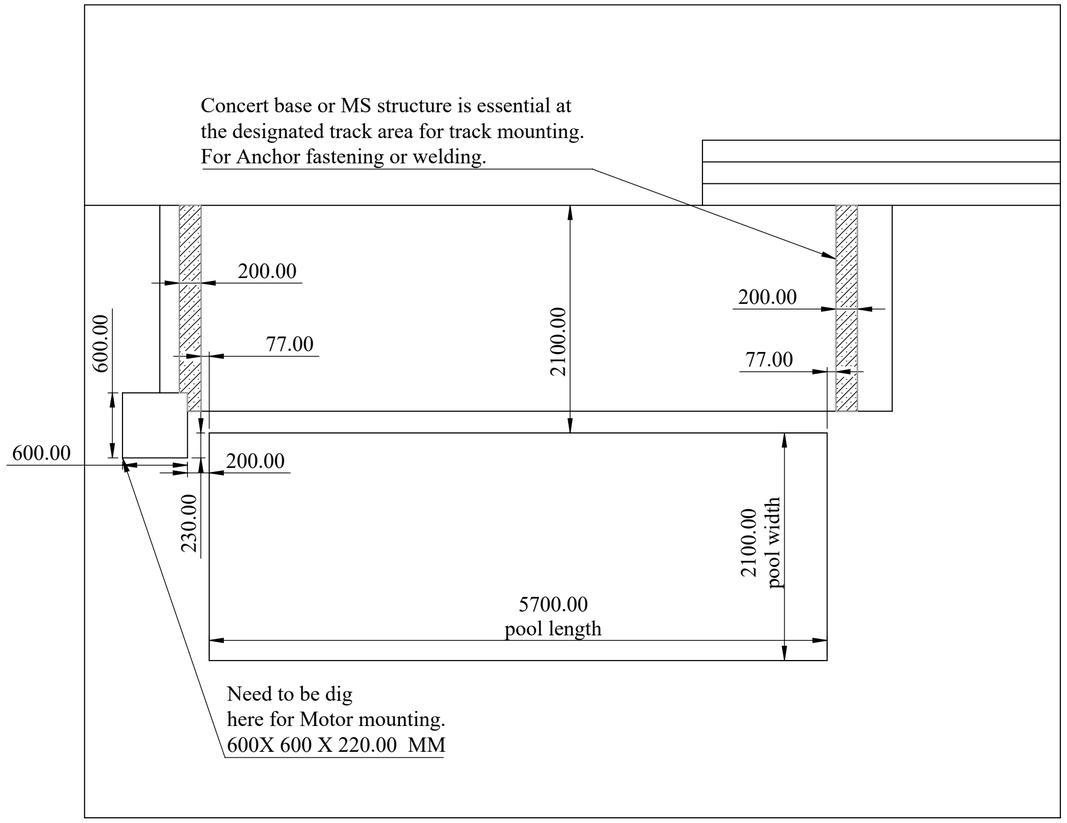


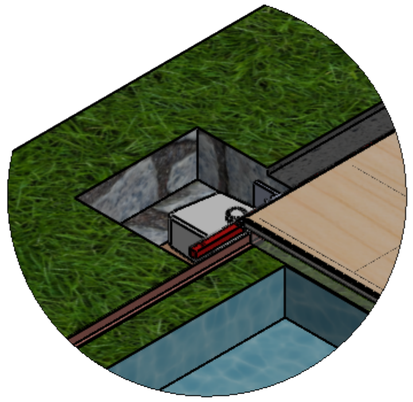


DETAIL G
SCALE 1 : 15

MOTOR ARRANGEMENT

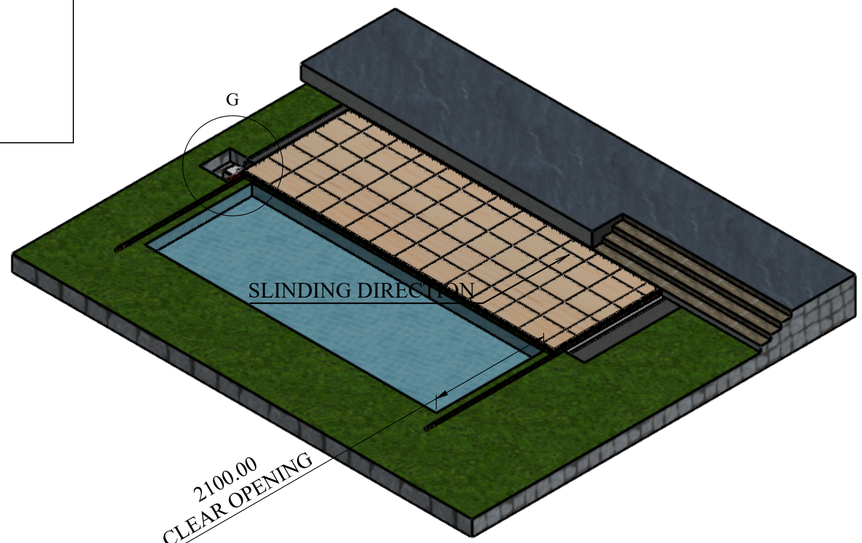

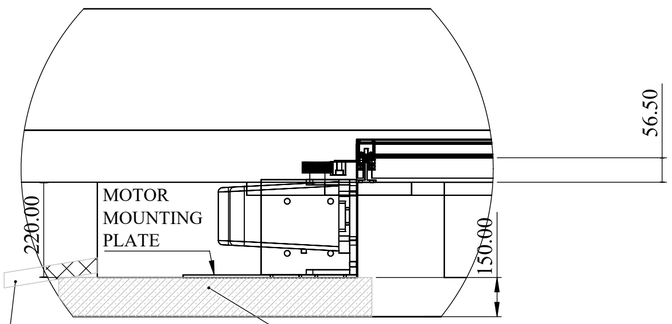

DETAIL K
SCALE 1 : 10

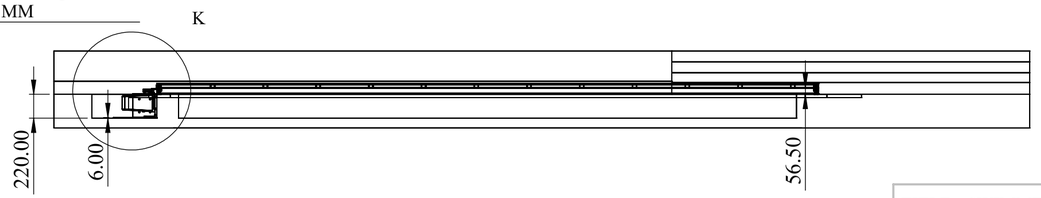

REV DESCRIPTION	DATE	REV NO
	29-07-2025	REV 00
1.		

NOTE :

All civil work is under the end client scope.

SPECIAL INSTRUCTION'S :

TITLE - SWIMMING POOL ENCLOSER

DWG NO - NTPL-000-PM-001-00-00-00

NIHVA TECHNOLOGIES PVT.LTD.PUNE
Website - www.nihva.com

	NAME	SIGNATURE	DATE
DRAWN	V.W.		29-07-2025
CHK'D	P.M.		30-07-2025
APPV'D	V.T.		30-07-2025

PRODUCT - SWIMMING POOL DECK
PROJECT NO - NTPL-000-PM
REVISION - 00
SITE LOCATION -
WEIGHT -
MATRIAL -
QTY - 1
SCALE :
PROJECTION METHOD:
SHEET 2 OF 7


If any queries contact - design.nihva@gmail.com

ALL DIMENSION ARE IN mm

A2

DRAWING

ITEM NO.	PART NUMBER	DESCRIPTION	QTY.
1	CIVIL BASE.._.		1
2	BASE PLATE	SS	2
3	TRACK FLAT 40X12 MM		2
4	FINAL ASM	SS	1
5	SS PLATE 6100 X 2100 X 3 MM THK.._.	SS	1
6	MOTOR MOUNTING ASM		1

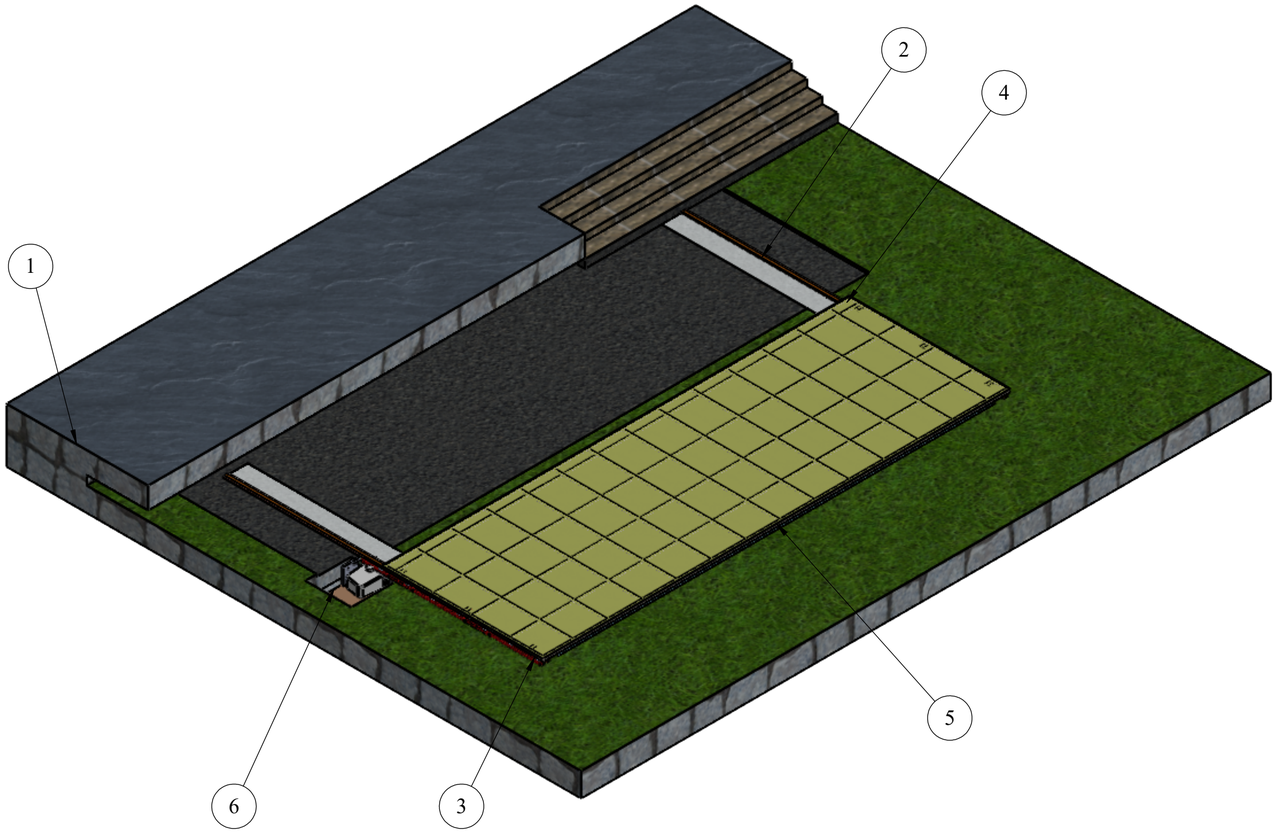

REV DESCRIPTION	DATE	REV NO
	30-07-2025	REV 00
1.		

NOTE :

SPECIAL INSTRUCTION'S :

TITLE - SWIMMING POOL ENCLOSER

DWG NO - NTPL-000-PM-001-00-00-00

NIHVA Technologies Pvt. Ltd.

NIHVA TECHNOLOGIES PVT.LTD.PUNE
Website - www.nihva.com

	NAME	SIGNATURE	DATE
DRAWN	V.W.		30-07-2025
CHK'D	P.M.		31-07-2025
APPV'D	V.T.		31-07-2025

PRODUCT - SWIMMING POOL DECK

PROJECT NO - NTPL-000-PM | REVISION - 00

SITE LOCATION - | WEIGHT -

MATRIAL - | QTY - 1


If any queries contact - design.nihva@gmail.com

ALL DIMENSION ARE IN mm | A2


PROJECTION METHOD:


SCALE :

DRAWING

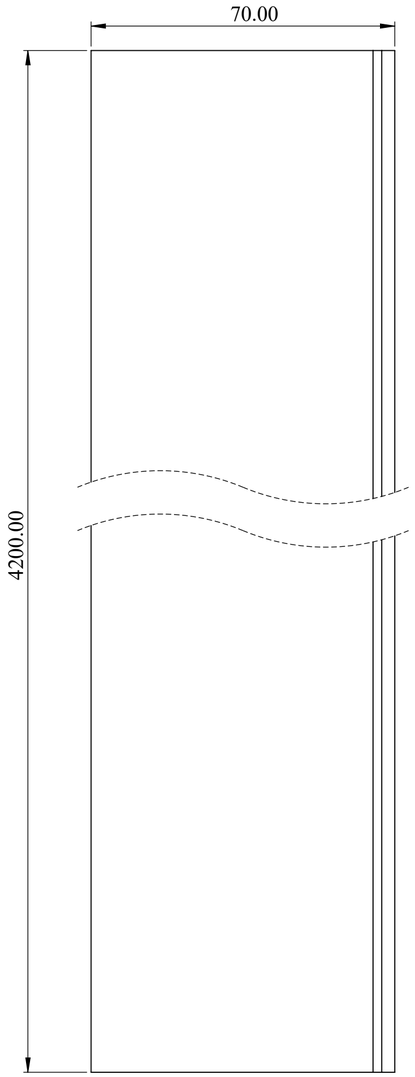

ITEM NO.	PART NUMBER	DESCRIPTION	QTY.
1	BASE PLATE	SS	1

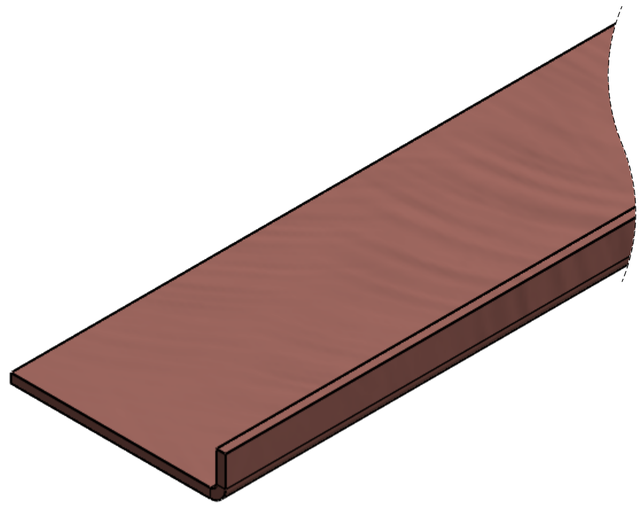

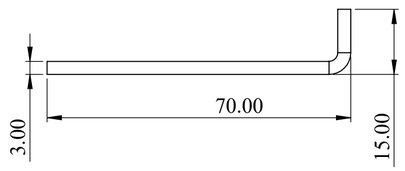

REV DESCRIPTION	DATE	REV NO
	30-07-2025	REV 00
1.		

NOTE :

SPECIAL INSTRUCTION'S :

TITLE - SWIMMING POOL ENCLOSER

DWG NO - NTPL-000-PM-001-00-00-00

NIHVA Technologies Pvt. Ltd.

NIHVA TECHNOLOGIES PVT.LTD.PUNE
Website - www.nihva.com

	NAME	SIGNATURE	DATE
DRAWN	V.W.		30-07-2025
CHK'D	P.M.		31-07-2025
APPV'D	V.T.		31-07-2025

PRODUCT - SWIMMING POOL DECK

PROJECT NO - NTPL-000-PM | REVISION - 00

SITE LOCATION - | WEIGHT -

MATRIAL - | QTY - 1

If any queries contact - design.nihva@gmail.com


ALL DIMENSION ARE IN mm | A2


PROJECTION METHOD:

SCALE :

DRAWING

ITEM NO.	PART NUMBER	DESCRIPTION	QTY.
1	TRACK FLAT	SS	2

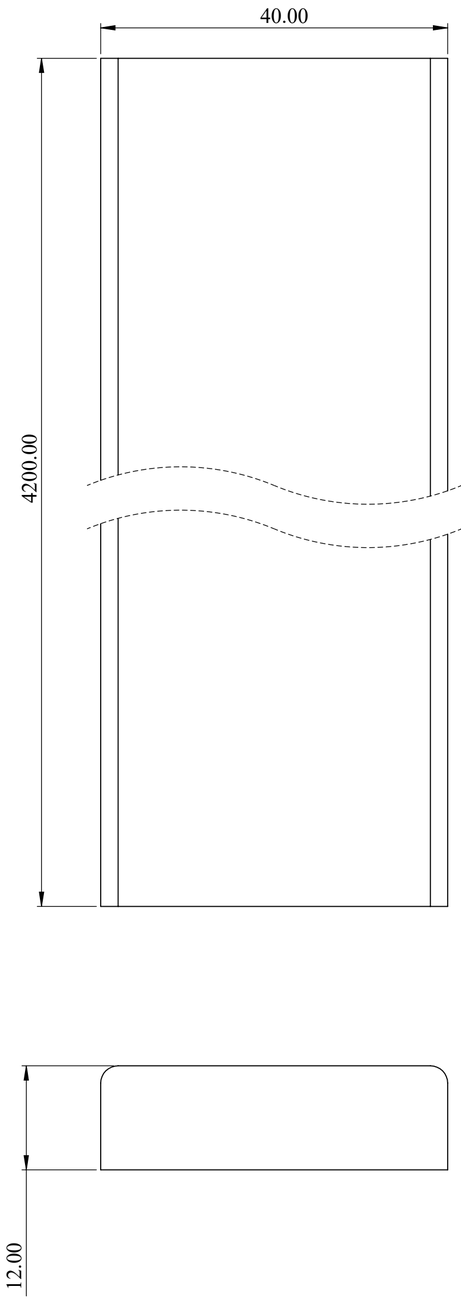

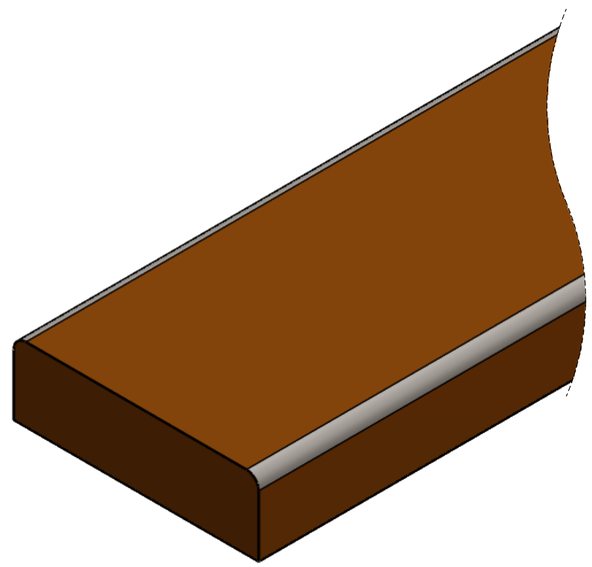

REV DESCRIPTION	DATE	REV NO
	30-07-2025	REV 00
1.		

NOTE :

SPECIAL INSTRUCTION'S :

TITLE - SWIMMING POOL ENCLOSER

DWG NO - NTPL-000-PM-001-00-00-00

NIHVA Technologies Pvt. Ltd.

NIHVA TECHNOLOGIES PVT.LTD.PUNE
Website - www.nihva.com

	NAME	SIGNATURE	DATE
DRAWN	V.W.		30-07-2025
CHK'D	P.M.		31-07-2025
APPV'D	V.T.		31-07-2025

PRODUCT - SWIMMING POOL DECK

PROJECT NO - NTPL-000-PM | REVISION - 00

SITE LOCATION - | WEIGHT -

MATRIAL - | QTY - 1


If any queries contact - design.nihva@gmail.com

ALL DIMENSION ARE IN mm | A2


PROJECTION METHOD:

SCALE :

DRAWING

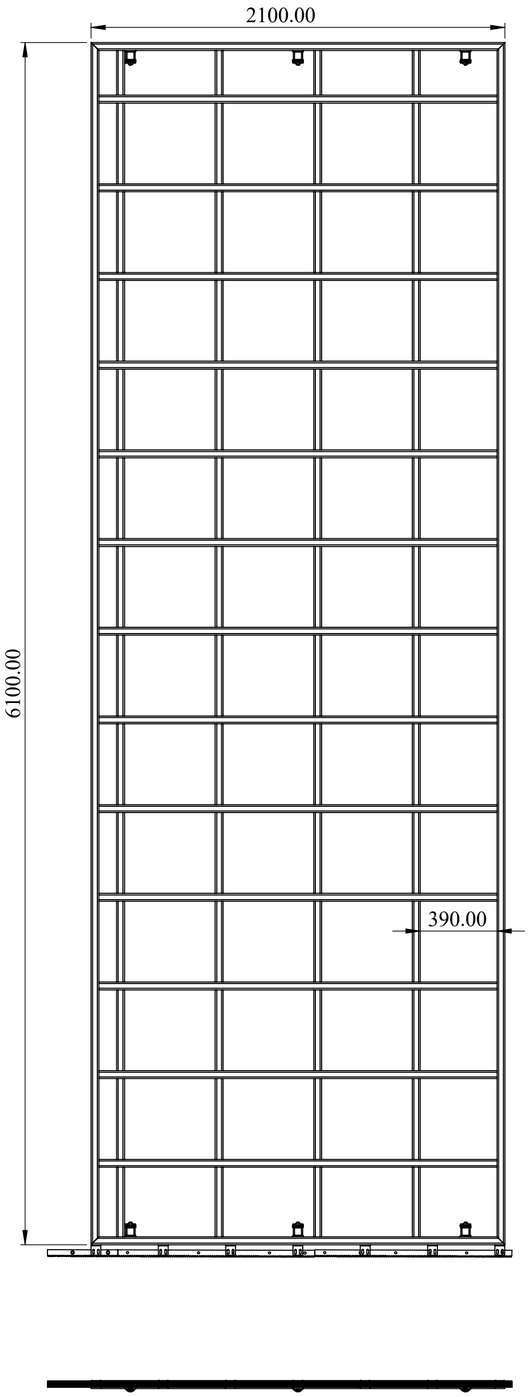

ITEM NO.	PART NUMBER	DESCRIPTION	QTY.
1	PANEL.._.	SS	1
2	ASM WHEEL R		6
3	BOLT	SS	6
4	NUT.._.	SS	6
5	RACK.._.	STD (M4 RACK, 30x8x1000 mm, ZINC COATED WITH SPACERS AND SCREWS.)	2
6	RACK CUT PART.._.	STD (M4 RACK, 30x8x1000 mm, ZINC COATED WITH SPACERS AND SCREWS.)	1
7	RACK SUPPORT PLATE 26-7		7

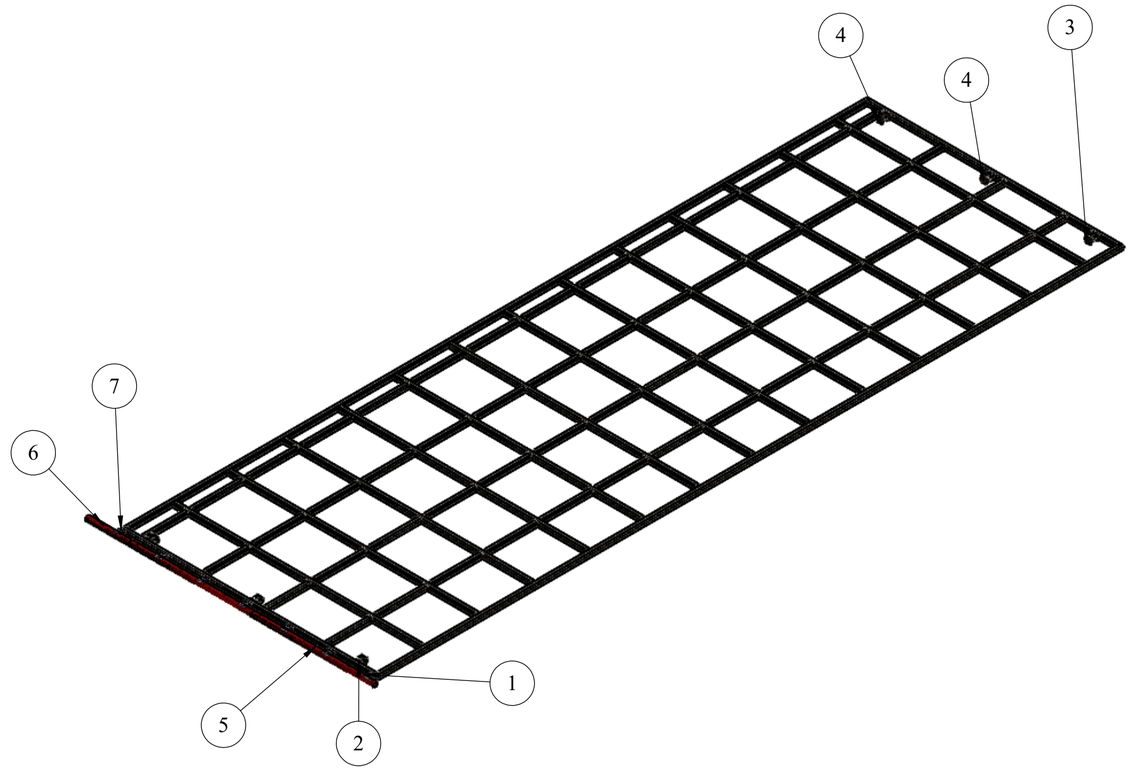

REV DESCRIPTION	DATE	REV NO
	30-07-2025	REV 00
1.		

NOTE :

SPECIAL INSTRUCTION'S :

TITLE - SWIMMING POOL ENCLOSER

DWG NO - NTPL-000-PM-001-00-00-00

NIHVA Technologies Pvt. Ltd.

NIHVA TECHNOLOGIES PVT.LTD.PUNE
Website - www.nihva.com

	NAME	SIGNATURE	DATE
DRAWN	V.W.		30-07-2025
CHK'D	P.M.		31-07-2025
APPV'D	V.T.		31-07-2025

PRODUCT - SWIMMING POOL DECK

PROJECT NO - NTPL-000-PM | REVISION - 00

SITE LOCATION - | WEIGHT -

MATRIAL - | QTY - 1

If any queries contact - design.nihva@gmail.com

ALL DIMENSION ARE IN mm | A2


PROJECTION METHOD:

SCALE :


DRAWING

ITEM NO.	PART NUMBER	DESCRIPTION	QTY.
1	PANEL.._.	SS	1

REV DESCRIPTION	DATE	REV NO
	30-07-2025	REV 00
1.		

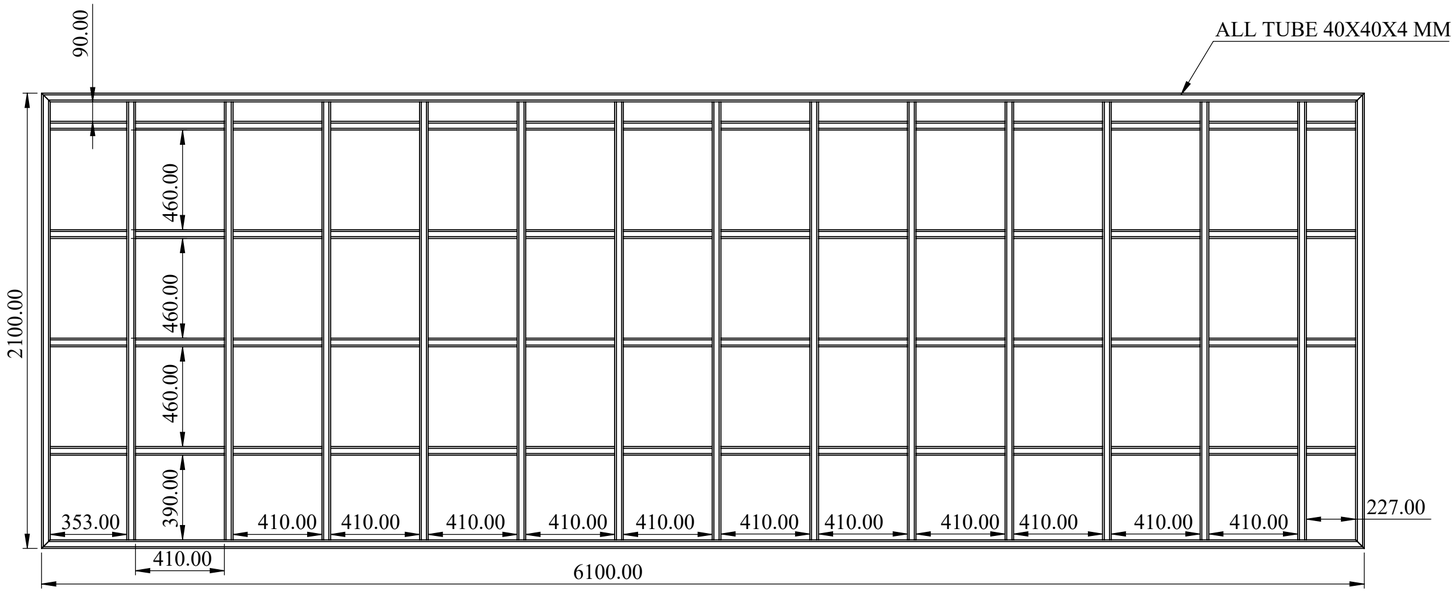



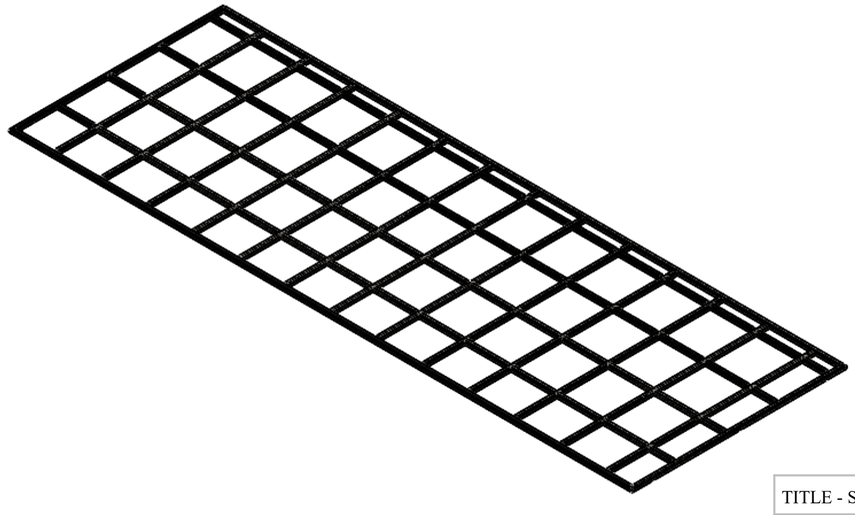

NOTE :

CUTOUT SECTION
Length - 5700 mm
Width - 2100 mm
All tube size - 40X40X4 MM THK
MTL - ss all

SPECIAL INSTRUCTION'S :

TITLE - SWIMMING POOL ENCLOSER

DWG NO - NTPL-000-PM-001-00-00-00

NIHVA TECHNOLOGIES PVT.LTD.PUNE
Website - www.nihva.com

	NAME	SIGNATURE	DATE
DRAWN	V.W.		30-07-2025
CHK'D	P.M.		31-07-2025
APPV'D	V.T.		31-07-2025

PRODUCT - SWIMMING POOL DECK
PROJECT NO - NTPL-000-PM
REVISION - 00
SITE LOCATION -
WEIGHT -
MATRIAL -
QTY - 1
If any queries contact - design.nihva@gmail.com
PROJECTION METHOD:
SCALE :
ALL DIMENSION ARE IN mm
A2