
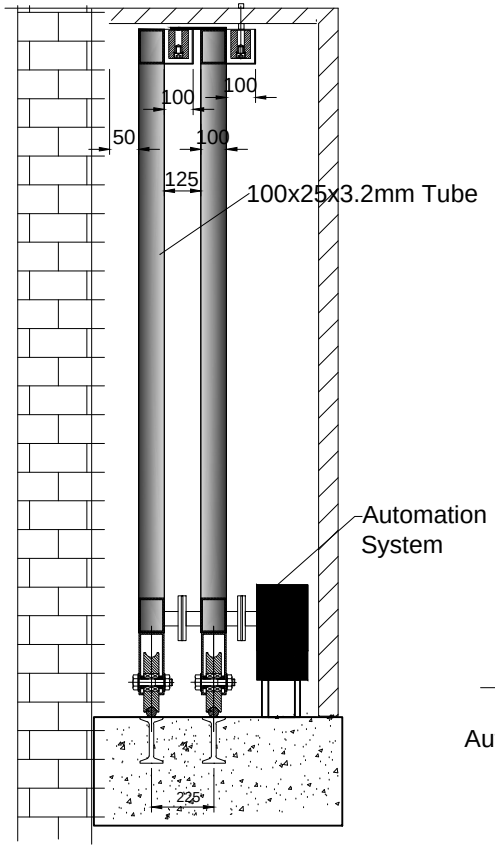



OPENING DIRECTION


6250 clear opening

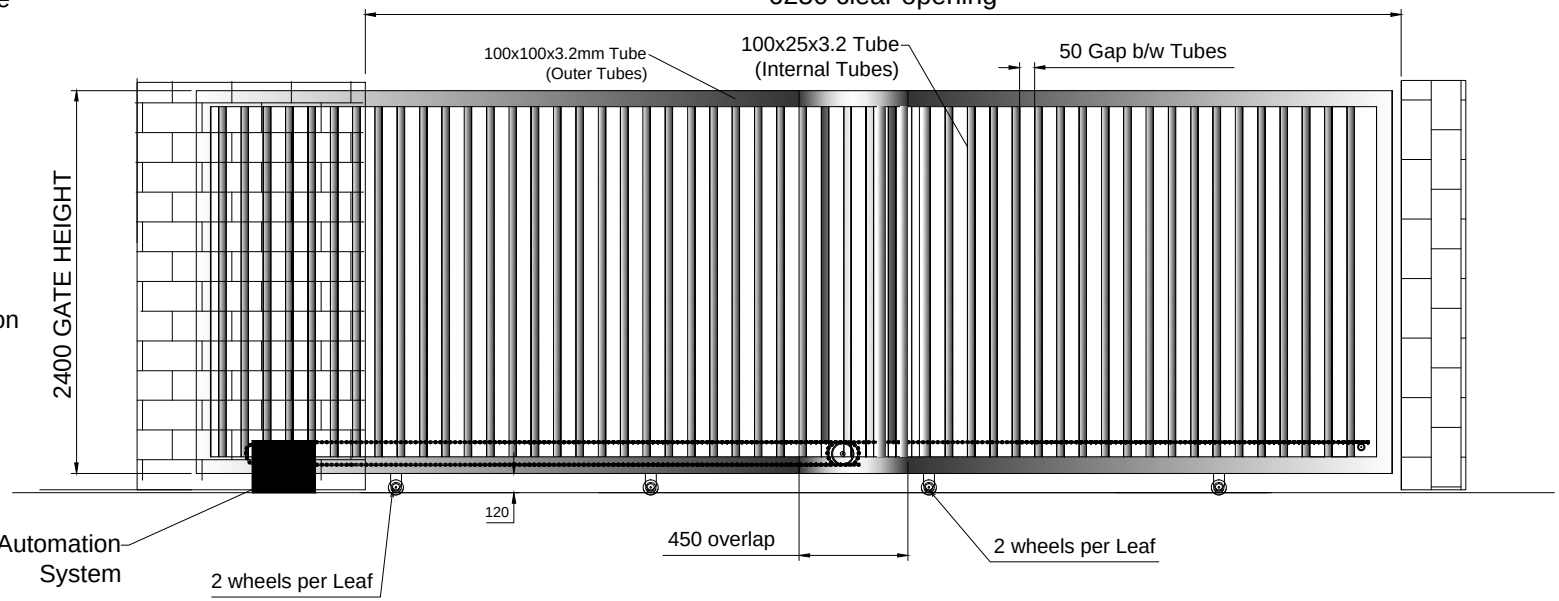

3725

OPENING DIRECTION

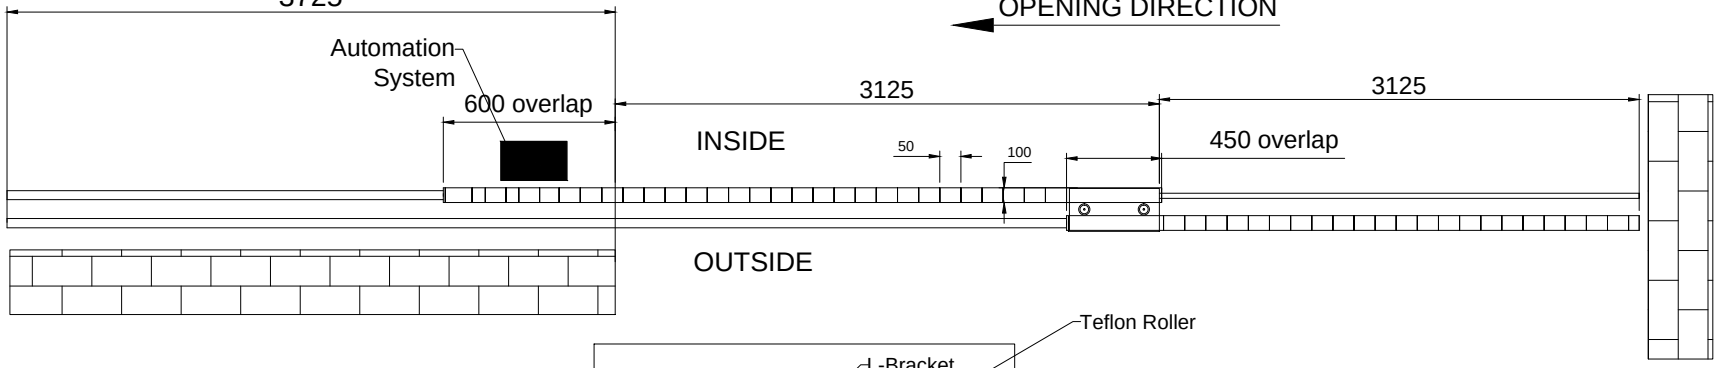

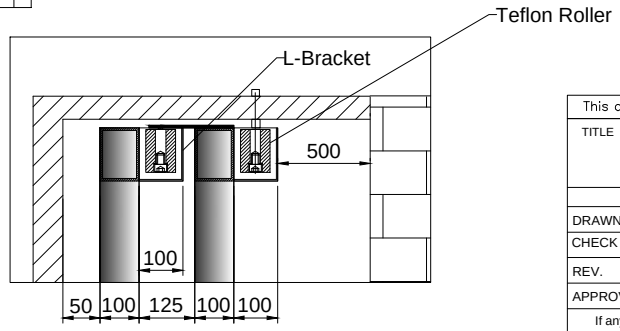

Clear Opening size - 6250mm x 3600mm
Total No. of Leaf - 2 Leaf
Factory paint finish - Red oxide primer coat
NOTE :- *ALL REQ. CIVIL WORK WILL BE IN CLIENT SCOPE.

This drawing & designing is the property of NIHVA TECHNOLOGIES. Not be sold or copy to any other concern.

TITLE	TELESCOPIC SLIDING GATE		NIHVA TECHNOLOGY PVT. LTD. PUNE Tel : 020 66304033 Email:- info@nihva.com Website:- www.nihva.com
	SIGN	DATE	
DRAWN	OMKAR	14/01/16	CLIENT -
CHECK	ANIL	14/01/16	PROJECT -
REV.	01		SITE -
APPROVAL			DWG. NO. : NIHVA/15-16/178
If any queries contact : projects@nihva.com			SCALE: 01 / WT: / SHEET: 01 OF 01
ALL DIMENSION ARE IN mm			