


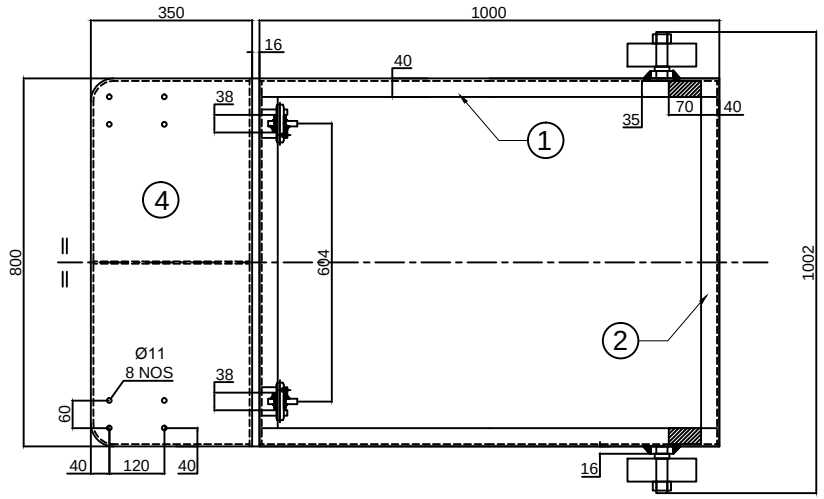


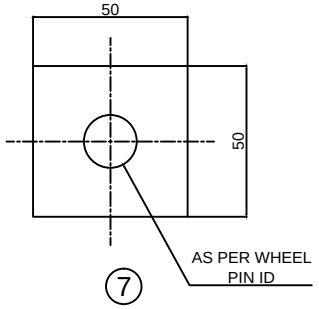


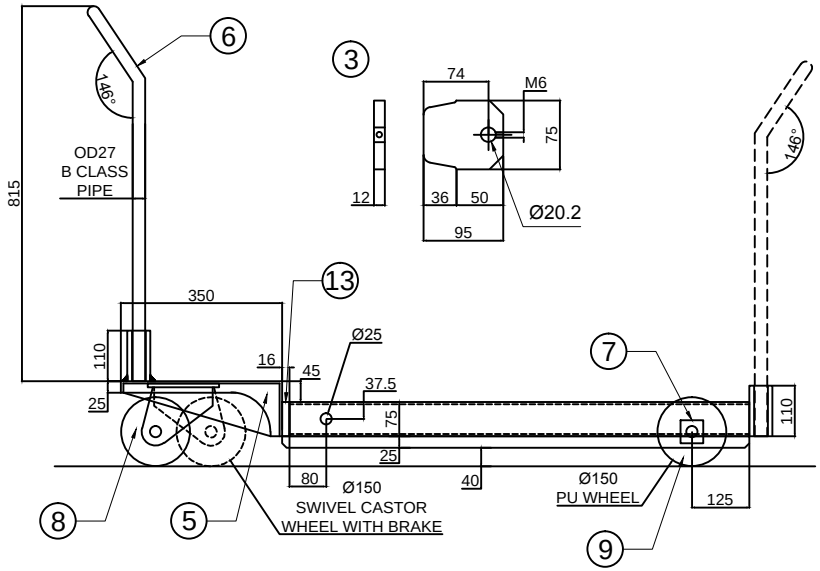

| SR NO | DESCRIPTION | QTY |
|---|---|---|
| 01 | ISMC 75 X 40 X 1000L | 2 NOS |
| 02 | ISMC 75 X 40 X 788L(NOTCH) | 2 NOS |
| 03 | PROFILE 75 X 12 THK X 95L | 4 NOS |
| 04 | BEND 350 X 5 X 800L | 1 NO |
| 05 | RIB 115 X 5 THK X 340L | 3 NOS |
| 06 | PIPE OD27 X 2.65 THK X 2600L | 1 NO |
| 07 | FLAT 50 X 16 THK X 50L | 2 NOS |
| 08 | NYLON WHEEL DIA 150 X 50 MEDIUM DUTY WITH BRAKE & SW CASTOR BRACKET | 2 NOS |
| 09 | NYLON WHEEL DIA 150 X 50 PIN DIA 25 MM | 2 NOS |
| 10 | BUSH ID27 X OD45 X 100L | 4 NOS |
| 11 | GRUB SCREW M6 X 20L | 2 NOS |
| 12 | M10 X 40L NUT BOLT WASHER | 8 NOS |
| 13 | FLAT 75 X 16 X 800L | 1 NO |

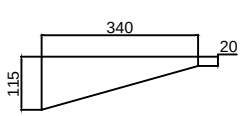


5 1 NO

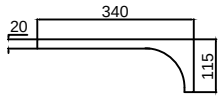


5 2 NOS

This drawing & design is the property of NIHVA TECHNOLOGIES. Not to be sold or copied to any other concern.

TITLE: BASE FRAME ASSEMBLY

| | NAME | SIGN | DATE |
|---|---|---|---|
| DRAWN | P.A | | 25.02.2020 |
| CHECK | G.J | | 25.02.2020 |
| APPRD. | | | |

NIHVA TECHNOLOGIES PVT. LTD.
NIHVA TECHNOLOGIES PVT. LTD. PUNE
Tel : 020 66304033
Email:- info@nihva.com
Website:- www.nihva.com

CLIENT -
PROJECT -
SITE LOCATION -

If any queries contact : design@nihva.com
DWG. NO. : NIHVA/19-20/VDR/331
REV- 0
ALL DIMENSION ARE IN mm
SCALE: NTS
WT:
SHEET: 01 OF 01