
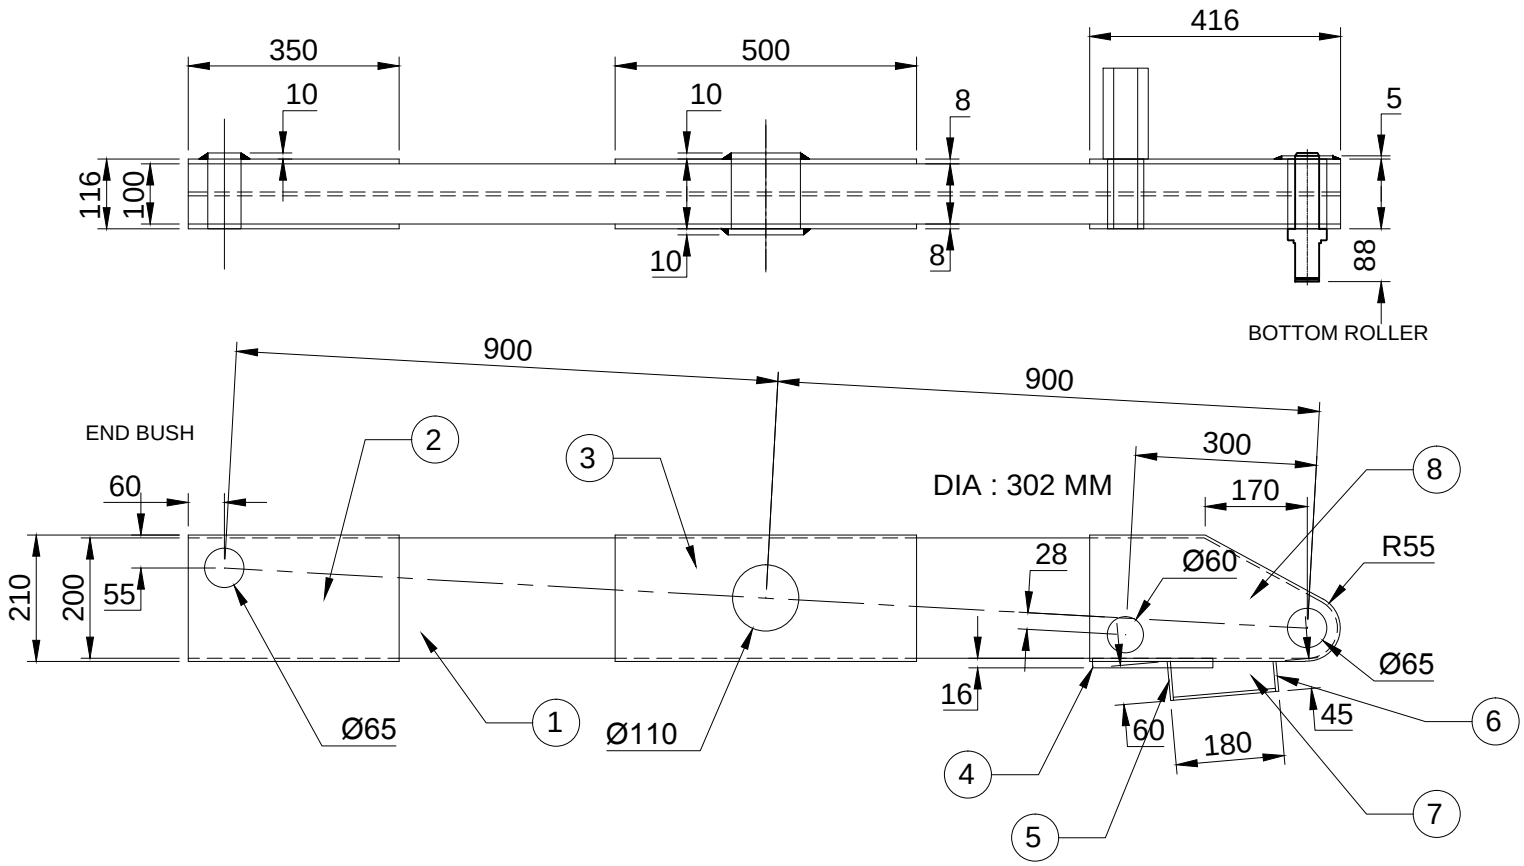


NOTE : MTL = M.S

1. ISMB 200 X 100 X 1915L = 2 NOS
2. PROFILE 210 X 8 THK X 350L = 4 NOS
3. PROFILE 210 X 8 THK X 500L = 4 NOS
4. FLAT 100 X 16 X 200L = 2 NOS
5. FLAT 75 X 6 THK X 116L = 2 NOS
6. FLAT 50 X 6 THK X 116L = 2 NOS
7. FLAT 55 X 10 THK X 170L = 4 NOS
8. PROFILE 210 X 8 THK X 416L = 4 NOS

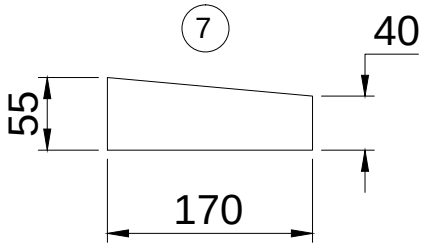

This drawing & design is the property of NIHVA TECHNOLOGIES. Not to be sold or copied to any other concern.

TITLE : -

BOTTOM OUTER SCISSOR

	SIGN	DATE
DRAWN	P.A	10.01.19
CHECK	R.D	10.01.19
REV.		
APPROVAL		

If any queries contact : projects@nihva.com

ALL DIMENSION ARE IN mm

NIHVA TECHNOLOGIES PVT. LTD.

NIHVA TECHNOLOGIES PVT. LTD. PUNE
Tel : 020 66304033
Email:- info@nihva.com
Website:- www.nihva.com

CLIENT -

PROJECT -

SITE -

DWG. NO. : NIHVA/18-19//MFG/NSCL327/06

SCALE: NTS | WT: | SHEET: 01 OF 01