

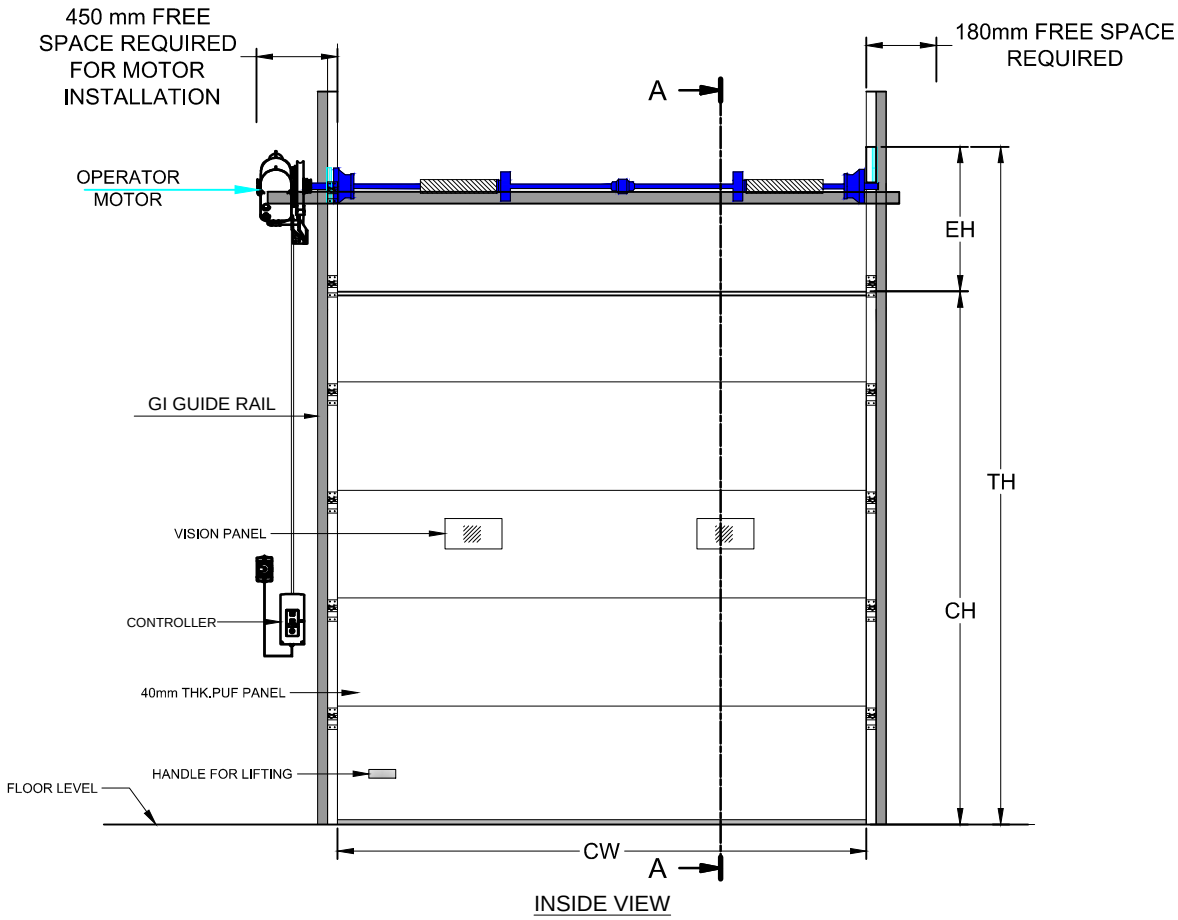


INSIDE VIEW

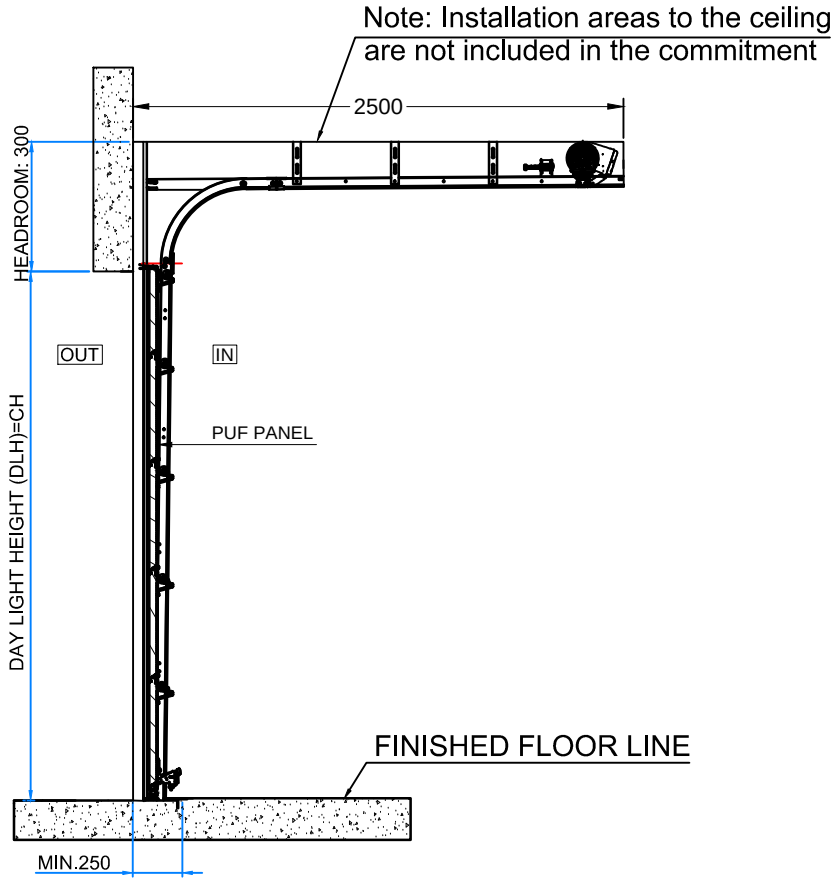

SECTION A-A

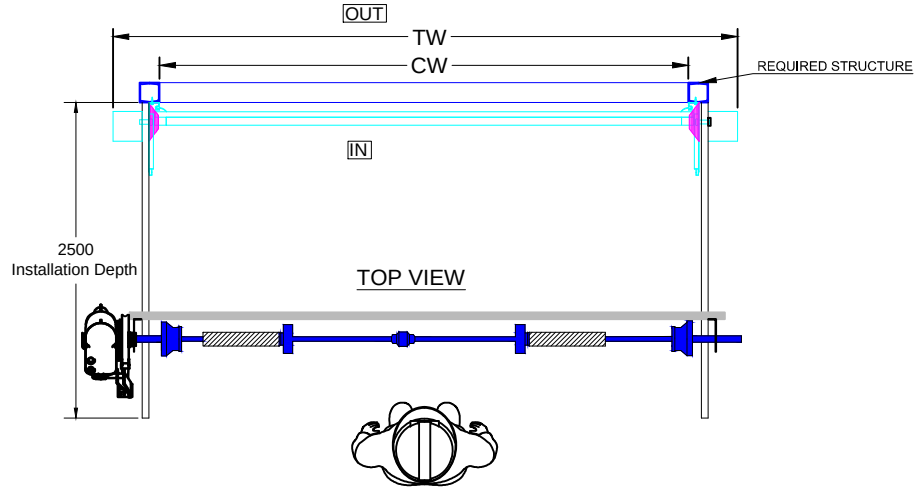

TOP VIEW

TOLERANCE: ± 10mm

SR. NO.	CLEAR WIDTH	CLEAR HEIGHT	QTY	TH	EH	TW
01	2600 mm	2400 mm	1	2700	300	3230

This drawing & design is the property of NIHVA TECHNOLOGIES. Not to be sold or copied to any other concern.

TITLE: SECTIONAL DOOR (LOW LIFTING)

NIHVA TECHNOLOGIES PVT. LTD. PUNE
Tel : 020 66304033
Website:- www.nihva.com Email:- info@nihva.com

	NAME	SIGN	DATE
DRAWN	AKASH		11.01.19
CHECK	VIKRANT		11.01.19
APPROVAL	R.D		11.01.19

CLIENT - SURESBHAI DHEBARIWALA
PROJECT -
SITE - SURAT, GUJRAT
If any queries contact : design@nihva.com
DWG. NO. : NIHVA/18-19/0234 REV: 0
ALL DIMENSION ARE IN mm
SCALE: NTS WT: SHEET: 01 OF 01