

BASE FRAME DETAILS

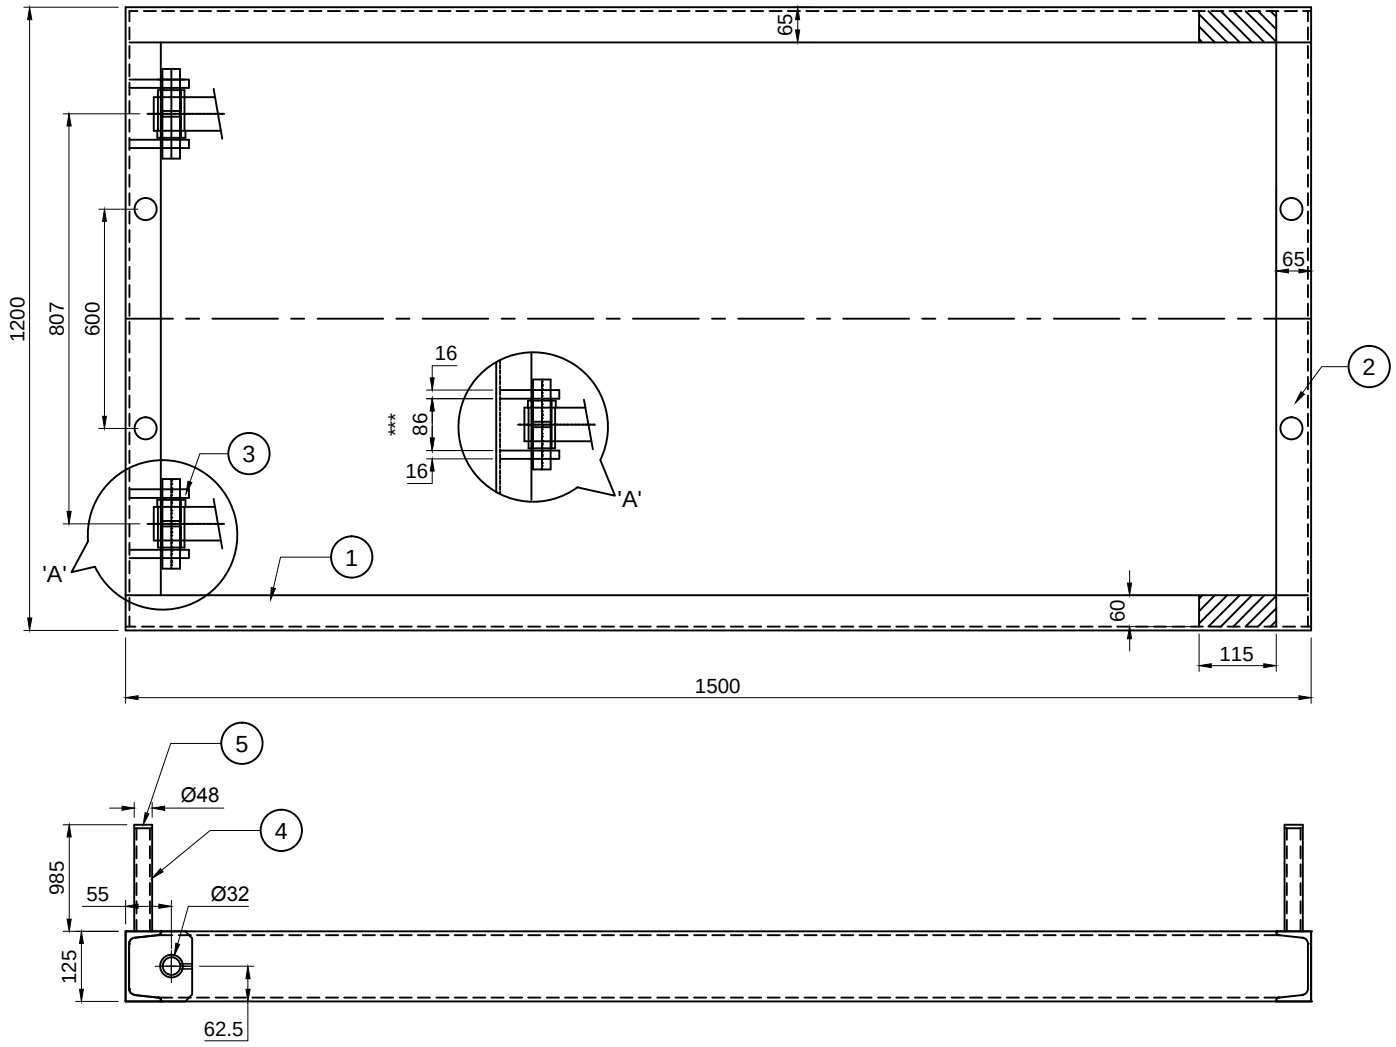

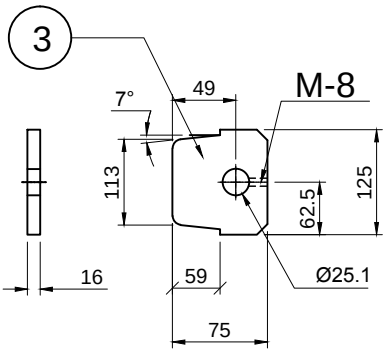

5.	PLATE OD48 X 5 THK	4NOS
4.	PIPE OD48 X 3 THK X 980L	4NOS
3.	FLAT 125 x 16Thk x 80L.M/C-75L	4NOS
2.	ISMC 125 x 65 x 1188L (NOTCH)	2NOS
1.	ISMC 125 x 65 x 1500L	2NOS
SR.NO	DESCRIPTION	QTY.

This drawing & design is the property of NIHVA TECHNOLOGIES. Not to be sold or copied to any other concern.

TITLE : - BASE FRAME ASSLY

NIHVA TECHNOLOGIES PVT. LTD.

NIHVA TECHNOLOGIES PVT. LTD. PUNE
Tel : 020 66304033
Email:- info@nihva.com
Website:- www.nihva.com

	SIGN	DATE	
DRAWN	P.A	04.10.2018	CLIENT -
CHECK	R.D	04.10.2018	PROJECT -
REV.			SITE -
APPROVAL			DWG. NO. : NIHVA/18-19/MFG/NSL/1018/001
If any queries contact : projects@nihva.com			SCALE: NTS | WT: | SHEET: 01 OF 01
ALL DIMENSION ARE IN mm			