
LOCATION - LIBRARY - 01

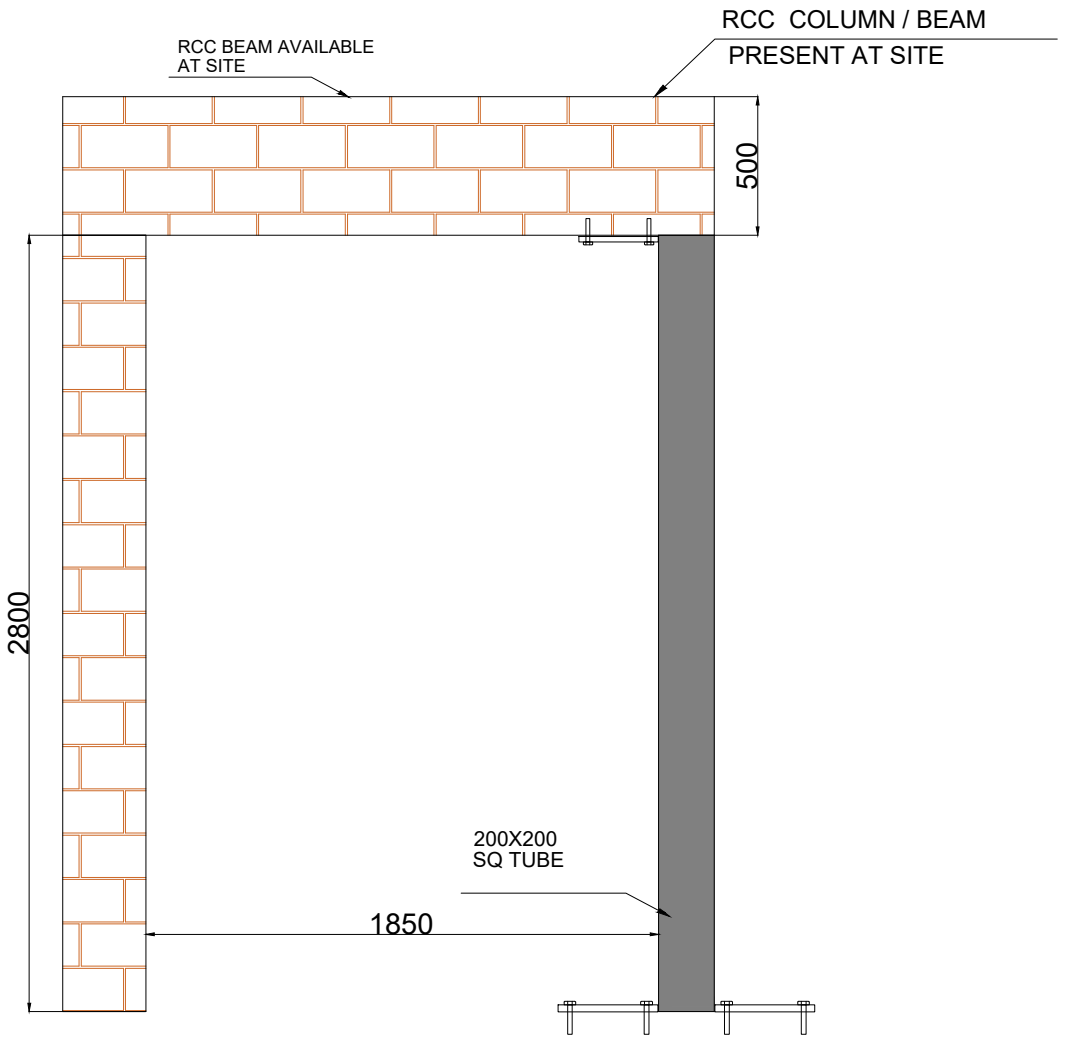


## TECHNICAL SPECIFICATION:-

| SR. | SPECIFICATION | DETAILS |
|---|---|---|
| 1. | DESCRIPTION & DRIVE | MOTORIZED ROLLING SHUTTER (INDIRECT DRIVE) |
| 2. | LOCATION AREA | INSIDE AREA / OUTSIDE AREA |
| 3. | MOUNTING SURFACE | SIDE BRACKETS: OPTIONAL = ON CONCRETE/STEEL&SIDE |
| 4. | SLAT | GI SLAT- 1MM THICK (75 MM WIDTH) |
| 5. | BOTTOM PROFILE | MS PLATE100 x 2.5 MM THICK WITH ANGLE STIFFENER. |
| 6. | GUIDE PROFILE | M.S." T " SHAPED PROFILE 125X3 MM THICK. |
| 7. | HOOD COVER & MOTOR COVER | MADE OF MS SHEET THICKNESS 0.9 MM. |
| 8. | SURFACE FINISH | SYNTHETIC ENAMEL PAINT |
| 9. | PUSH BOTTON | 3 WAY PUSH BUTTON ON SINGLE SIDE |

## SHUTTER SIZES :-

| SR. | CLEAR WIDTH | CLEAR HEIGHT | QTY. |
|---|---|---|---|
| 01 | 1850 mm | 2800 mm | 01 |

NOTE :-

1. All DIMENSIONS ARE IN MM.
2. HIGH LEX BOARD / INTERIOR SHEET/ PUFF PANEL REMOVER OR CUTTING IN CLIENT SCOPE

This drawing & designing is the property of NIHVA TECHNOLOGIES. Not to be sold or copied to any other concern.

TITLE :- MOTORISED ROLLING SHUTTER

NIHVA TECHNOLOGIES PVT. LTD. PUNE
Tel : 020 66304033
Email:- info@nihva.com
Website:- www.nihva.com

NIHVA TECHNOLOGIES PVT. LTD.

| | NAME | DATE |
|---|---|---|
| DRAWN | B.S. | 30/09/2025 |
| CHECK & APPROVAL | V.T. | 30/09/2025 |

PROJECT - MOTORISED ROLLING SHUTTER
FORMAT NO - NIHVA-DD-F-03
DWG. NO. : NIHVA/24-25/MP/1308001 REV-00
SCALE: NTS WT: SHEET: 01 OF 01
ALL DIMENSION ARE IN mm
If any queries contact : design@nihva.com