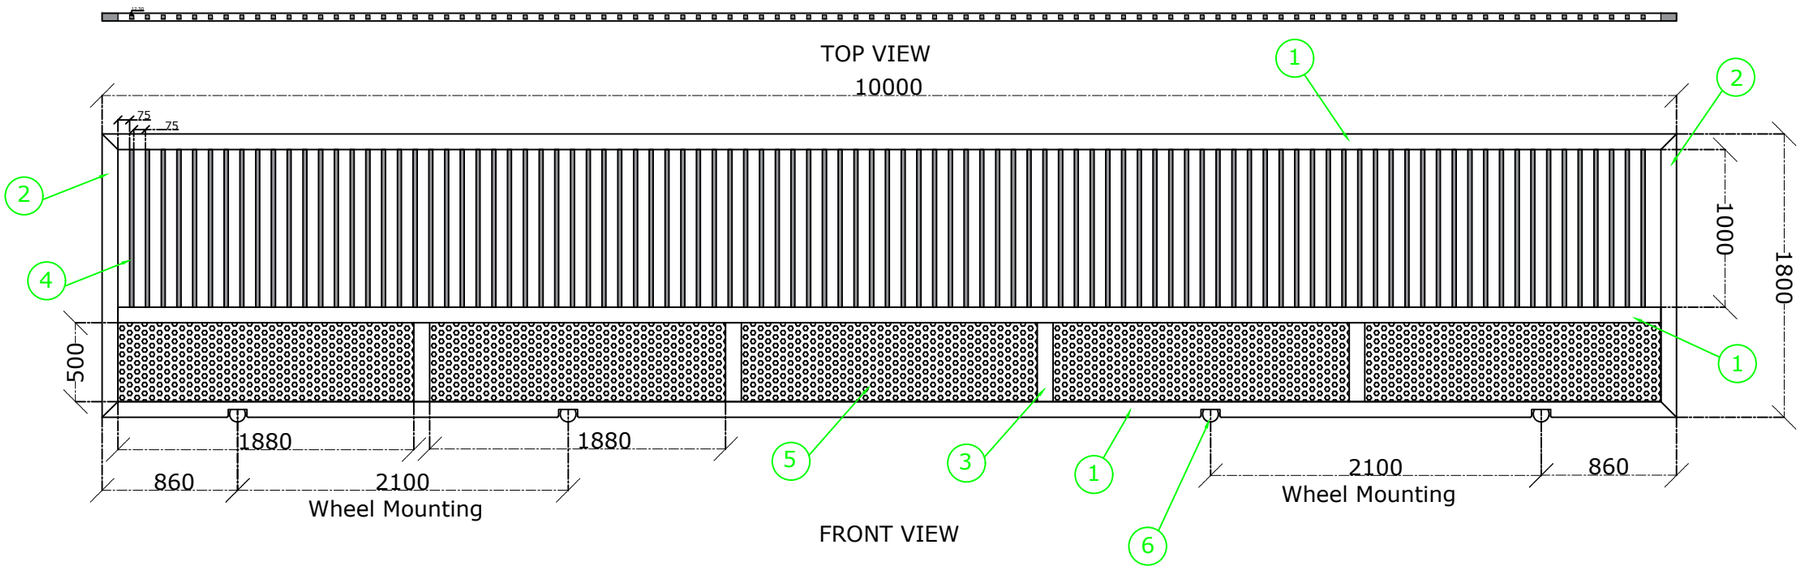


SR.NO	DESCRIPTION	LENGTH (M)	QTY
1	MS.RQ. TUBE 100X50X2.5 THK	10.0	03
2	MS.RQ. TUBE 100X50X2.5 THK	1.8	02
3	MS.RQ. TUBE 100X50X2.5 THK	0.5	04
4	MS.SQ. TUBE 25X25X2.0 THK	1.0	97
5	PERFORATED SHEET 1880X500X2.0mm THK		05
6	BOTTOM SLIDING WHEEL		04

GATE SIZES :-

SR.	CLEAR WIDTH	CLEAR HEIGHT	QTY.
01	10000 mm	1800 mm	01

This drawing & designing is the property of NIHVA TECHNOLOGIES. Not to be sold or copied to any other concern.

TITLE :-
MOTORIZED SINGLE
LEAF SLIDING GATE

NIHVA TECHNOLOGIES
PVT. LTD. PUNE
Tel : 020 66304033
Email:- info@nihva.com
Website:- www.nihva.com

	NAME	DATE
DRAWN	S.J.	18/11/2024
CHECK	K.T.	18/11/2024
APPROVAL	V.T.	18/11/2024

CLIENT - REWARD CON.
PROJECT - MOTORIZED SINGLE LEAF SLIDING GATE
FORMAT NO - NIHVA-DD-F-03
DWG. NO. : NIHVA/24-25/XX00 REV-00
SCALE: NTS WT: SHEET: 01 OF 01
ALL DIMENSION ARE IN mm
If any queries contact : design@nihva.com