



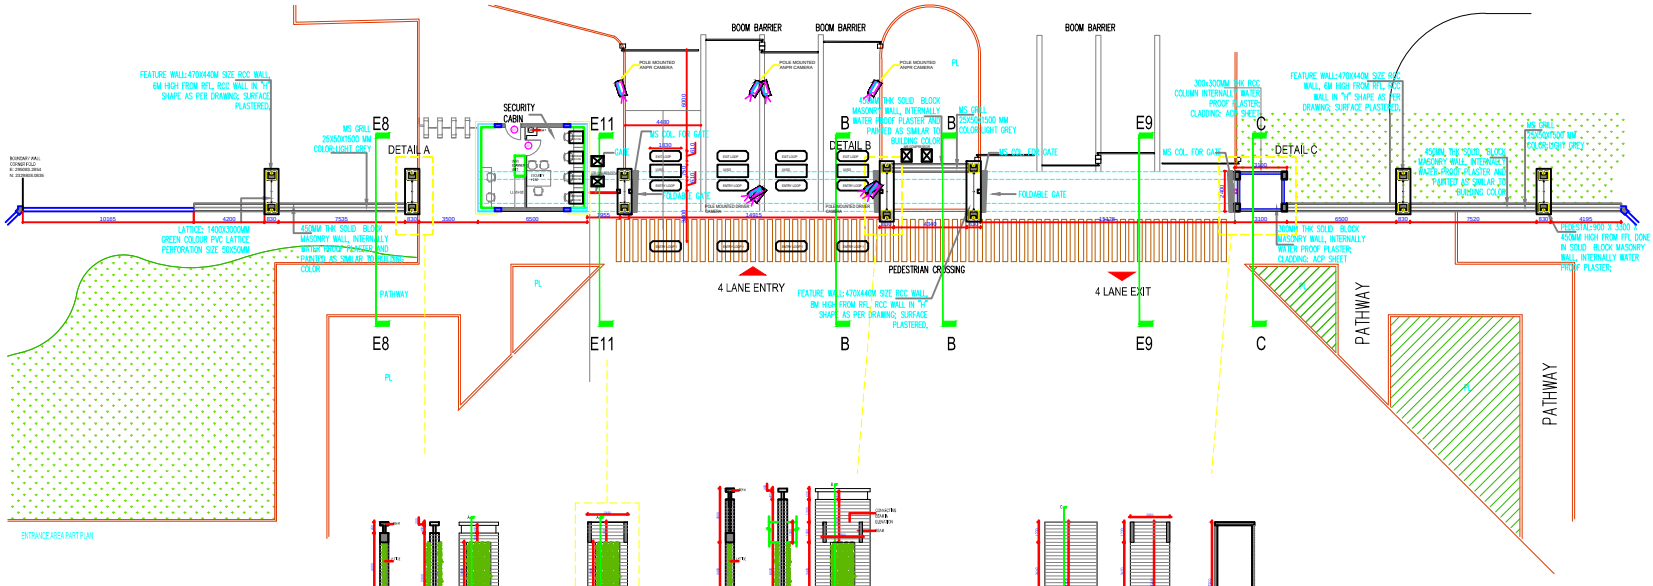

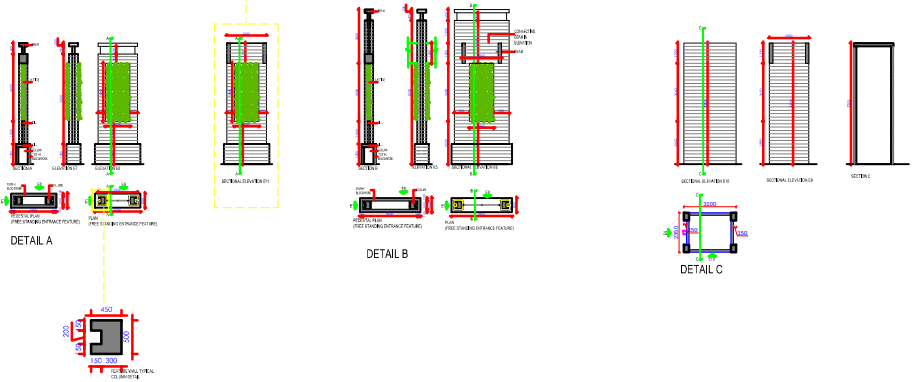

GENERAL NOTES

1. ALL DIMENSIONS ARE IN MILLIMETRES
2. DIMENSIONS ARE TO BE READ AND NOT TO BE SCALED.
3. THE CONTRACTOR MUST VERIFY ALL DIMENSIONS ON SITE AND REFER THE RELEVANT STRUCTURAL AND OTHER CONSULTANT'S DRAWINGS BEFORE COMMENNCING ANY WORK OR PREPARING ANY SHOP DRAWING, AND INCASE ANY DISCREPANCY IS NOTICED THE SAME SHALL BE BROUGHT TO THE NOTICE OF ARCHITECT AND
4. FOR TOILETS, STAIRCASES, DOOR WINDOWS,CURTAIN WALLS REFER SEPARATE DETAIL DRGS.

Client :

ARCHITECT :

RKA

Civil & Structural Engineer :

Plumbing & Fire fighting :

HVAC :

Dew point Consultant Pvt. Ltd.
Suite : TA 8 & 10, Crown Plaza, Mathura road, sector-15A
Faridabad - 121003, Haryana, India
Tel : (0129) - 4072278-9, Fax : (0129)-4072278
E-mail : promod@dewpoint.biz

Electrical :

T.S.Sethi and Engineering Associates
701, Vatika City point, M.G.Road, Sector-25, Gurgaon - 122002
Gurgaon - 122002, Haryana
Tel/Fax : (0124)-4010874, 4010875, Mob : 9810004257
E-mail : tssethi@tssea.net

Project title :

WORKING DRAWINGS

drawing title

ENTRANCE AREA BOUNDARY WALL DETAILS

Stage	WORKING DRAWINGS	Stage	
checked by		checked by	
date	11-10-2017	approved by	
drawing no.	A-MD-WD-102a	revision	R0

THIS DRAWING IS COPYRIGHT