

THIS PRINT IS THE PROPERTY OF NIHVA TECHNOLOGIES PVT LTD
RETURNED UPON REQUSETTHIS PART MUST NOT BE SOLD TO ANY OTHER CONCERN

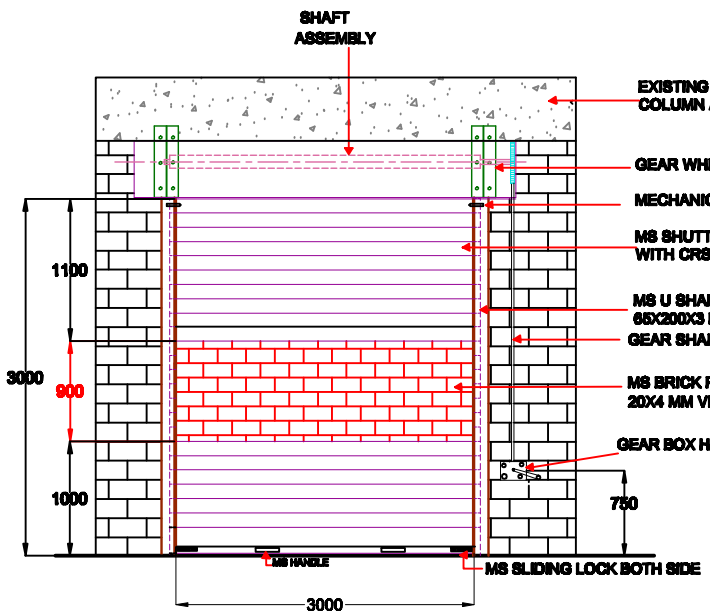



INSIDE ELEVATION

Clear Opening size:-
(W)3.0m x (H)3.0m

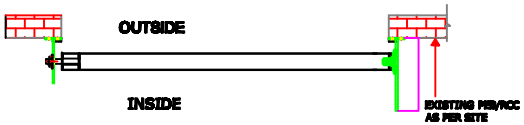


PLAN

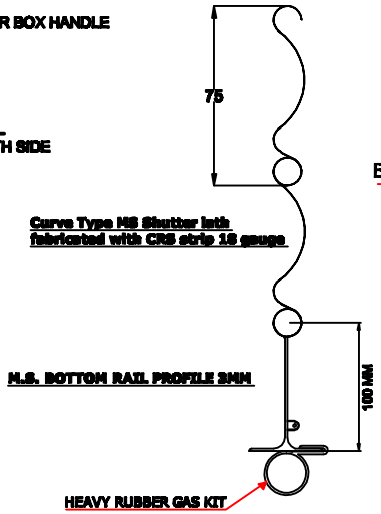


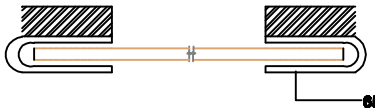

Side guide

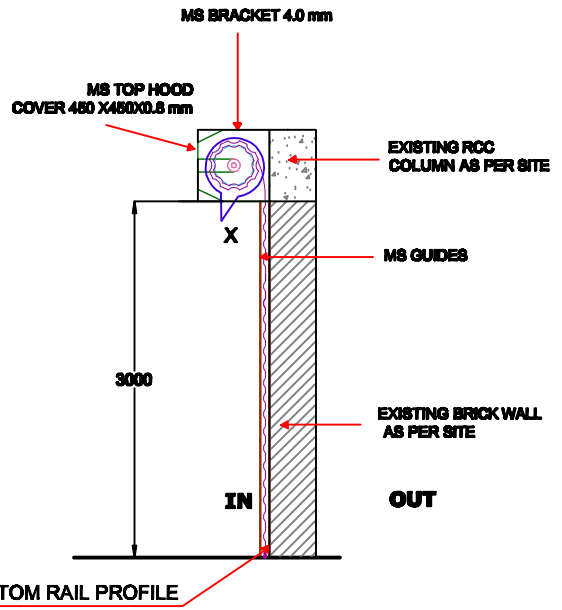

SIDE VIEW

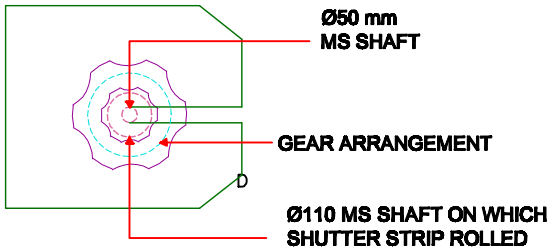

Bracket

Location :- Substation
Size :- 3.0m(W) X 3.0M (H)

TITLE: Grilled Manual Gear Operated Rolling Shutter - GRS 1	DO NOT SCALE DRAWING		NIHVA TECHNOLOGIES PVT. LTD. Pune:-411044 Tel :- 020 66304033 Email :- info@nihva.com
		SIGN / DATE	
CLIENTS APPROVEL:-	DRAWN	ABHIJIT / 20/01/15	
	CHECK	Anil / 20/01/15	CLIENT: REWARD CONSTRUCTION
	ENG		PROJECT / SITE: IR PROJECT/ NAROL - AHEMDABAAD
	APPRD.		PRODUCT NAME:
ALL DIMENSION ARE IN M.M.	PROD		DWG. NO.: NVA/REWARD/01/R2
	MFG		REV.: 0
	Ref. No.		SCALE: NTS / WT: / SHEET: 1 OF 1