
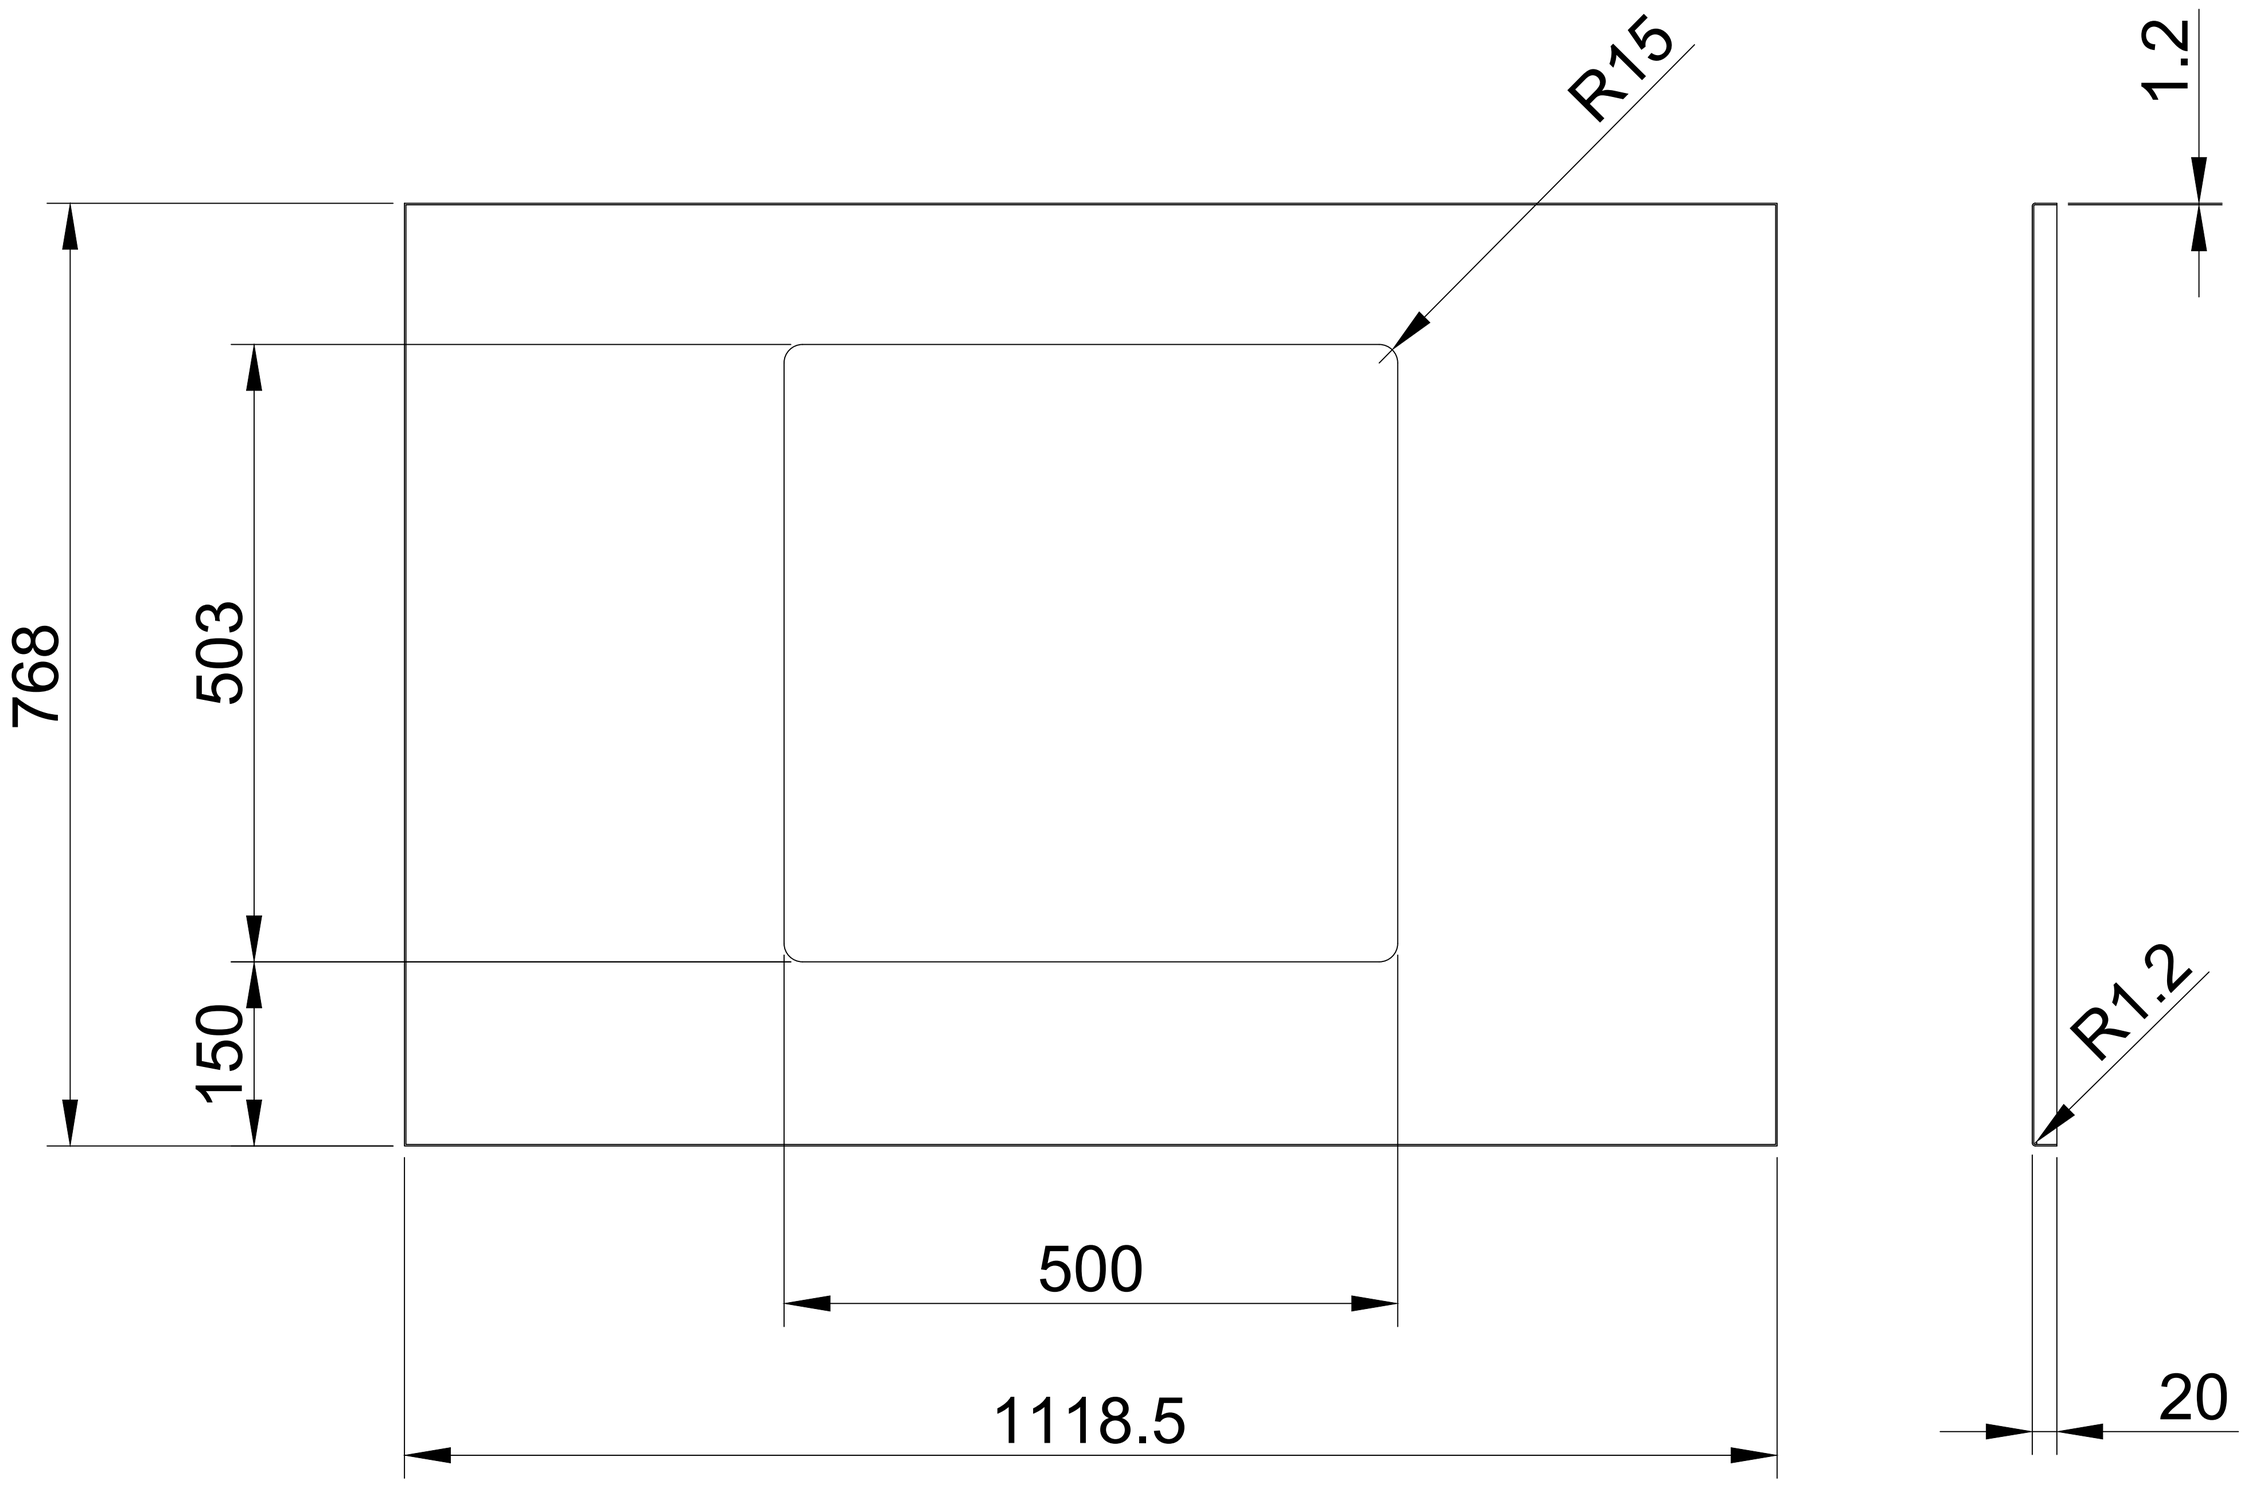


2ND LEAF WINDOW SHEET
MATL - M.S.
QTY - 16 NOS
THK - 1.2 mm

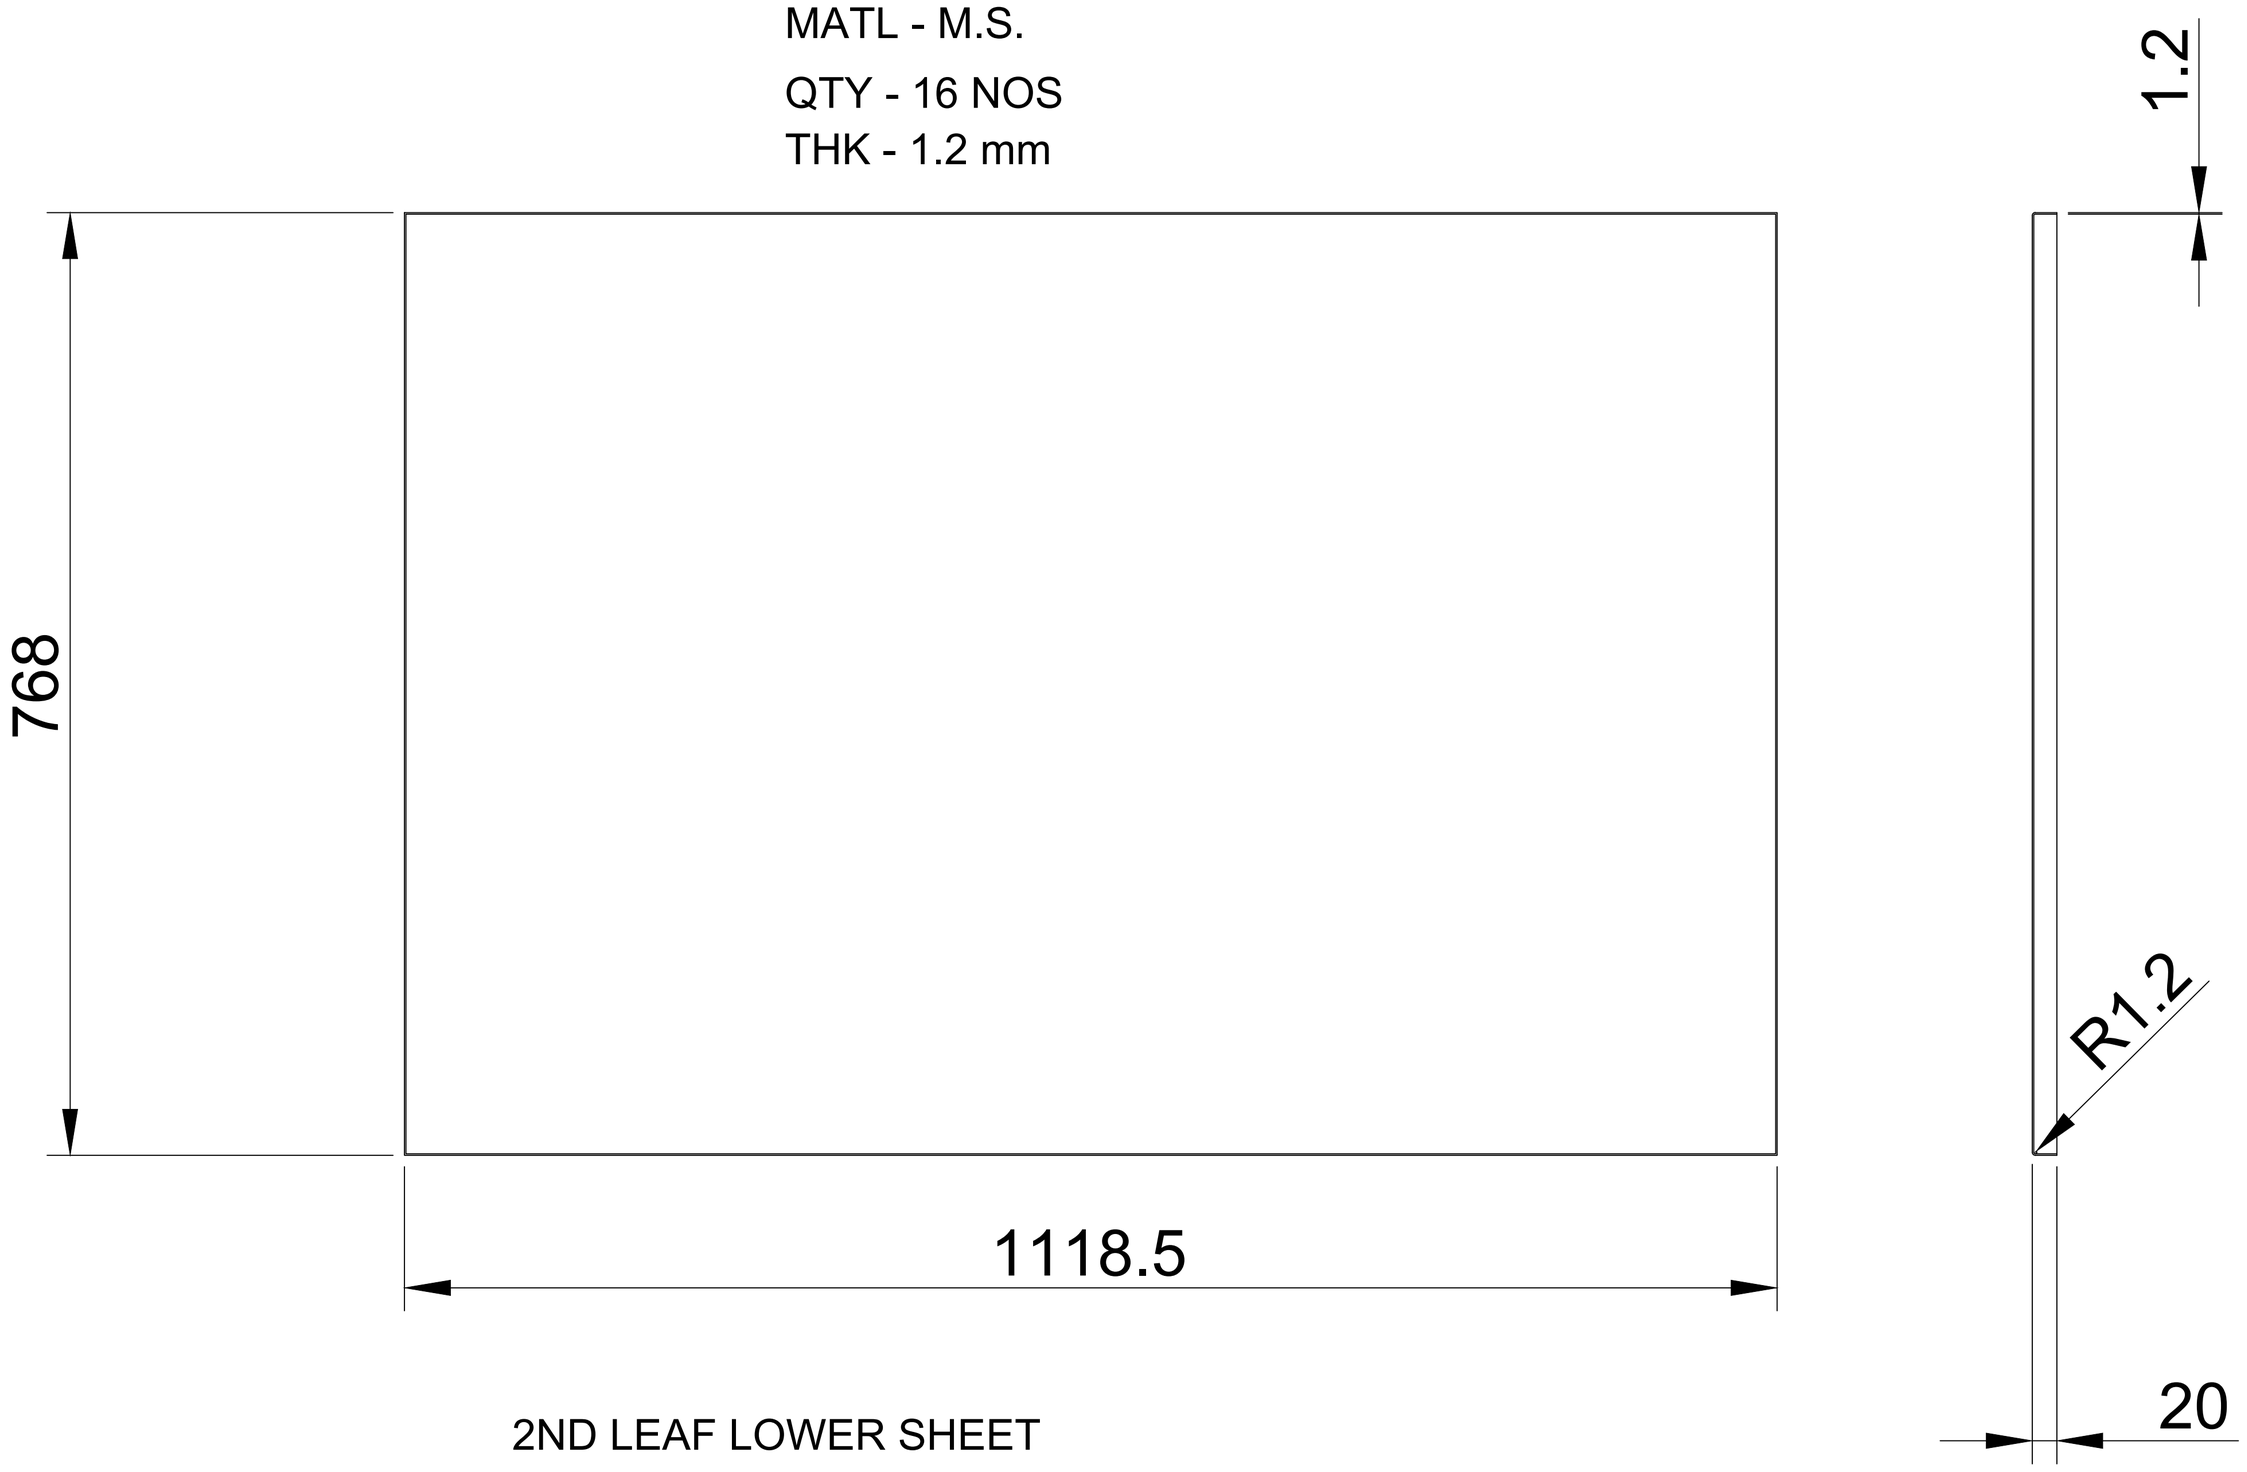

2ND LEAF LOWER SHEET
MATL - M.S.
QTY - 16 NOS
THK - 1.2 mm

Rev No.	Revision	Date	Revised By

This drawing & design is the property of NIHVA TECHNOLOGIES. Not to be sold or copied to any other concern.

TITLE:- 2ND & 3RD LEAF CLADDING

	NAME	DATE	SIGN
DRAWN	NIRMALA	15/04/2023	
CHECK	A.K.	15/04/2023	
APPRD.	V.T.	15/04/2023	

If any queries contact : design@nihva.com

ALL DIMENSION ARE IN mm

NIHVA
NIHVA TECHNOLOGIES PVT. LTD.

NIHVA TECHNOLOGIES PVT. LTD. PUNE
Tel : 020 66304033
Email:- info@nihva.com
Website:- www.nihva.com

CLIENT - Cloos India Welding Technology Pvt. Ltd
LOCATION -
PRODUCT - TELESCOPIC SLIDING GATE | QTY:-
DWG NO:-NIHVA/23-24/VDR/0114 | REV- 0
SCALE: NTS | SCALE:-- 1:1 | SHEET: 01 OF 01