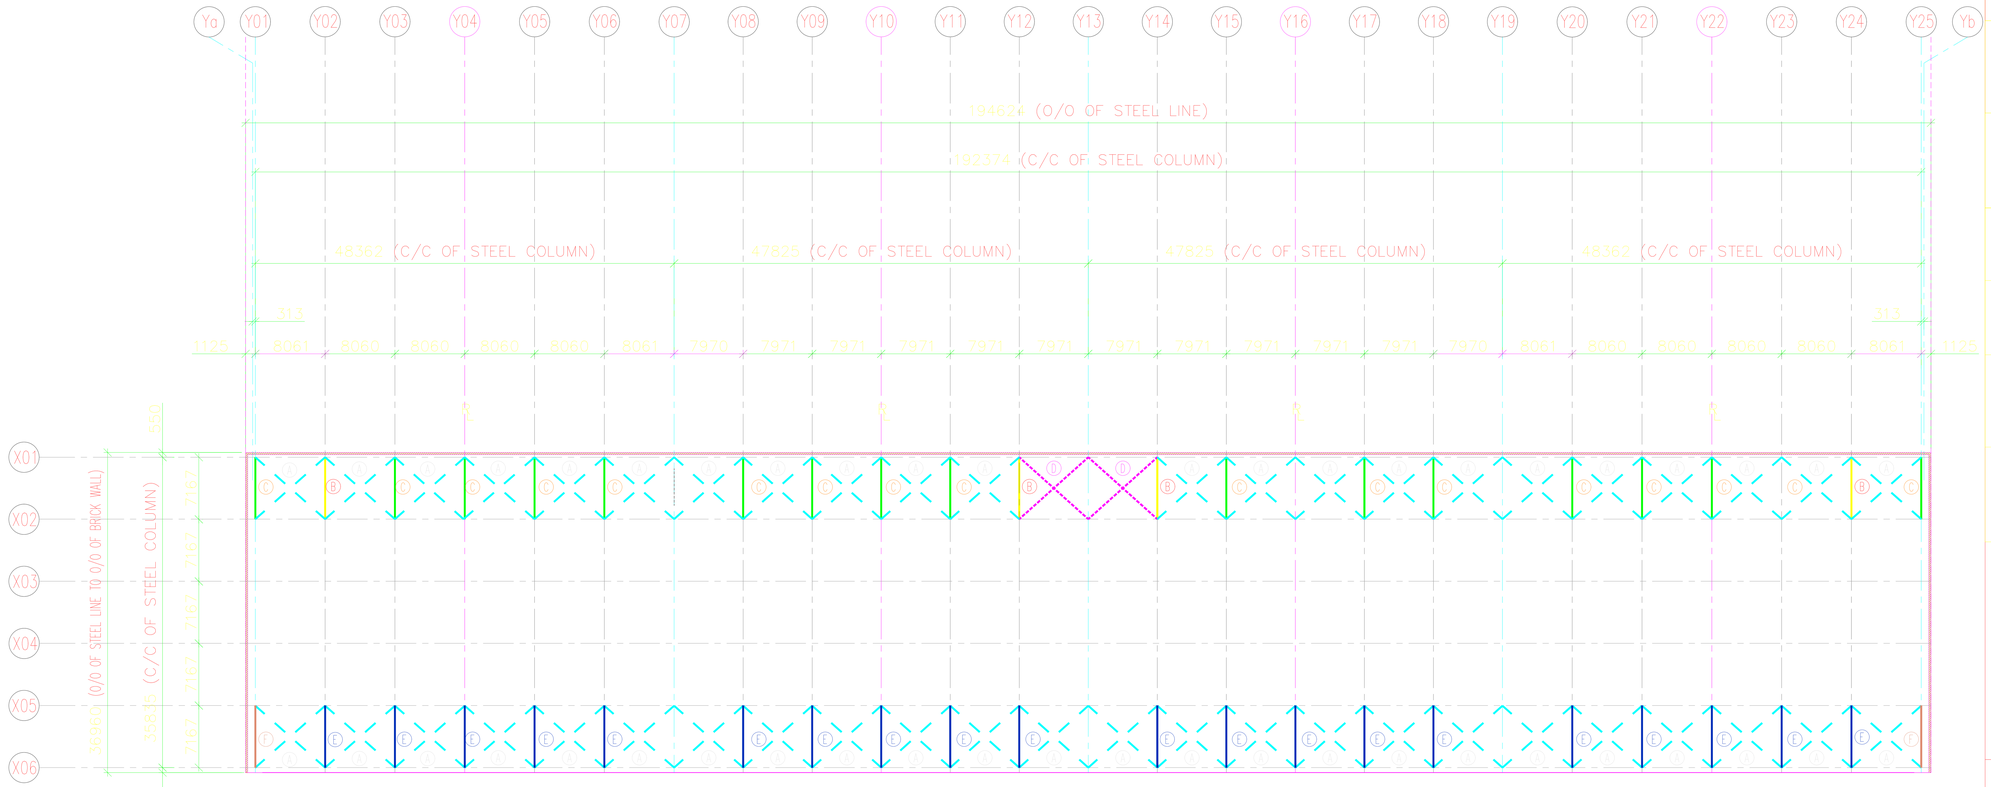


ROOF BRACING PLAN

FOR FASCIA TIE BEAM CONNECTION DETAIL REFER GA-015

MARK NO.	PIPE BRACING DIA. (A)
A	100 NB (M) PIPE
B	175 NB (M) PIPE
C	150 NB (M) PIPE
D	125 NB (M) PIPE
E	W=300x4 F=175x12
F	W=300x4 F=180x12

GOOD FOR RECORDS

ISSUED FOR APPROVAL

SENT ON .....

IN ORDER TO SCHEDULE THIS PROJECT IN THE MOST EFFICIENT MANNER, RETURN THESE DOCUMENTS, MARKED WITH YOUR COMMENTS, WITHIN TWO WEEKS FROM THE ABOVE MENTIONED DATE.

ANY CHANGES MADE AFTER APPROVAL OF THESE DRAWINGS MAY DELAY THE FABRICATION AND DELIVERY PROCESS.

THESE DRAWINGS ARE NOT FOR CONSTRUCTION.

1. ☐ APPROVED
   NO CHANGES, PROCEED WITH FABRICATION.
2. ☐ APPROVED AS NOTED
   FABRICATION MAY PROCEED ON THE BASIS OF CORRECTIONS INDICATED.
3. ☐ NOT APPROVED, RE-SUBMIT FOR APPROVAL.

REVIEWED BY .....
NAME
SIGNATURE DATE

Rev.	Description	Name	Checked	Date
R2	GOOD FOR RECORDS	P.B./B.R.	A.A./M.S.	26/05/2023
R1	ISSUED FOR APPROVAL	P.B.	A.A./M.S.	30/03/2023

REVISIONS

Project: Pre Engineering Building At GMR-DELHI INTERNATIONAL AIRPORT LTD. NEW DELHI

Client: GMR-DELHI INTERNATIONAL AIRPORT LTD. NEW DELHI

Process Consultant:

Detailed Engineering Consultant:


Building: GA PARKING

Drawing Title: ROOF BRACING PLAN


Everest Industries Limited
everest
ESBS Division, Level 3, Tower 14, Solitaire Corporate Park, Chakala, Andheri (E)
Mumbai-400093, India.
Website :- www.everestind.com

Drawn by:	P.B.	Scale:	N.T.S.	Date:	30/03/2023
Checked by:	A.A./M.S.	Project No:	ESBS/PB-02434:01.01.01	Drawing No:	GA-008
Design By	A.A.			Revision:	R2


NOTE:-
1. All rights reserved. This drawing contains proprietary information which is protected by copyright. No part of this drawing may be reproduced, translated in computer language, or transmitted in any form whatsoever without the prior written consent of EVEREST INDUSTRIES LIMITED.

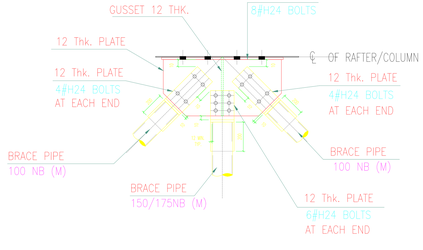

PIPE BRACING DETAIL
(@RAFTER/COLUMN INTERMEDIATE LOCATION)

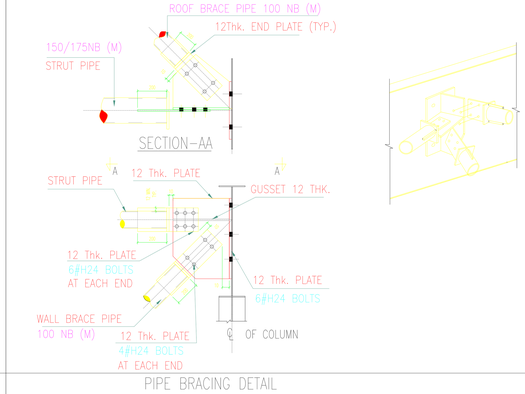

PIPE BRACING DETAIL
(@COLUMN/RAFTER HOUNCH LOCATION)

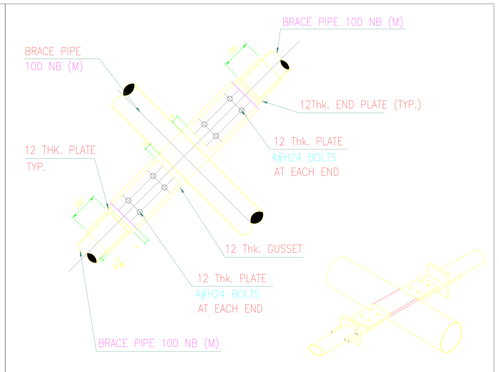

PIPE BRACING DETAIL
(@ INTERSECTION LOCATION)

B-022

SHEET SIZE-A3