


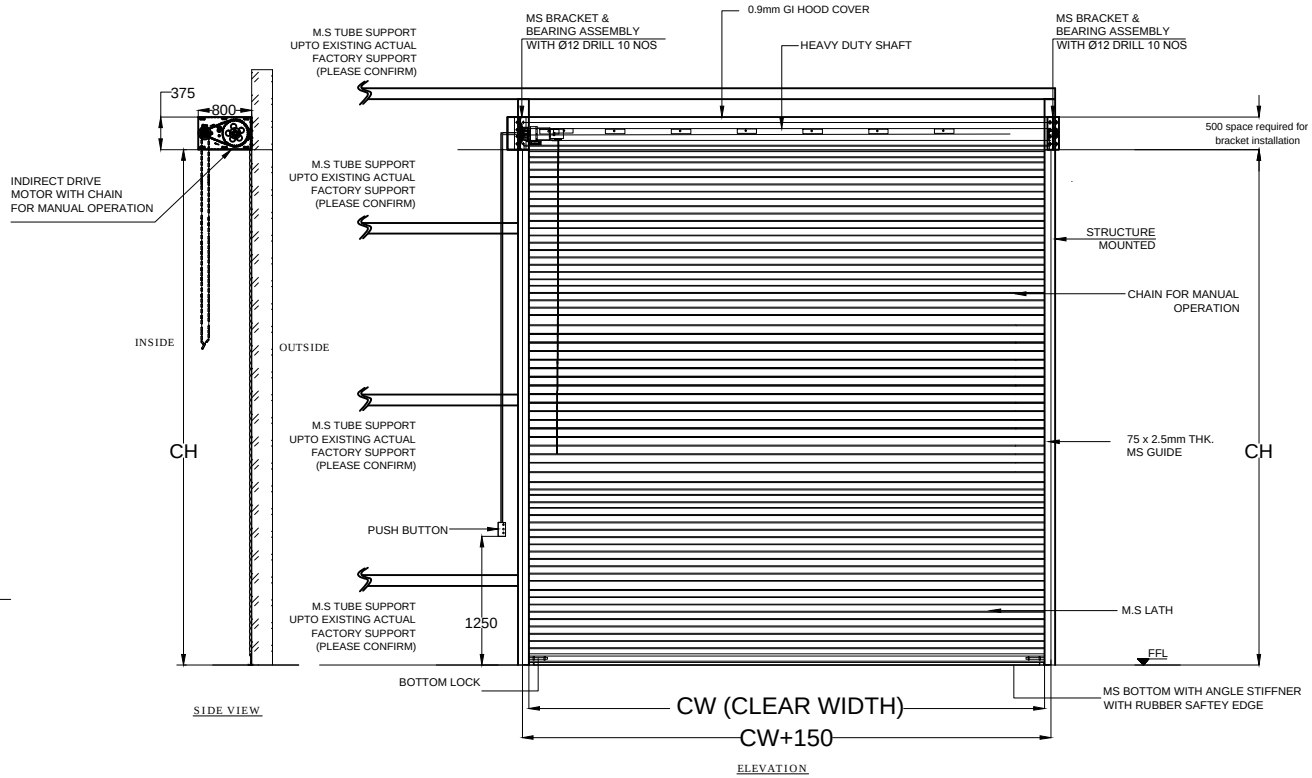


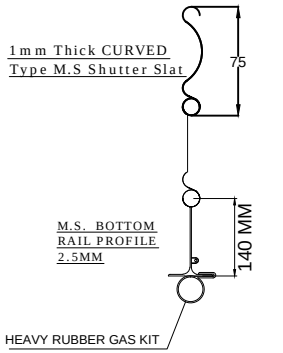

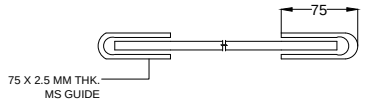

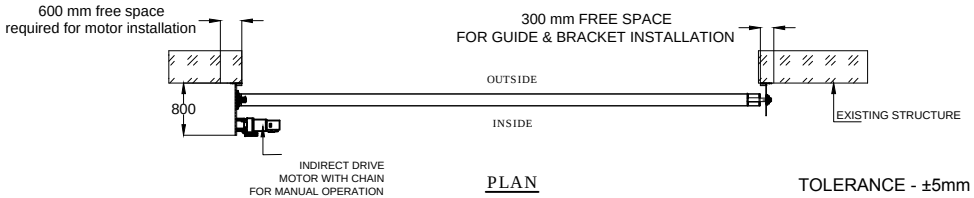

TOLERANCE - ±5mm

REV NO	DATE	DRAWN	REMARK
R02	14.03.20	P.A	3. CLIENT DETAILS CHANGE 2. RAL CODE CHANGE. 1. MOTOR LOCATION CHANGE
R01	13.03.20	P.A	1. STRUCTURE DESIGN CHANGE

This drawing & design is the property of NIHVA TECHNOLOGIES. Not to be sold or copied to any other concern.

NOTE-
1. ALL CIVIL WORK & M.S STRUCTURE WILL BE CLIENT'S SCOPE.

S.NO	RAL CODE	COLOR	CLEAR WIDTH	CLEAR HEIGHT	QTY.	MOUNTING
01	RAL 5002	UM BLUE	2500mm	2500mm	1 NO	STRUCTURE

TITLE
MOTORISED ROLLING SHUTTER

	NAME	SIGN	DATE
DRAWN	P.A		12.02.2020
CHECK	G.J		12.02.2020
APPRD.			

If any queries contact : design@nihva.com

ALL DIMENSION ARE IN mm

NIHVA TECHNOLOGIES PVT. LTD.
Website:- www.nihva.com

NIHVA TECHNOLOGIES
PVT. LTD. PUNE
Tel : 020 66304033
Email:- info@nihva.com

CLIENT - MASTPRO
PROJECT - MARS
SITE LOCATION - KHED CITY
DWG. NO. : NIHVA/19-20/0213/R02
REV- R02
SCALE: NTS
WT:
SHEET: 01 OF 01