
PRODUCED BY AN AUTODESK EDUCATIONAL PRODUCT

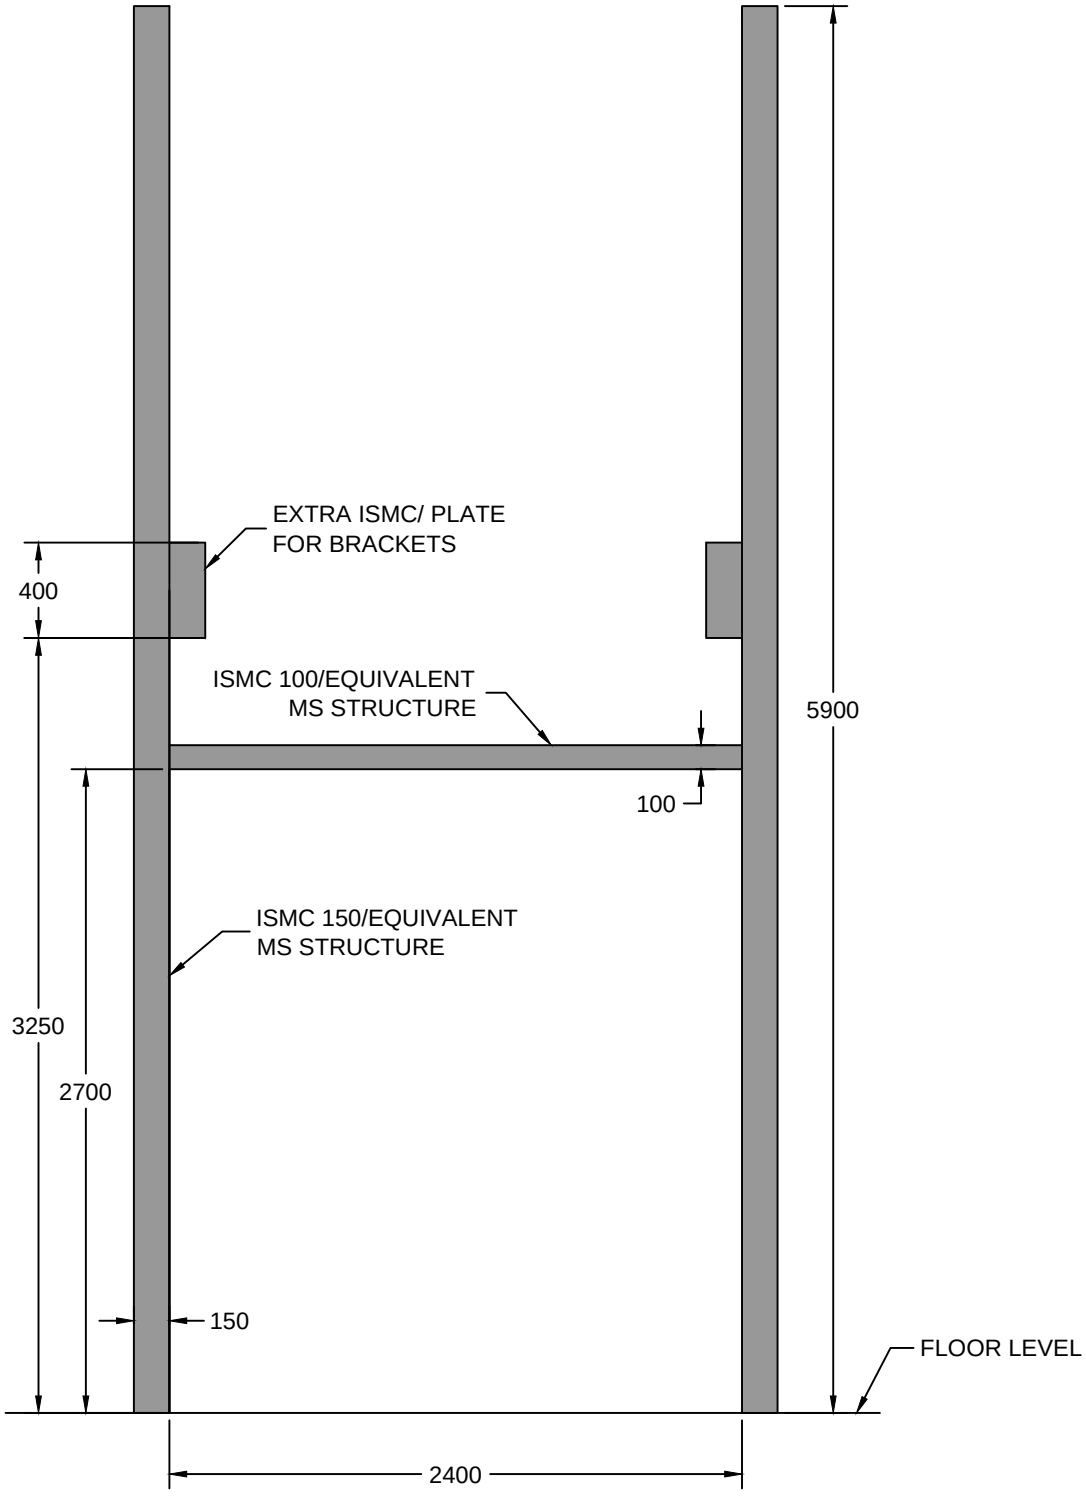

MS STRUCTURE

This drawing & design is the property of NIHVA TECHNOLOGIES. Not to be sold or copied to any other concern.

TITLE

STRUCTURE FOR SECTIONAL DOOR

CLIENT APPROVAL

ALL DIMENSION ARE IN mm

NIHVA TECHNOLOGIES PVT. LTD.

NIHVA TECHNOLOGIES PVT. LTD. PUNE
Tel : 020 66304033
Email:- info@nihva.com
Website:- www.nihva.com

	SIGN	DATE
DRAWN	OMKAR	31/08/17
CHECK	SHEKHAR	31/08/17
REV.		
APPRD.	SHEKHAR	31/08/17
MFG		
Ref No.		

CLIENT - RELIANCE

PROJECT -

SITE - SULTANPUR

DWG. NO. - NIHVA/17-18/0192

SCALE: NTS | WT: | SHEET: 01 OF 01

If any queries contact : projects@nihva.com

PRODUCED BY AN AUTODESK EDUCATIONAL PRODUCT

PRODUCED BY AN AUTODESK EDUCATIONAL PRODUCT