



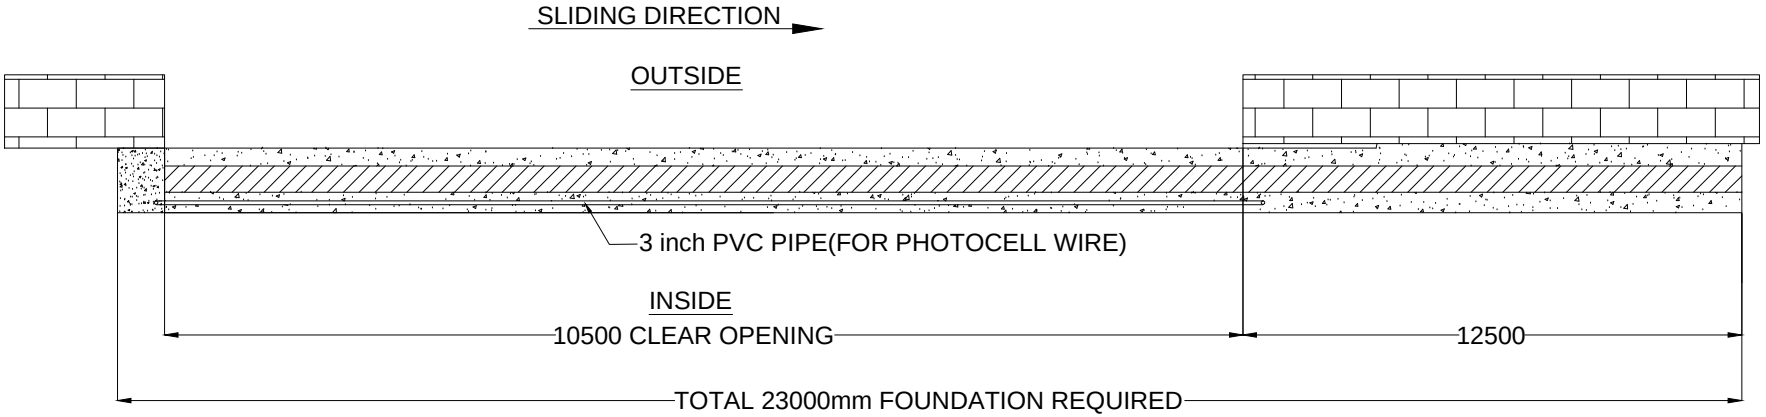

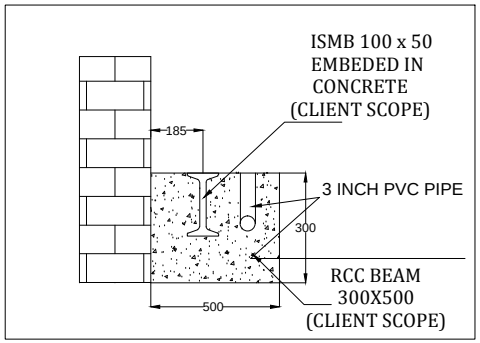

This drawing & designing is the property of NIHVA TECHNOLOGIES. Not to be sold or copied to any other concern.

TITLE			
SLIDING GATE FOUNDATION DRAWING			
	Name	SIGN	DATE
DRAWN	SURAJ		13/11/18
CHECK	PRADEEP		13/11/18
APPROVAL	R.D		13/11/18

If any queries contact : design@nihva.com

ALL DIMENSION ARE IN mm

NIHVA
NIHVA TECHNOLOGIES PVT. LTD.
NIHVA TECHNOLOGIES PVT. LTD. PUNE
Tel : 020 66304033
Website:- www.nihva.com
Email:- info@nihva.com

CLIENT -INOX AIR PRODUCTS

PROJECT -

SITE LOCATION -MODINAGR,UTTAR PRADESH

DWG. NO. : NIHVA/18-19/0176/R01 REV.:- R01

SCALE: NTS WT: SHEET: 01 OF 01

REV NO	REV DATE	DRAWN	REMARK
R01	10.10.2019	P.V.A	1. CLEAR WIDTH CHANGE