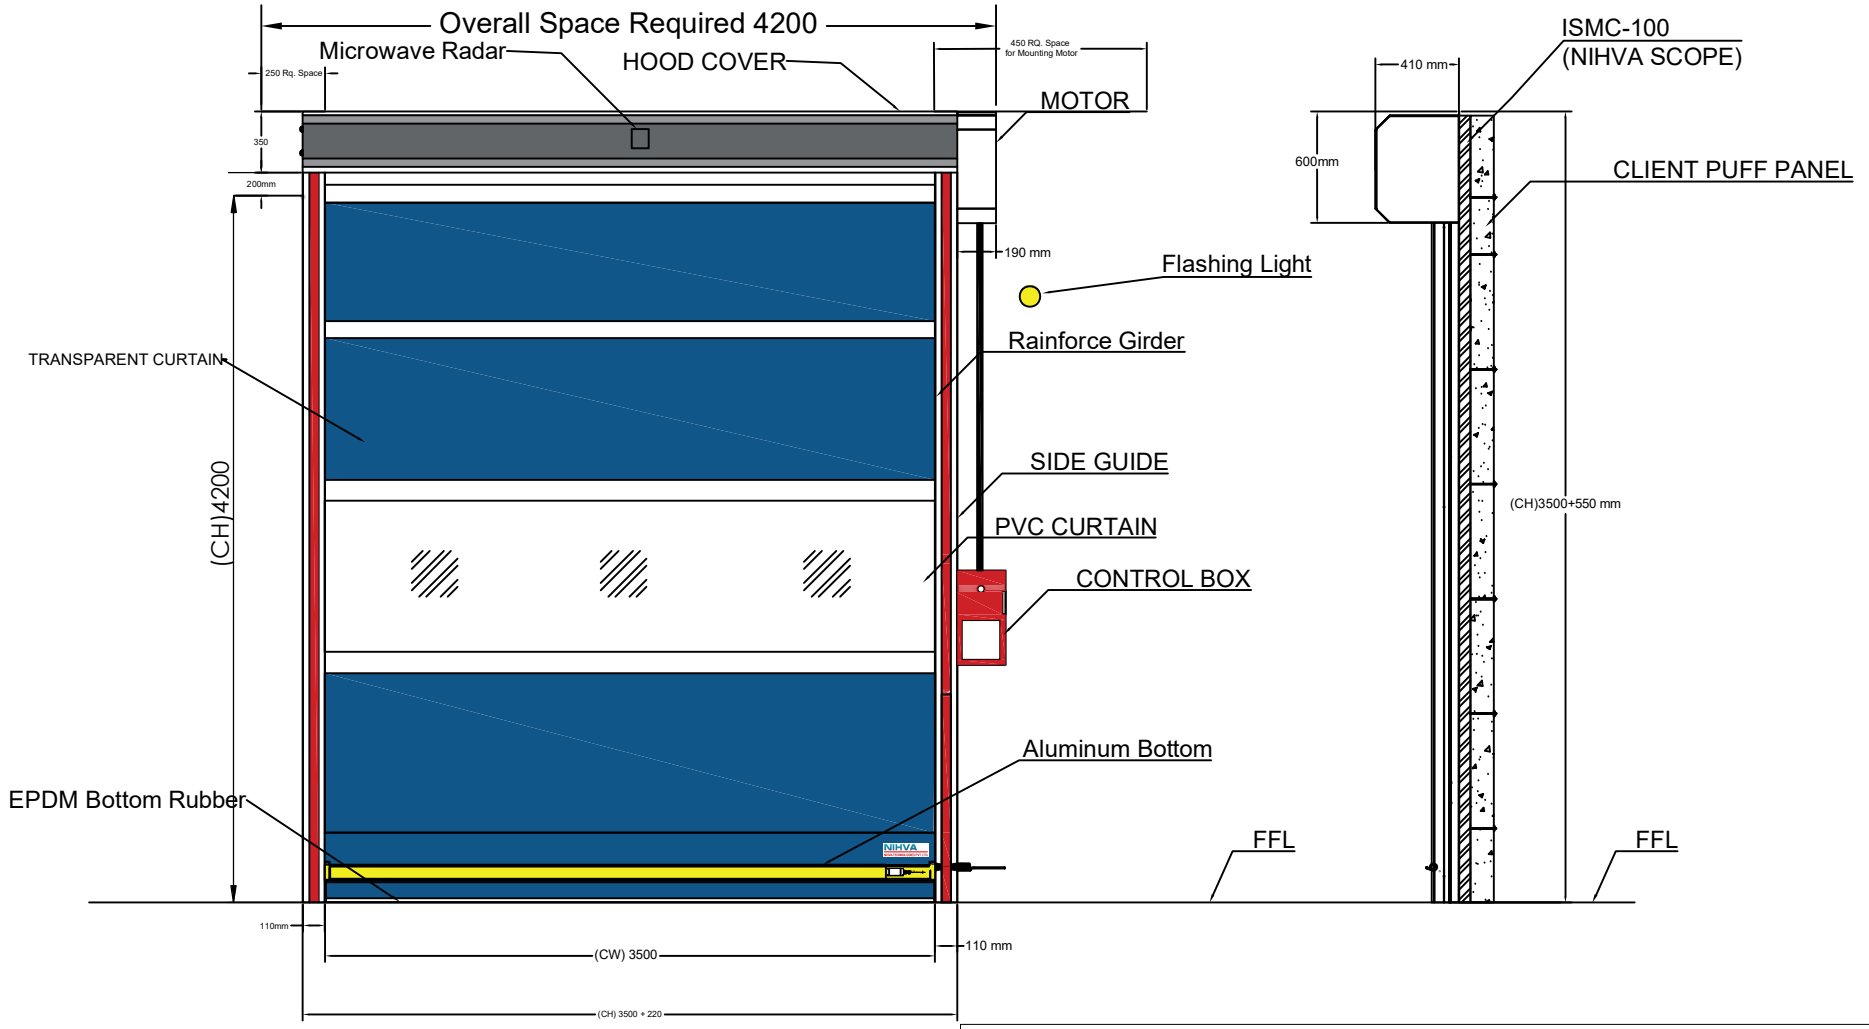


NOTE: (1) REQUIRED M.S. TECHNICAL STRUCTURE & FITTING FOR HSD IS IN NIHVA SCOPE)

(2) ALL CIVIL WORK IN CLIENT SCOPE

Sr	Description	Clear Width (CW)	Clear Height (CH)	QTY
1	HSD With Sensor	**3500**	**4200**	1

This drawing & design is the property of NIHVA TECHNOLOGIES. Not to be sold or copied to any other concern.

TITLE HIGH SPEED DOOR GA DRAWING

	NAME	SIGN	DATE
DRAWN	S.J		18.01.2024
CHECK	A.K		18.01.2024
APPRD.	V.T		18.01.2024

If any queries contact : projectsupport@nihva.com

ALL DIMENSION ARE IN mm

NIHVA TECHNOLOGIES PVT. LTD.

NIHVA TECHNOLOGIES PVT. LTD. PUNE
Tel : 020 66304033
Email:- info@nihva.com
Website:- www.nihva.com


CLIENT - RINAC

PROJECT - HIGH SPEED DOOR

FORMAT NO - NIHVA-DD-F-03

DWG. NO. : NIHVA/23-24/00XX | REV- R00

SCALE: NTS | WT: | SHEET:

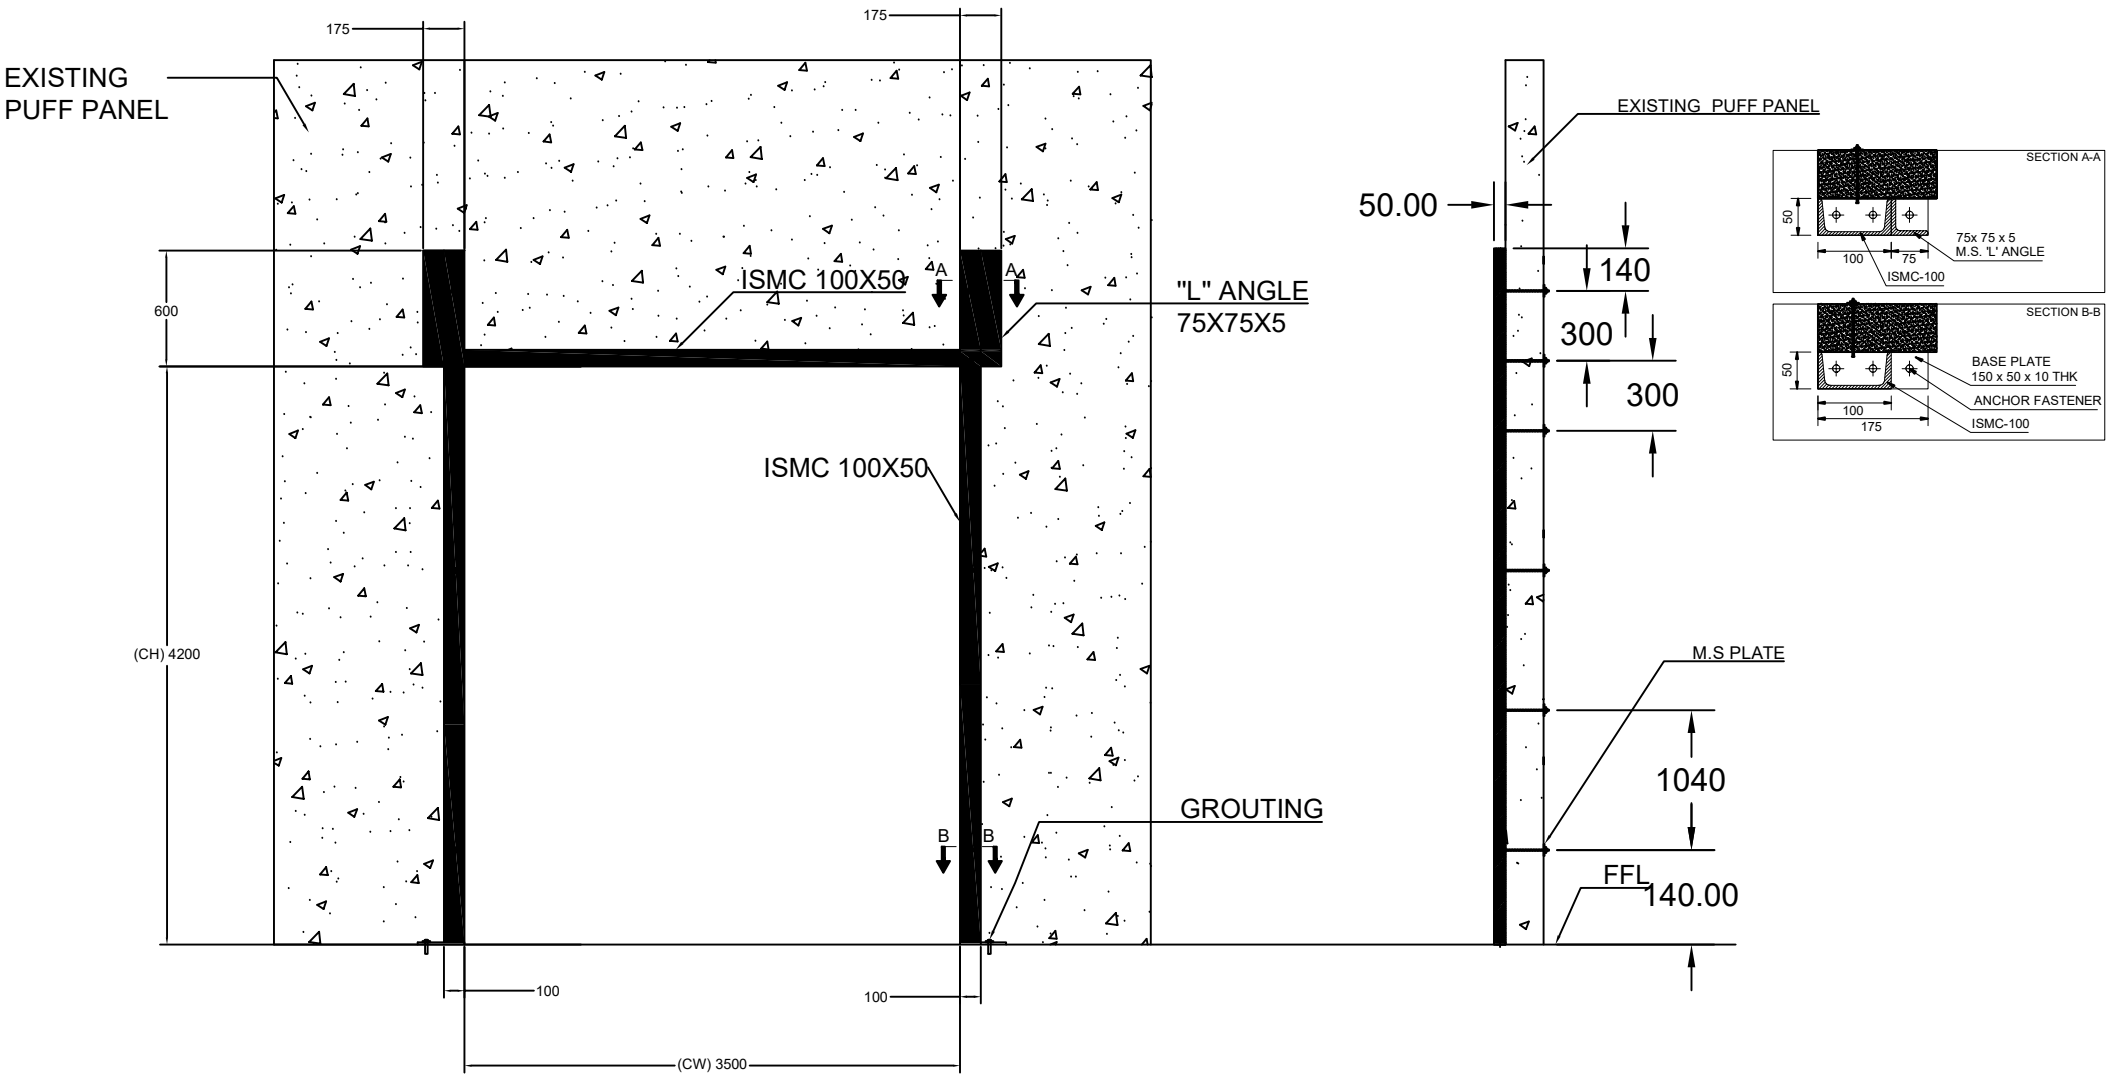

M.S. STRUCTURE DETAILS

Sr	Description	Clear Width (CW)	Clear Height (CH)	QTY
1	HSD With Sensor	**3500**	**4200**	1

This drawing & design is the property of NIHVA TECHNOLOGIES. Not to be sold or copied to any other concern.

TITLE HIGH SPEED DOOR STRUCTURE DRAWING

NIHVA TECHNOLOGIES PVT. LTD.

NIHVA TECHNOLOGIES PVT. LTD. PUNE
Tel : 020 66304033
Email:- info@nihva.com
Website:- www.nihva.com

	NAME	SIGN	DATE
DRAWN	S.J		18.01.2024
CHECK	A.K		18.01.2024
APPRD.	V.T		18.01.2024

If any queries contact : projectsupport@nihva.com

ALL DIMENSION ARE IN mm

CLIENT - RINAC

PROJECT - HIGH SPEED DOOR ST.

FORMAT NO - NIHVA-DD-F-03

DWG. NO. : NIHVA/23-24/00XX | REV- R00

SCALE: NTS | WT: | SHEET: