

LOAD DIAGRAM

Nominal static vertical loads are indicated. Value within brackets include dynamic surload factor 1.25 for door leaf loads in open position.
Includes items provided by ASSA ABLOY only.

DISTRIBUTED LOAD: 37.5kN

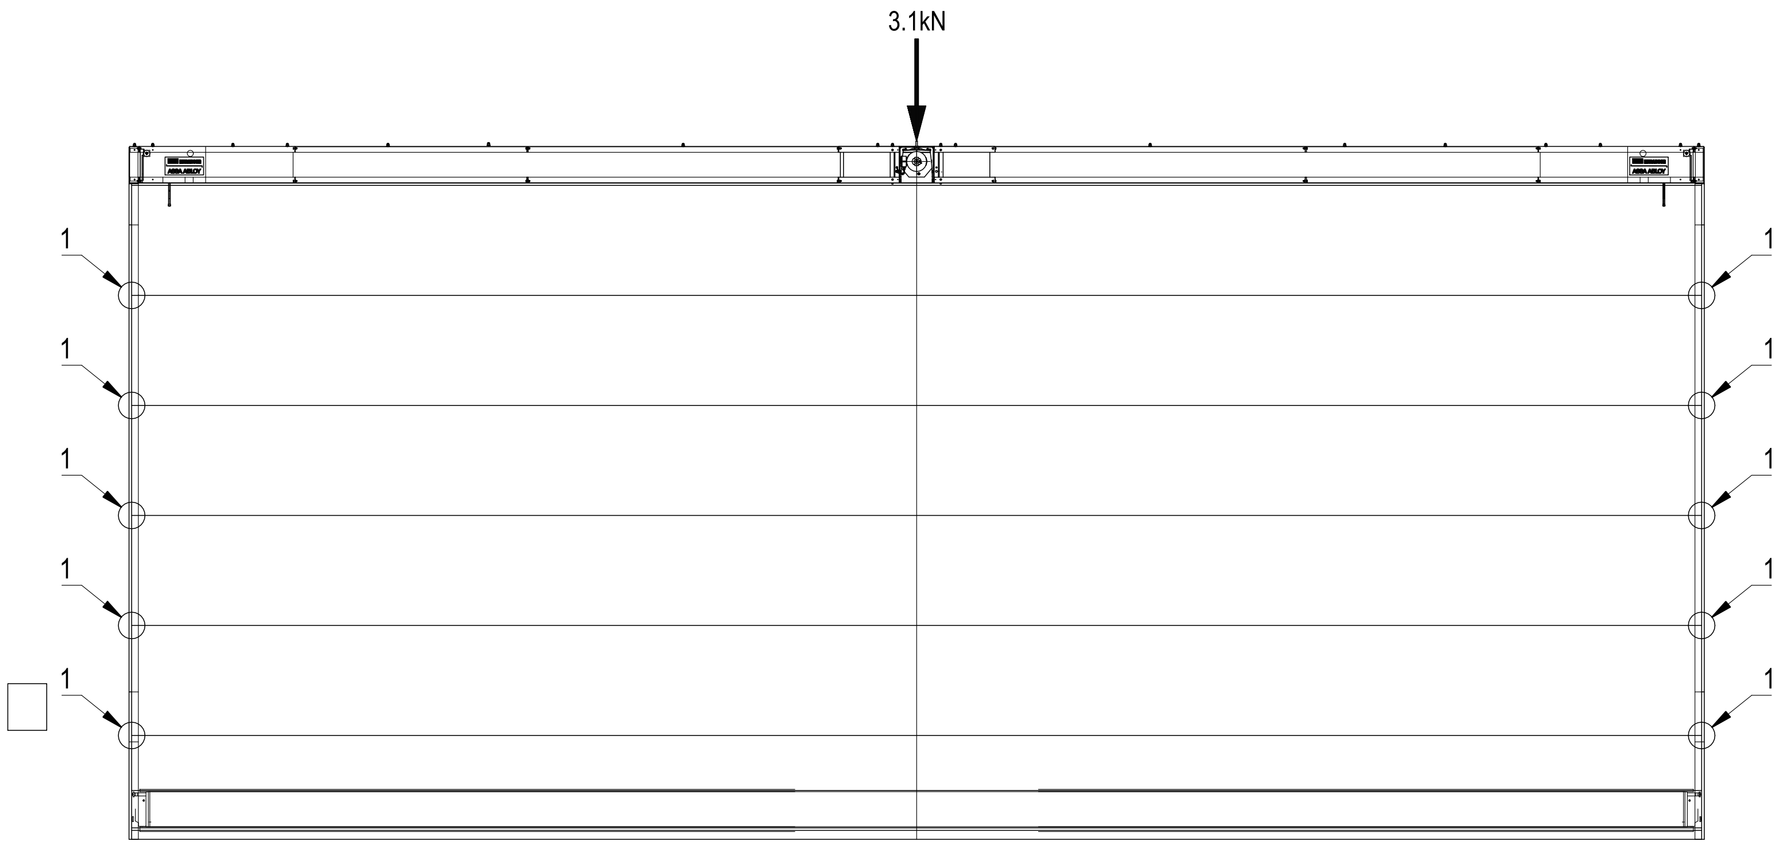

Interior view, Door closed

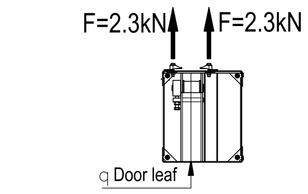


Load on header box attachment (each screw), due to wind load and door weight

DISTRIBUTED LOAD: 8.7kN


14.4kN (18.0kN)

3.1kN


14.4kN (18.0kN)

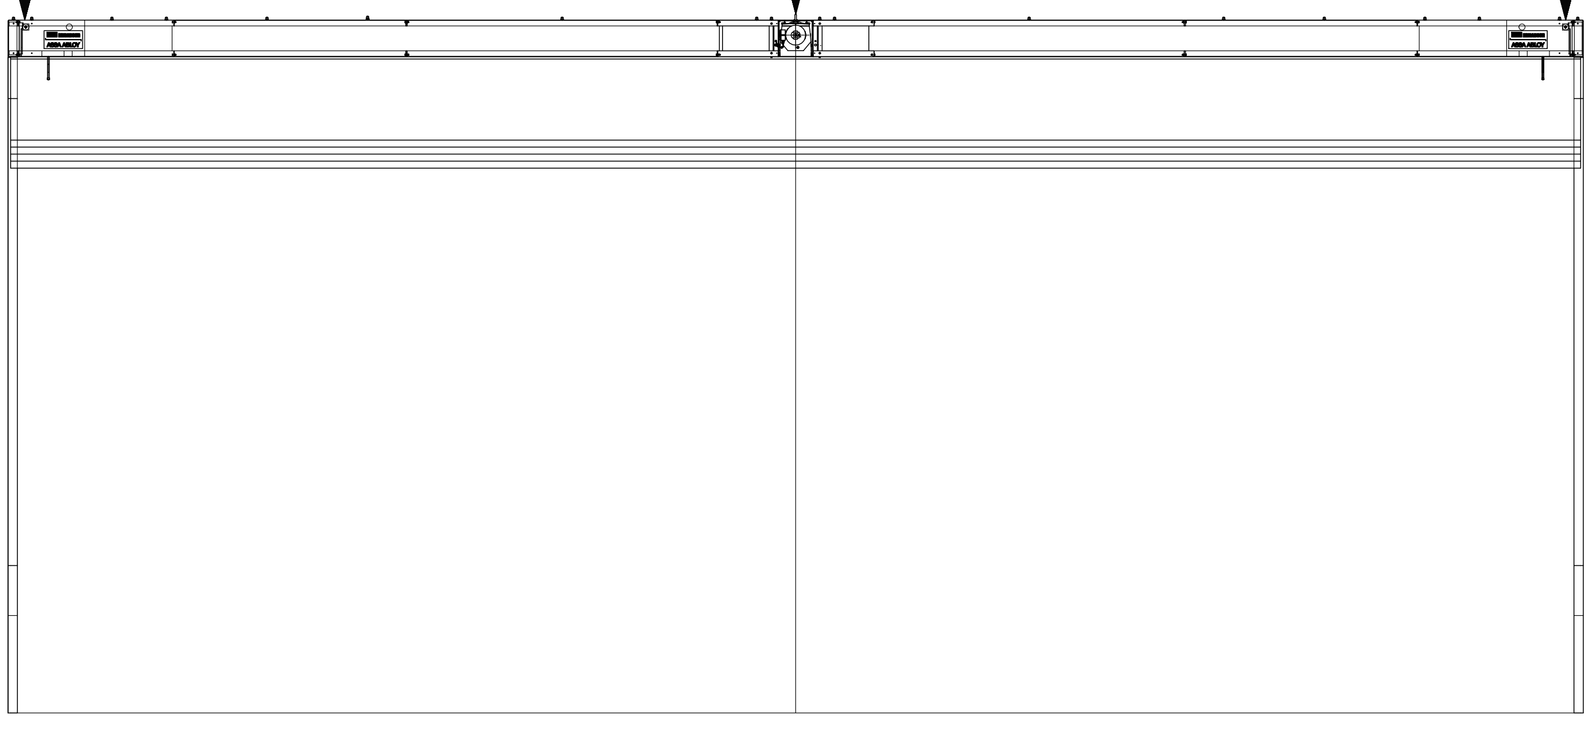

Interior view, Door open

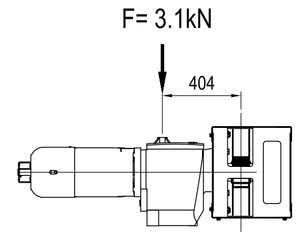

Section @ gear motor
SK 73F-132 S/4
Scale 1:20

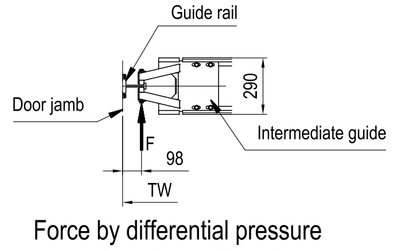

Force by differential pressure transferred to guide rail at each intermediate position.
(located at pos 1)
F=13.4 kN

NOT INCLUDED IN DOOR SUPPLY:

1. Design and supply of all door supporting structural components.
2. Design and supply of all closure between door and adjacent steel.
3. Design and supply of coverage, such as roofing or enclosure, for door components at door head.
4. Door jambs adjustable for overall door width and true to plumb.
5. Paint job after completed door installation.
6. Any frameworks being provided by ASSA ABLOY will be clearly indicated as "by ASSA ABLOY".

REQUIREMENTS ON BUILDING:

7. Door head support must be straight within 1/600 of span in the in/out direction and free from protrusions of any kind.
8. For a single door leaf, door head support should be horizontal and straight within 1/600 of span at distributed full door load.
9. Door side jambs must be smooth, straight and parallel, out of plumb must not exceed 2mm/m (total deviation at full length 5 mm) in any direction.
10. Any footings at bottom of jamb columns must not interfere with installation of guide rails at floor level.
11. At time of installation, finished floor, free from obstructions, out to a distance of 2 m on each side of door centreline must be available.
12. Header box must be accessible from both sides during installation.

DOOR PROPERTIES:

13. The door is designed to withstand a differential pressure of 1kPa.
14. Guide rails, top- and intermediate beams in extruded aluminium with natural finish.
15. Environmental category: Megadoor standard
16. Bottom beam in carbon steel painted: Light grey (RAL7047)
17. Colored clamp strips on both sides: GREY (RAL7004)
18. Door header box enclosed on motor side.
19. Color of header box: BLACK (NCS 9000-N. RAL 9005)
20. The door fabric is a UV stabilized, flame retardant, self-extinguishing, PVC coated polyester fabric with fire technical properties Euroclass C-s2, d0 (according to EN 13501-1:2007).
    Colour of fabric: White Aluminum (RAL 9006)

ELECTRICAL:

21. One main control panel provided of PLC type.
22. Control mode : Impulse up / Constant contact down.
23. Cables are included.
24. Back-up power socket & switch.
25. Audible & visual alarm.
26. Approx. size of main control panel: WxHxD (500x600x250mm),
27. Location of main control panel: Please specify location.
28. Aux. Voltage 24VDC
29. Power supply: 400V /3Ph /50Hz
30. Power: 8.6kW
31. Nom. current: 18.1A
32. Start current: 79.6A
33. (max. allowed voltage drop at start: 5%)

BELT HOIST UNITS:

SK 73F-132S74 OD440
75mm wide polyester belt. Rupture load 108kN/belt.

DOOR IDENTITY NUMBER: 84470001

INTERFACE DRAWING, ref. to drwng. no. 69424

DESIGNED FV	APPROVED	SIZE A1	SCALE 1:50
CODE 84470		If not otherwise stated: Tolerances ISO 2768-m EN ISO 13920-B	
ITEM NO		Cutting class ISO 9013-442	
DATE 2019-10-08		Weld class ISO 5817-C	
ASSA ABLOY		Surface finish Smooth raw surface	

Nihva Poonawalla
India
Megadoor 20000 x 7000
Load diagram & Notes

DRAWING NO 69425 | REVISION --

PLOT DATE

This document is the property of ASSA ABLOY Entrance Systems AB and shall not without our written permission be copied, imparted to a third party or used for any other unauthorized purpose.