

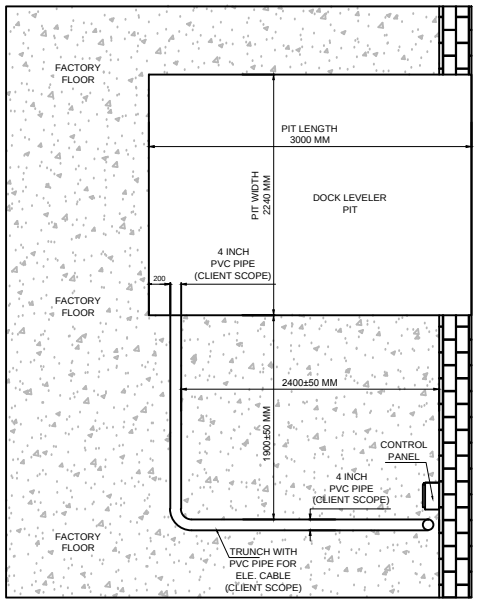


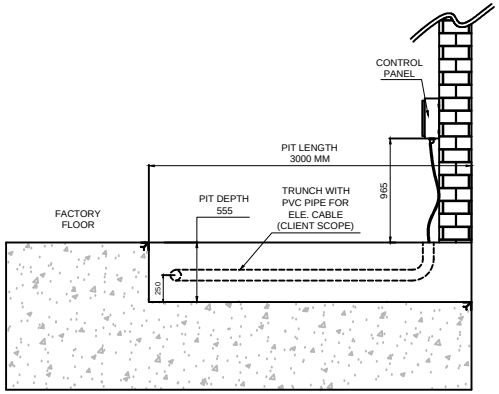

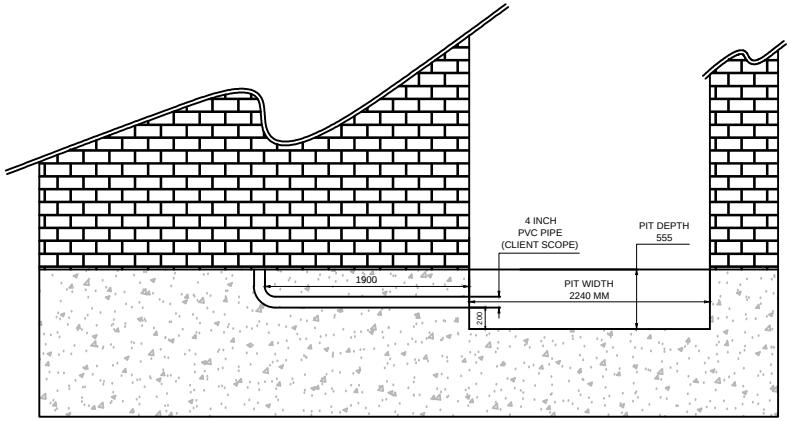

TOLERANCE :- ± 10mm

CONSULTANT NAME : SPECTRUM PHARMATECH CONSULTANT PVT LTD.

This drawing & design is the property of NIHVA TECHNOLOGIES. Not to be sold or copied to any other concern.

TITLE

DOCK LEVELER PIT

NIHVA TECHNOLOGIES PVT. LTD. PUNE
Tel : 020 66304033
Email:- info@nihva.com
NIHVA TECHNOLOGIES PVT. LTD.
Website:- www.nihva.com

	NAME	SIGN	DATE
DRAWN	P.V.A		22.06.2019
CHECK	V.M.T		22.06.2019
APPRD.			

CLIENT - MYLAN LABORATORIES LTD

PROJECT - CENTRAL WAREHOUSE

SITE LOCATION - BANGLORE

If any queries contact : design@nihva.com

DWG. NO. : NIHVA/19-20/0037 | REV- 00

ALL DIMENSION ARE IN mm | SCALE: NTS | WT: | SHEET: 01 OF 01