

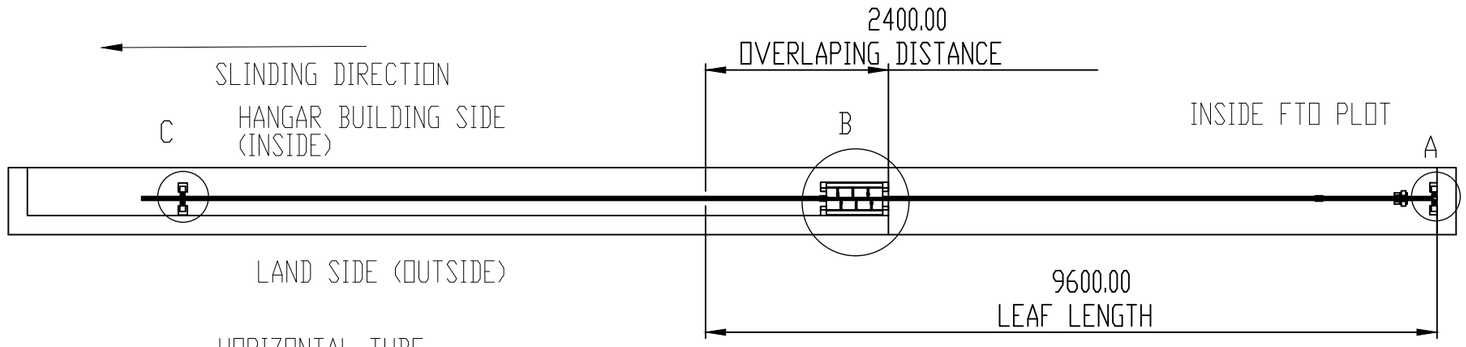


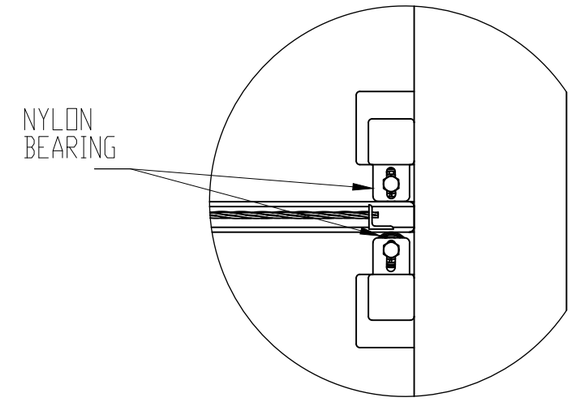



POST 1 AND NYLON
BEARING ASM

DETAIL A
SCALE 1 : 10

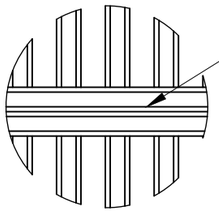


DETAIL E
SCALE 1 : 10

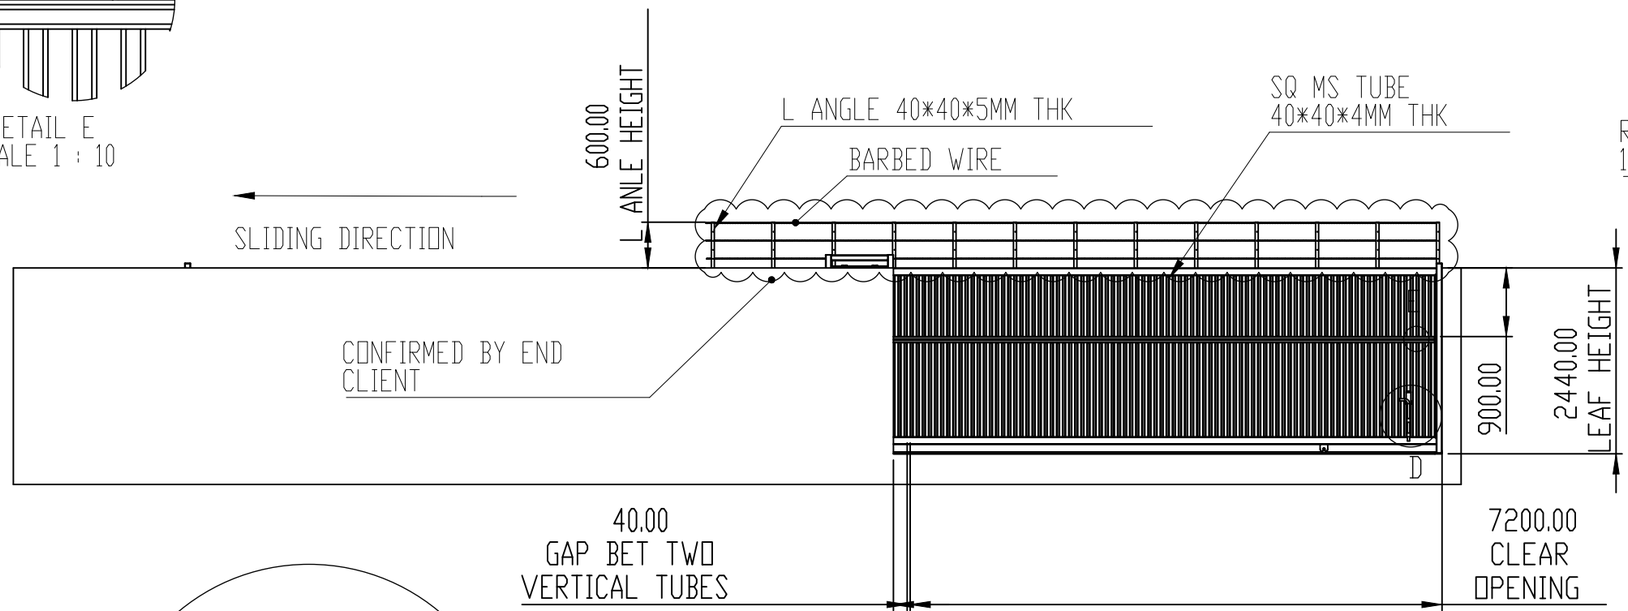

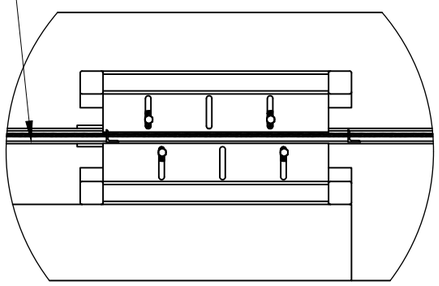


POST 2 AND NYLON
BEARING ASM

DETAIL B
SCALE 1 : 20

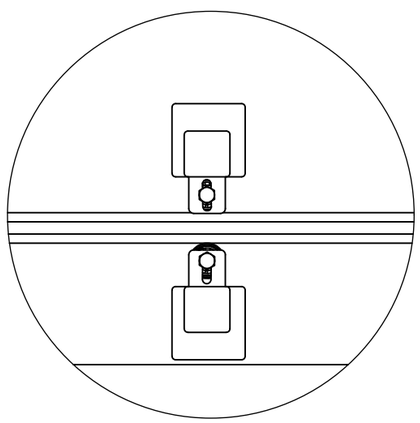

POST NO 3 &
NYLON ROLLER BERAING
ASM

DETAIL C
SCALE 1 : 10

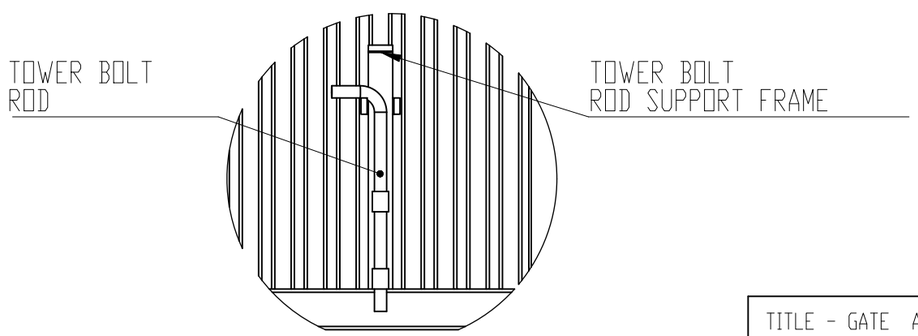

TOWER BOLT LOCKING
ARRANGEMENT.

DETAIL D
SCALE 1 : 15

NOTE :
GA DRAWING
TYPE NO 01

TITLE - GATE AUTOMATION				NIHVA TECHNOLOGIES PVT.LTD.PUNE
DWG NO - NTPL-000-PM-001-00-00-00				Website - www.nihva.com
	NAME	SIGNATURE	DATE	PROJECT NO - NTPL-000-PM
DRAWN	V.W		21-05-2025	PRODUCT - SINGLE SLIDING GATE
CHK'D	S.W.		21-05-2025	SITE LOCATION -
APPV'D	V.T.		21-05-2025	
if any queries contact - supportautomation@nihva.com				REVISION - 01 / QTY - 1
ALL DIMENSION ARE IN mm			A3	SCALE / SHEET 1 OF 1