
DRAWING

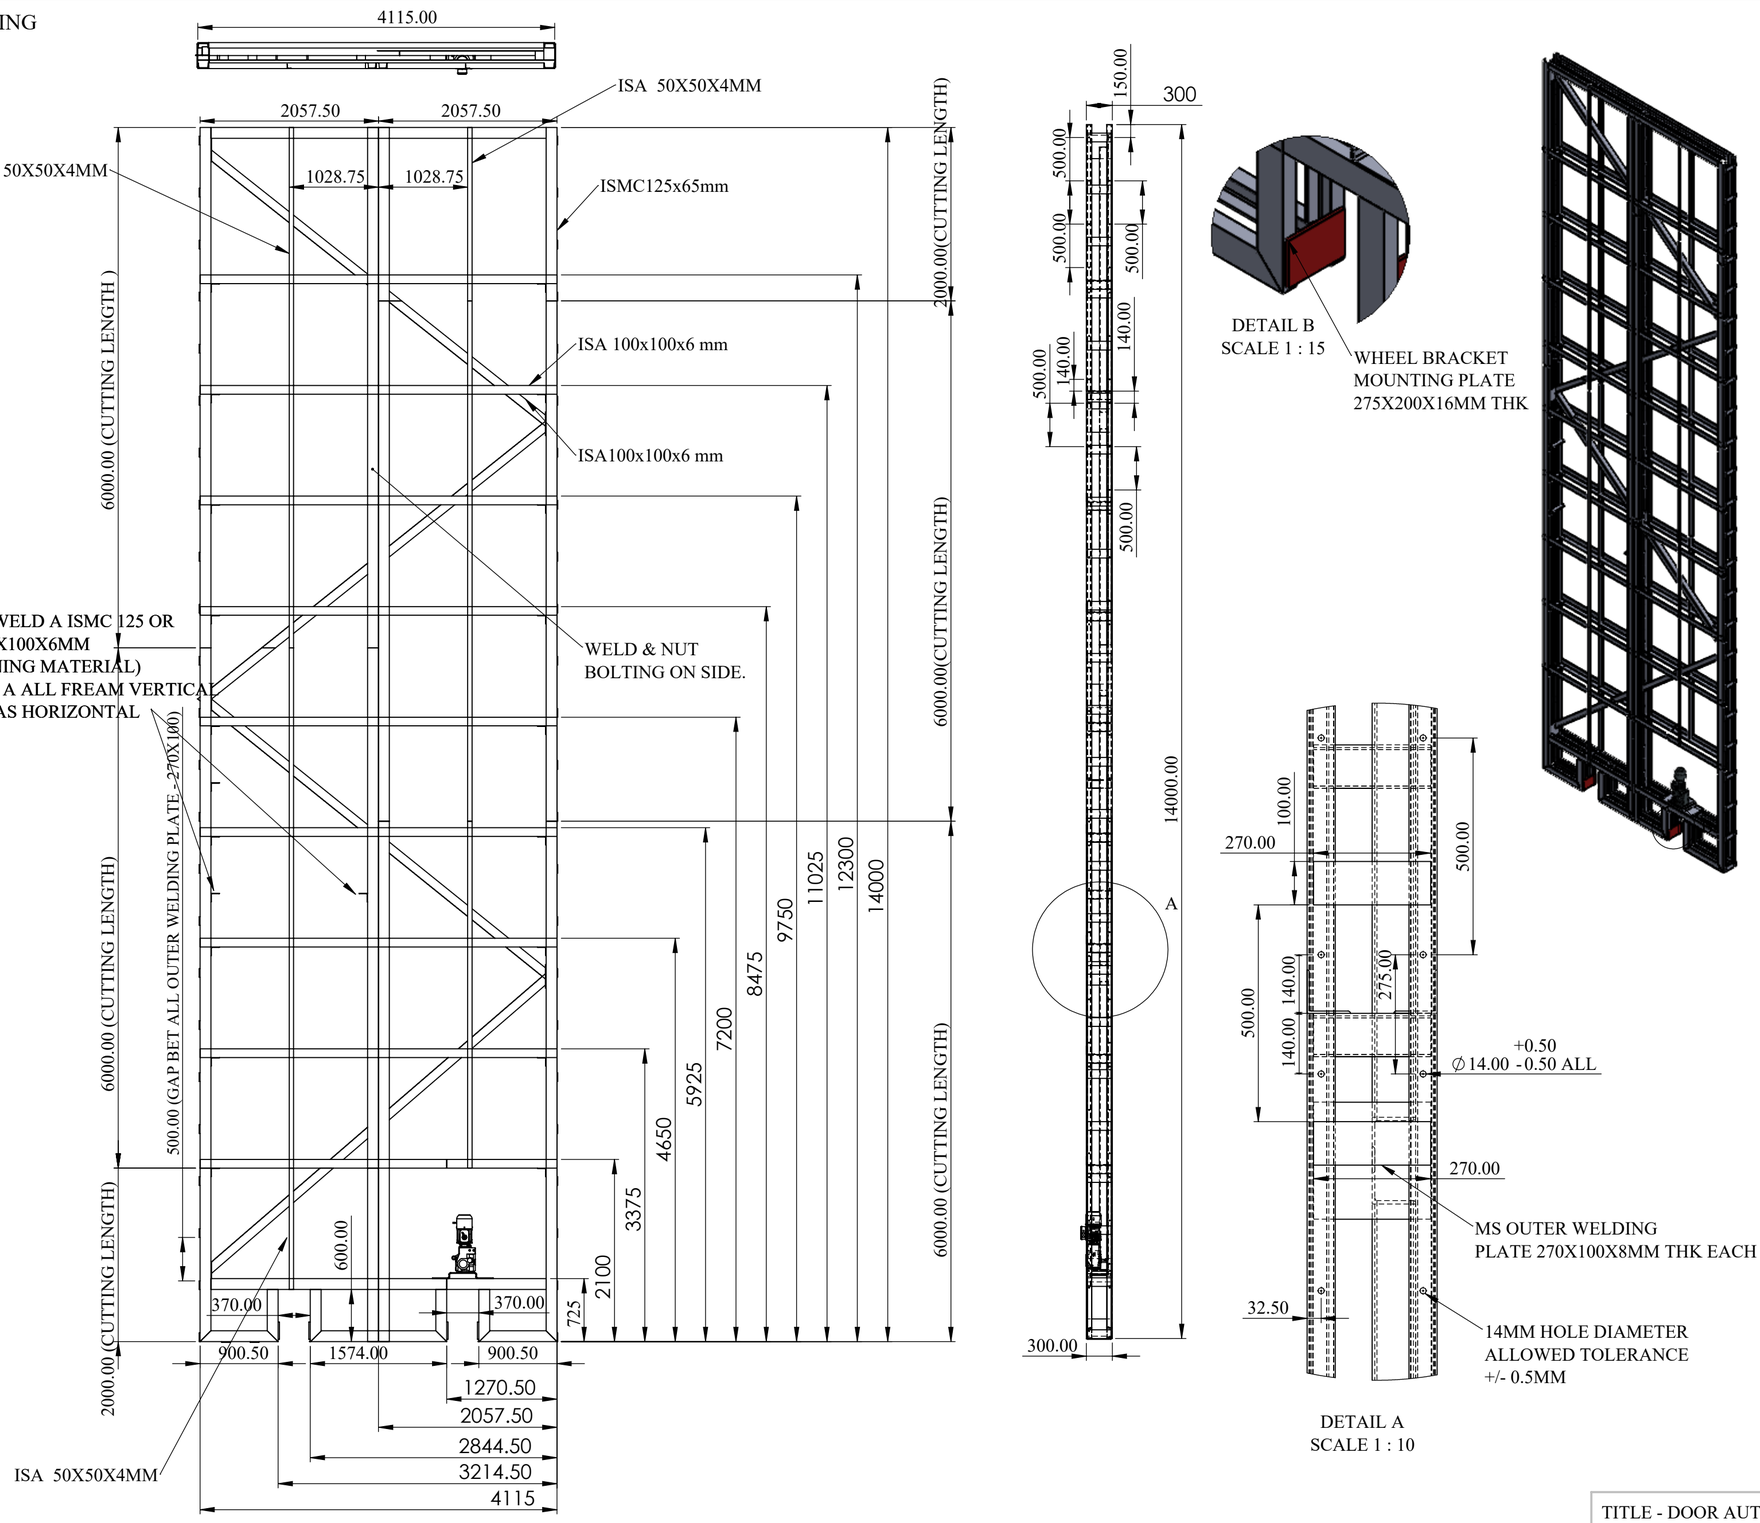

REV DESCRIPTION	DATE	REV NO
	08-08-2025	REV 00
1.		


NOTE :


NAME: HANGER SLINDING DOOR
SIIZE: W7.3 X H14M
INTERNAL DOOR LEAF NO - 01
QTY - 01 NOS


SPECIAL INSTRUCTION'S :

TITLE - DOOR AUTOMATION				NIHVA Technologies Pvt. Ltd.	NIHVA TECHNOLOGIES PVT.LTD.PUNE Website - www.nihva.com
DWG NO - NTPL-0007-PM-001				PRODUCT - BI-PARTING SLIDING HANGER DOOR	
	NAME	SIGNATURE	DATE		
DRAWN	J.P.		07-08-2026	PROJECT NO - NTPL-0007	REVISION - 00
CHK'D	B.S.		09-08-2026	SITE LOCATION - HYDERABAD	WEIGHT -
APPV'D	V.T.		09-08-2026	MATRIAL -	QTY - 1
If any queries contact - Sales@nihva.com				PROJECTION METHOD:	SCALE :
ALL DIMENSION ARE IN mm			A2		SHEET 1 OF 2

DRAWING

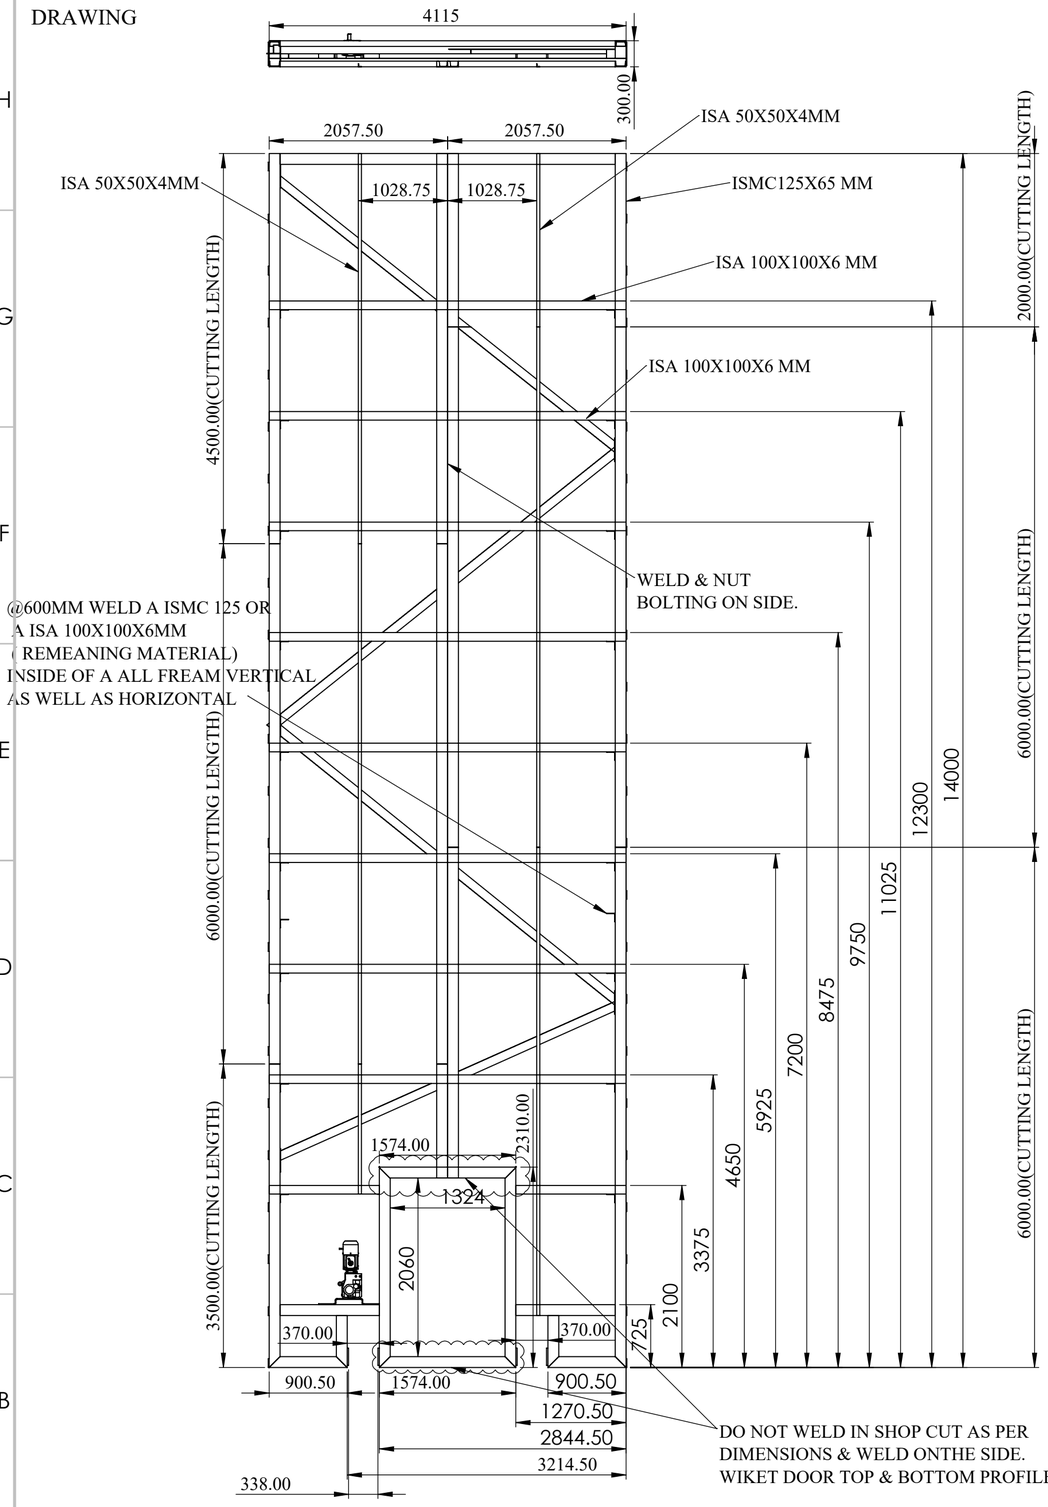


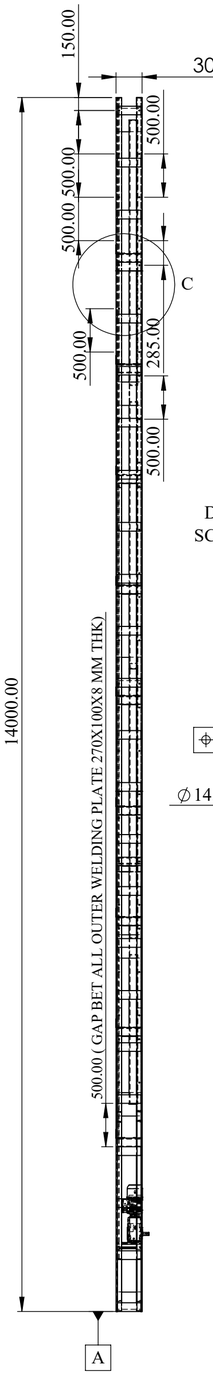


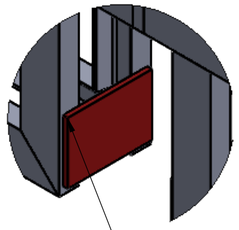

DETAIL D
SCALE 1 : 10

WHEEL BRACKET
MOUNTING PLATE
275X200X16MM THK

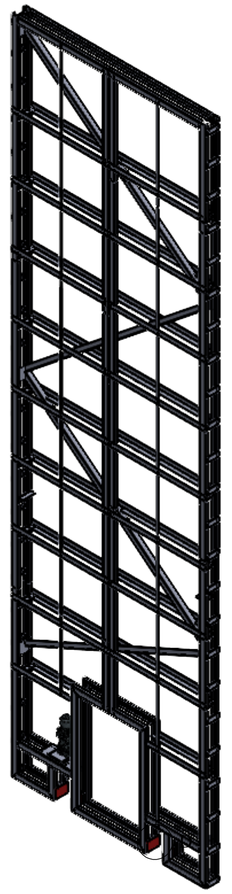

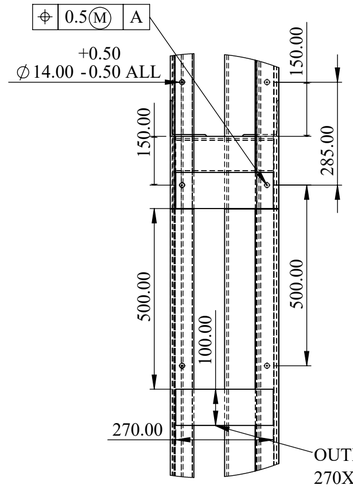

DETAIL C
SCALE 1 : 12

REV DESCRIPTION	DATE	REV NO
	08-08-2025	REV 00
1.		

NOTE :

NAME: HANGER SLINDING DOOR
SIIZE: W7.3 X H14M
INTERNAL DOOR LEAF NO - 02
QTY - 01 NOS

SPECIAL INSTRUCTION'S :

TITLE - DOOR AUTOMATION			
DWG NO - NTPL-0007-PM-001			
	NAME	SIGNATURE	DATE
DRAWN	J.P.		07-08-2026
CHK'D	B.S.		09-08-2026
APPV'D	V.T.		09-08-2026
If any queries contact - Sales@nihva.com			
ALL DIMENSION ARE IN mm		A2	

NIHVA Technologies Pvt. Ltd.

NIHVA TECHNOLOGIES PVT.LTD.PUNE
Website - www.nihva.com

PRODUCT - BI-PARTING SLIDING HANGER DOOR	
PROJECT NO - NTPL-0007	REVISION - 00
SITE LOCATION - HYDERABAD	WEIGHT -
MATRIAL -	QTY - 1
PROJECTION METHOD:	SCALE :
	SHEET 2 OF 2