
The reproduction, distribution and utilization of this document as well as the disclosure of its content to others without prior explicit written consent of SMS Meer GmbH is prohibited. Holder has to protect this document against unauthorized withdrawal of third parties. Offenders will be held liable for the payment of damages. All rights reserved in case of patent/utility model/trademark protection.

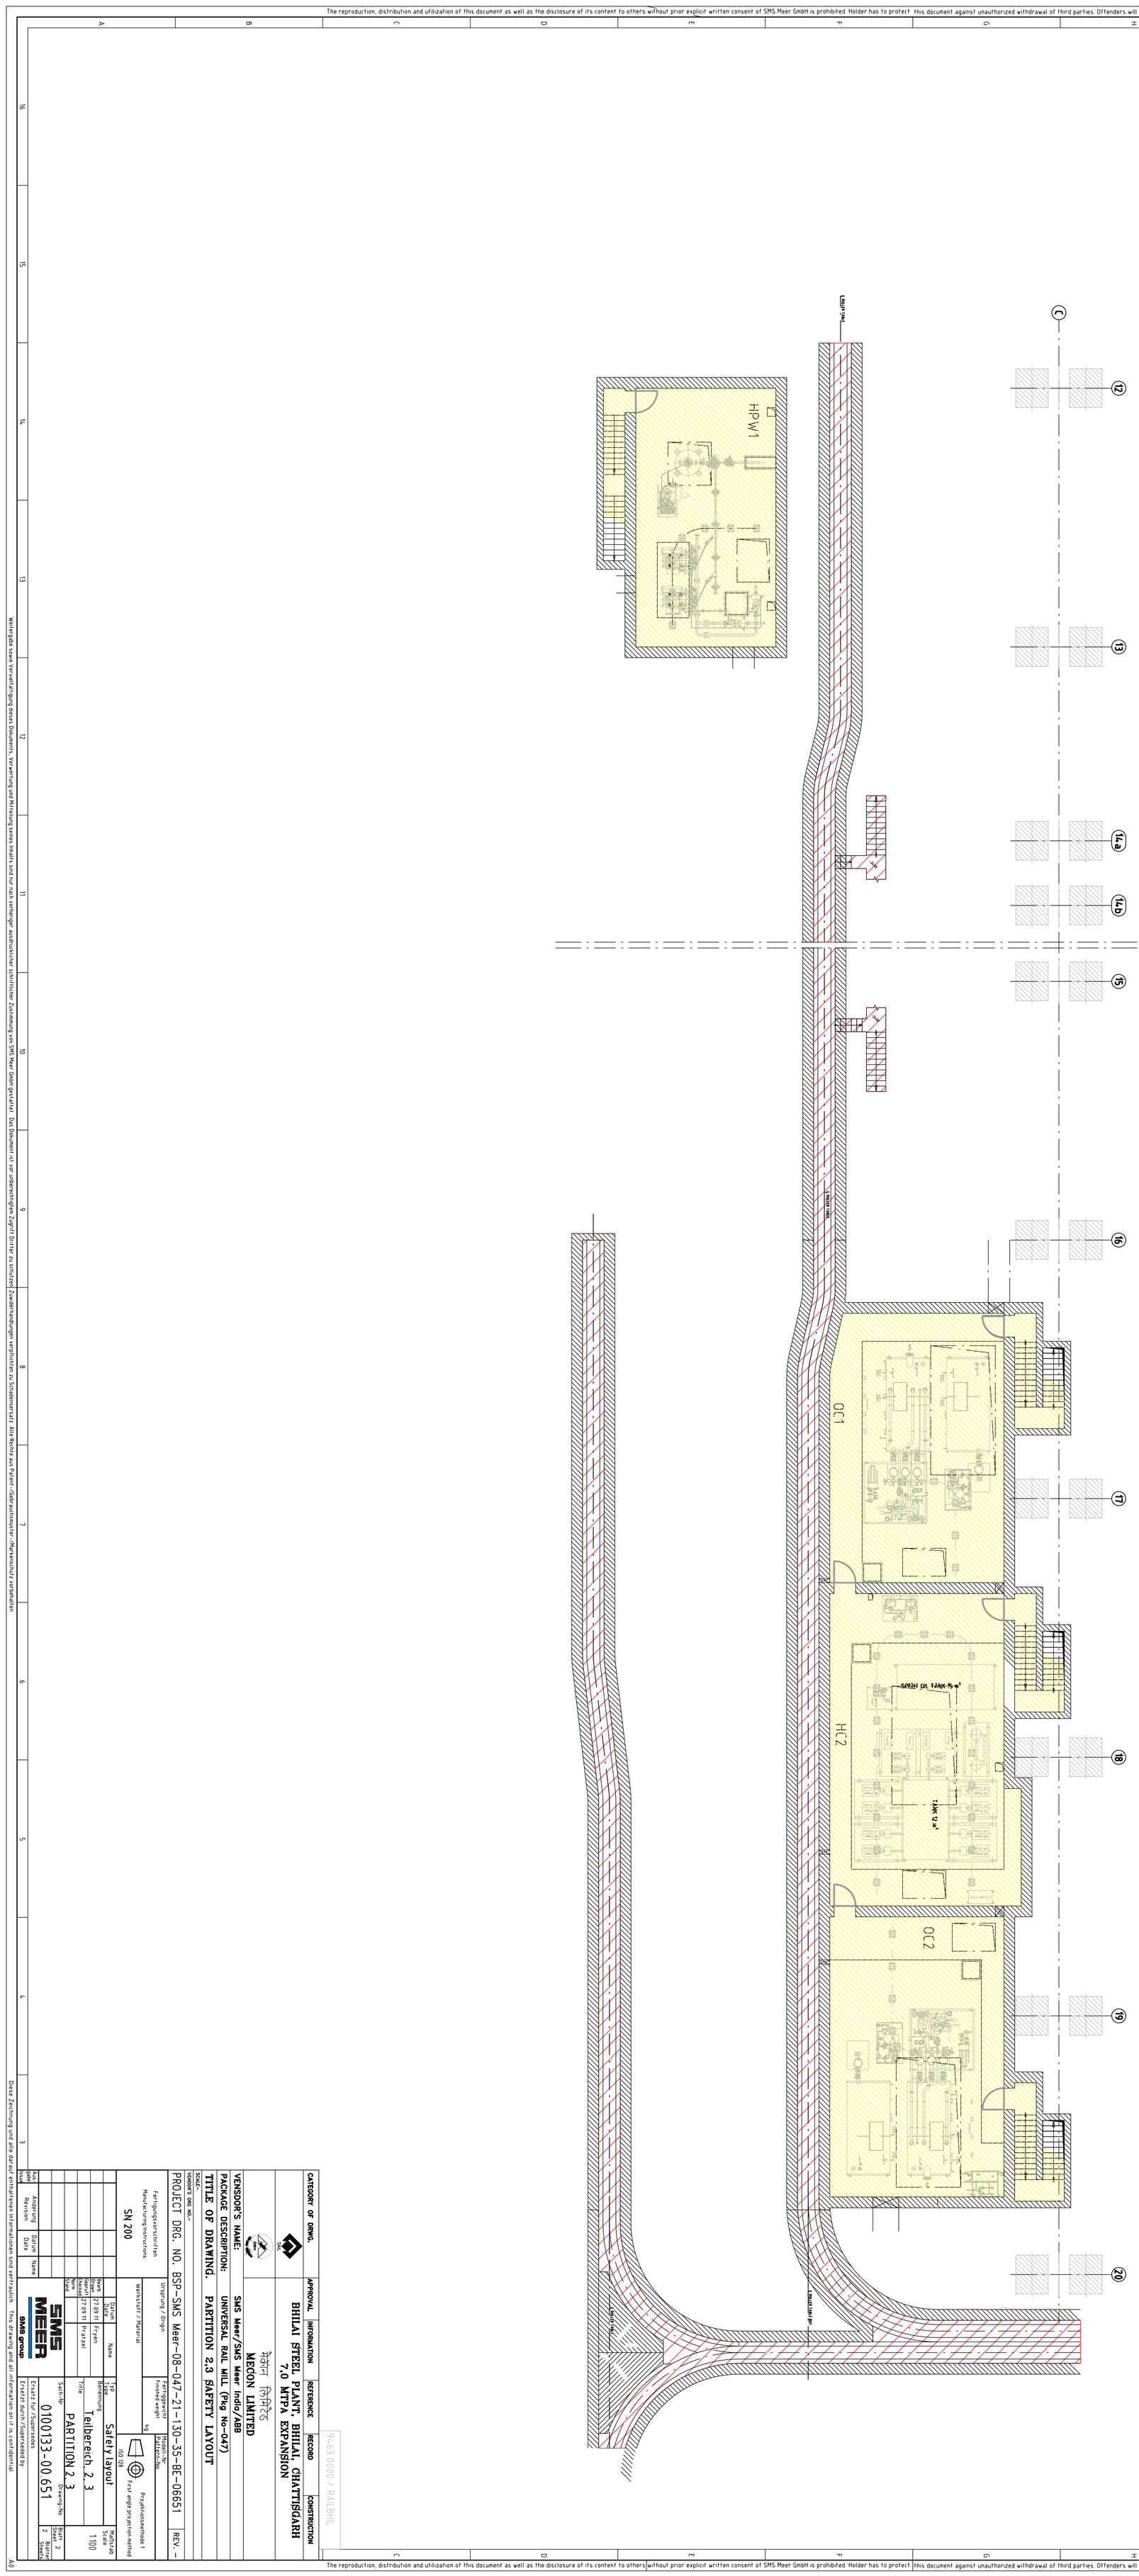

CATEGORY OF DRWG.	APPROVAL	INFORMATION	REFERENCE	RECORD	CONSTRUCTION
	BHILAI STEEL PLANT, BHILAI, CHATTISGARH 7.0 MTPA EXPANSION			9463 0000 / RAILBHIL	
	MECON LIMITED				
VENDOR'S NAME:	SMS Meer/SMS Meer India/ABB				
PACKAGE DESCRIPTION:	UNIVERSAL RAIL MILL (Pkg No-047)				
TITLE OF DRAWING.	PARTITION 2,3 SAFETY LAYOUT				
VENDOR'S DRG. NO.-					
PROJECT DRG. NO. BSP-SMS Meer-08-047-21-130-35-BE-06651					REV. -

Ursprung / Origin	Fertiggewicht Finished weight	kg	Modell-Nr. Pattern-No		
Fertigungsvorschriften Manufacturing instructions	Werkstoff / Material		ISO 128	First angle projection method	Projektionsmethode 1
SN 200					

	Datum Date	Name	Typ Type Benennung	Safety layout	Maßstab Scale
Bearb. Drawn	27 09 11	Fryen			1:100
Gepr. Checked	27 09 11	Pratzel	Titel	Teilbereich 2,3	
Norm Standard			Sach-Nr	PARTITION 2,3	Blatt Sheet 2
				Drawing-No.	Blätter Sheets 2
			0100133-00 651		

Änderung Revision	Datum Date	Name

Ersatz für/Superseded

Ersatz durch/Superseded by

SMS MEER
SMS group

Diese Zeichnung und alle darauf enthaltenen Informationen sind vertraulich. This drawing and all information on it is confidential.

The reproduction, distribution and utilization of this document as well as the disclosure of its content to others without prior explicit written consent of SMS Meer GmbH is prohibited. Holder has to protect this document against unauthorized withdrawal of third parties. Offenders will be held liable for the payment of damages. All rights reserved in case of patent/utility model/trademark protection.