




INSIDE ELEVATION

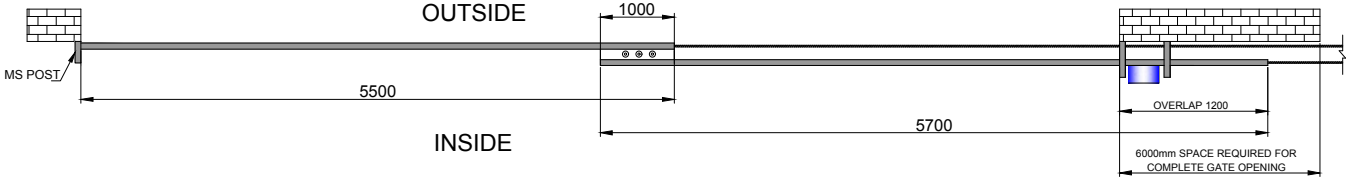

INSIDE

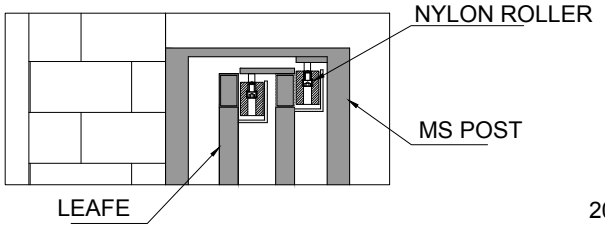

DETAILED VIEW OF 'B'

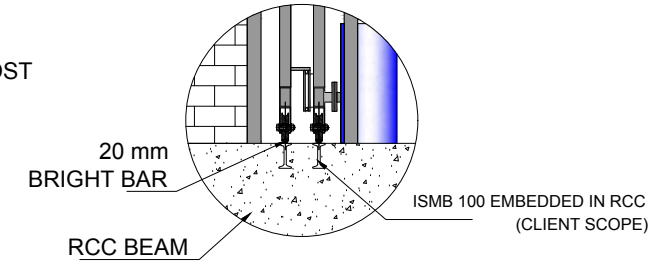

DETAILED VIEW OF 'A'

TOLERANCE- ±10mm

DIMENSION :

CLEAR WIDTH	CLEAR HEIGHT	QUANTITY
9000mm	2000mm	1 NO

MATERIAL:

THICKNESS :

NOTE-
1. ALL REQUIRED CIVIL WORK WILL BE IN CLIENTS SCOPE.
2. ONE COAT OF RED OXIDE SHADE WILL BE GIVEN TO THE GATE.

NIHVA
NIHVA TECHNOLOGIES PVT. LTD.
NIHVA TECHNOLOGIES PVT. LTD. PUNE
Email:- info@nihva.com
Website:- www.nihva.com

TITLE:
2 LEAF TELESCOPIC (MOTORIZED)

CLIENT'S APPROVAL :

CLIENT - GROUP SURYA
PROJECT - CUMMINS
SITE LOCATION -
DWG. NO. : NIHVA/19-20/0116

SCALE: NTS	WT:	SHEET:1 OF 1
DRAWN BY: P.V.A		DATE: 09.10.2019
CHECK BY :		DATE:
APPROVED BY :		DATE:

If any queries contact : design@nihva.com
NOTE: ALL DIMENSIONS ARE IN mm

THIS DRAWING & DESIGN IS THE PROPERTY OF NIHVA TECHNOLOGIES. NOT TO BE SOLD OR COPIED TO ANY OTHER CONCERN.