



PRODUCED BY AN AUTODESK EDUCATIONAL PRODUCT

DOOR LOCATION - GRID Q1- Q2

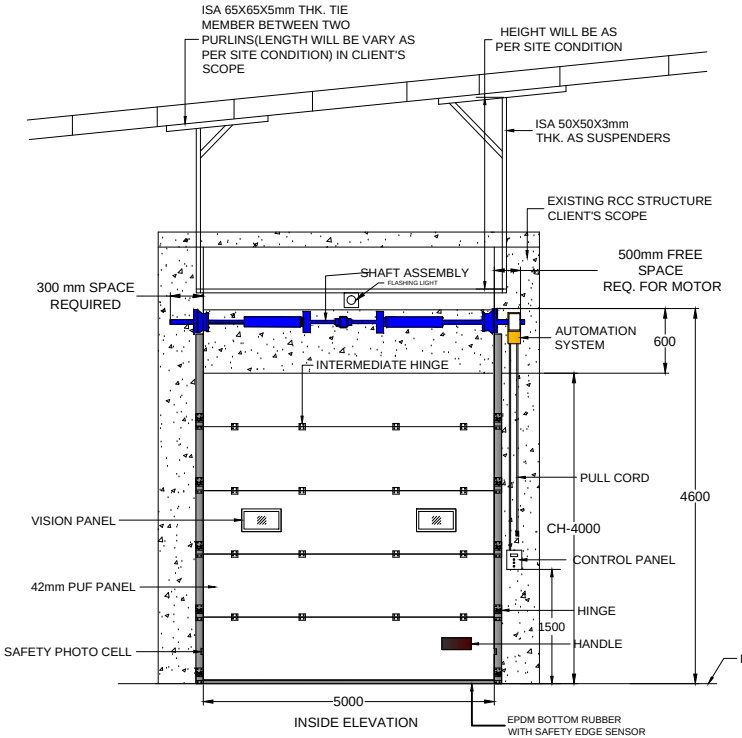

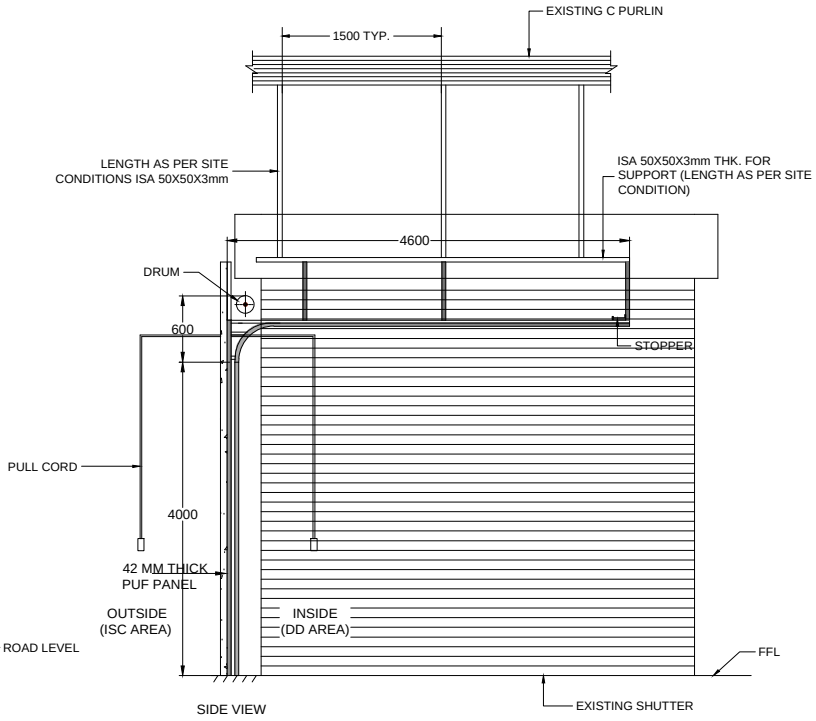

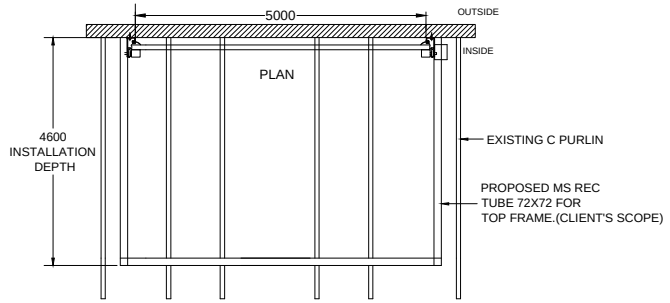

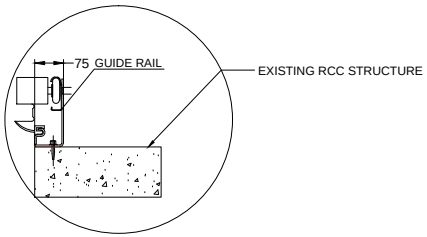

DIMENSION :

CLEAR WIDTH	CLEAR HEIGHT	QUANTITY
5000 mm	4000 mm	1

TECHNICAL DATA :

COMPONENTS	MATERIALS	SPECIFICATIONS
DOOR PANELS	GI & PUF	42mm CFC- FREE POLYURETHANE WITH 0.5mm THK, GI PRECOATED PANELS.
DOOR HINGE	——	HEAVY DUTY HINGES FOR INTERLOCKING OF PANELS
SHAFT ASSEMBLY	STD.	TORSIONAL SPRING WITH SHAFT & BEARING PLATES
FINISH		ENAMEL PAINT WITH APPROVED SHADE RAL 5012 LIGHT BLUE

ACCESSORIES-
1. SAFETY PHOTOCELL- 1 PAIR /DOOR
2. FLASH LIGHT- 2 SIDE OF DOOR
3. PULL CORD SWITCH- 1 SINGLE SIDE

IMPORTANT NOTES:

1. REQUIRED STRUCTURE FOR DOOR SHALL BE IN CLIENT'S SCOPE.
2.SINGLE PHASE POWER SUPPLY REQUIRED AT DOOR LOCATION.
3.ALL CIVIL WORK SHALL BE CLIENT'S SCOPE.

NIHVA TECHNOLOGIES PVT. LTD.
NIHVA TECHNOLOGIES PVT. LTD. PUNE
Email:- info@nihva.com
Website:- www.nihva.com

TITLE:

SECTIONAL DOOR SL 1 (MOTORIZED)

CLIENT'S APPROVAL :

CLIENT - SCON PROJECTS

PROJECT - BEKAERT INDUSTRIES PVT.LTD.

SITE LOCATION - RANJANGAON, MIDC

DWG. NO. : NIHVA/17-18/0140

SCALE: NTS	WT:	SHEET:1 OF 1

DRAWN BY: OMKAR	DATE: 05-08-2017
CHECK BY: SHEKHAR	DATE: 05-08-2017
APPROVED BY : SHEKHAR	DATE: 05-08-2017

If any queries contact : projects@nihva.com

NOTE: ALL DIMENSIONS ARE IN mm

PRODUCED BY AN AUTODESK EDUCATIONAL PRODUCT
PRODUCED BY AN AUTODESK EDUCATIONAL PRODUCT
PRODUCED BY AN AUTODESK EDUCATIONAL PRODUCT