
0.23m Wall

0.15m Wall

RCC BEAM GRID

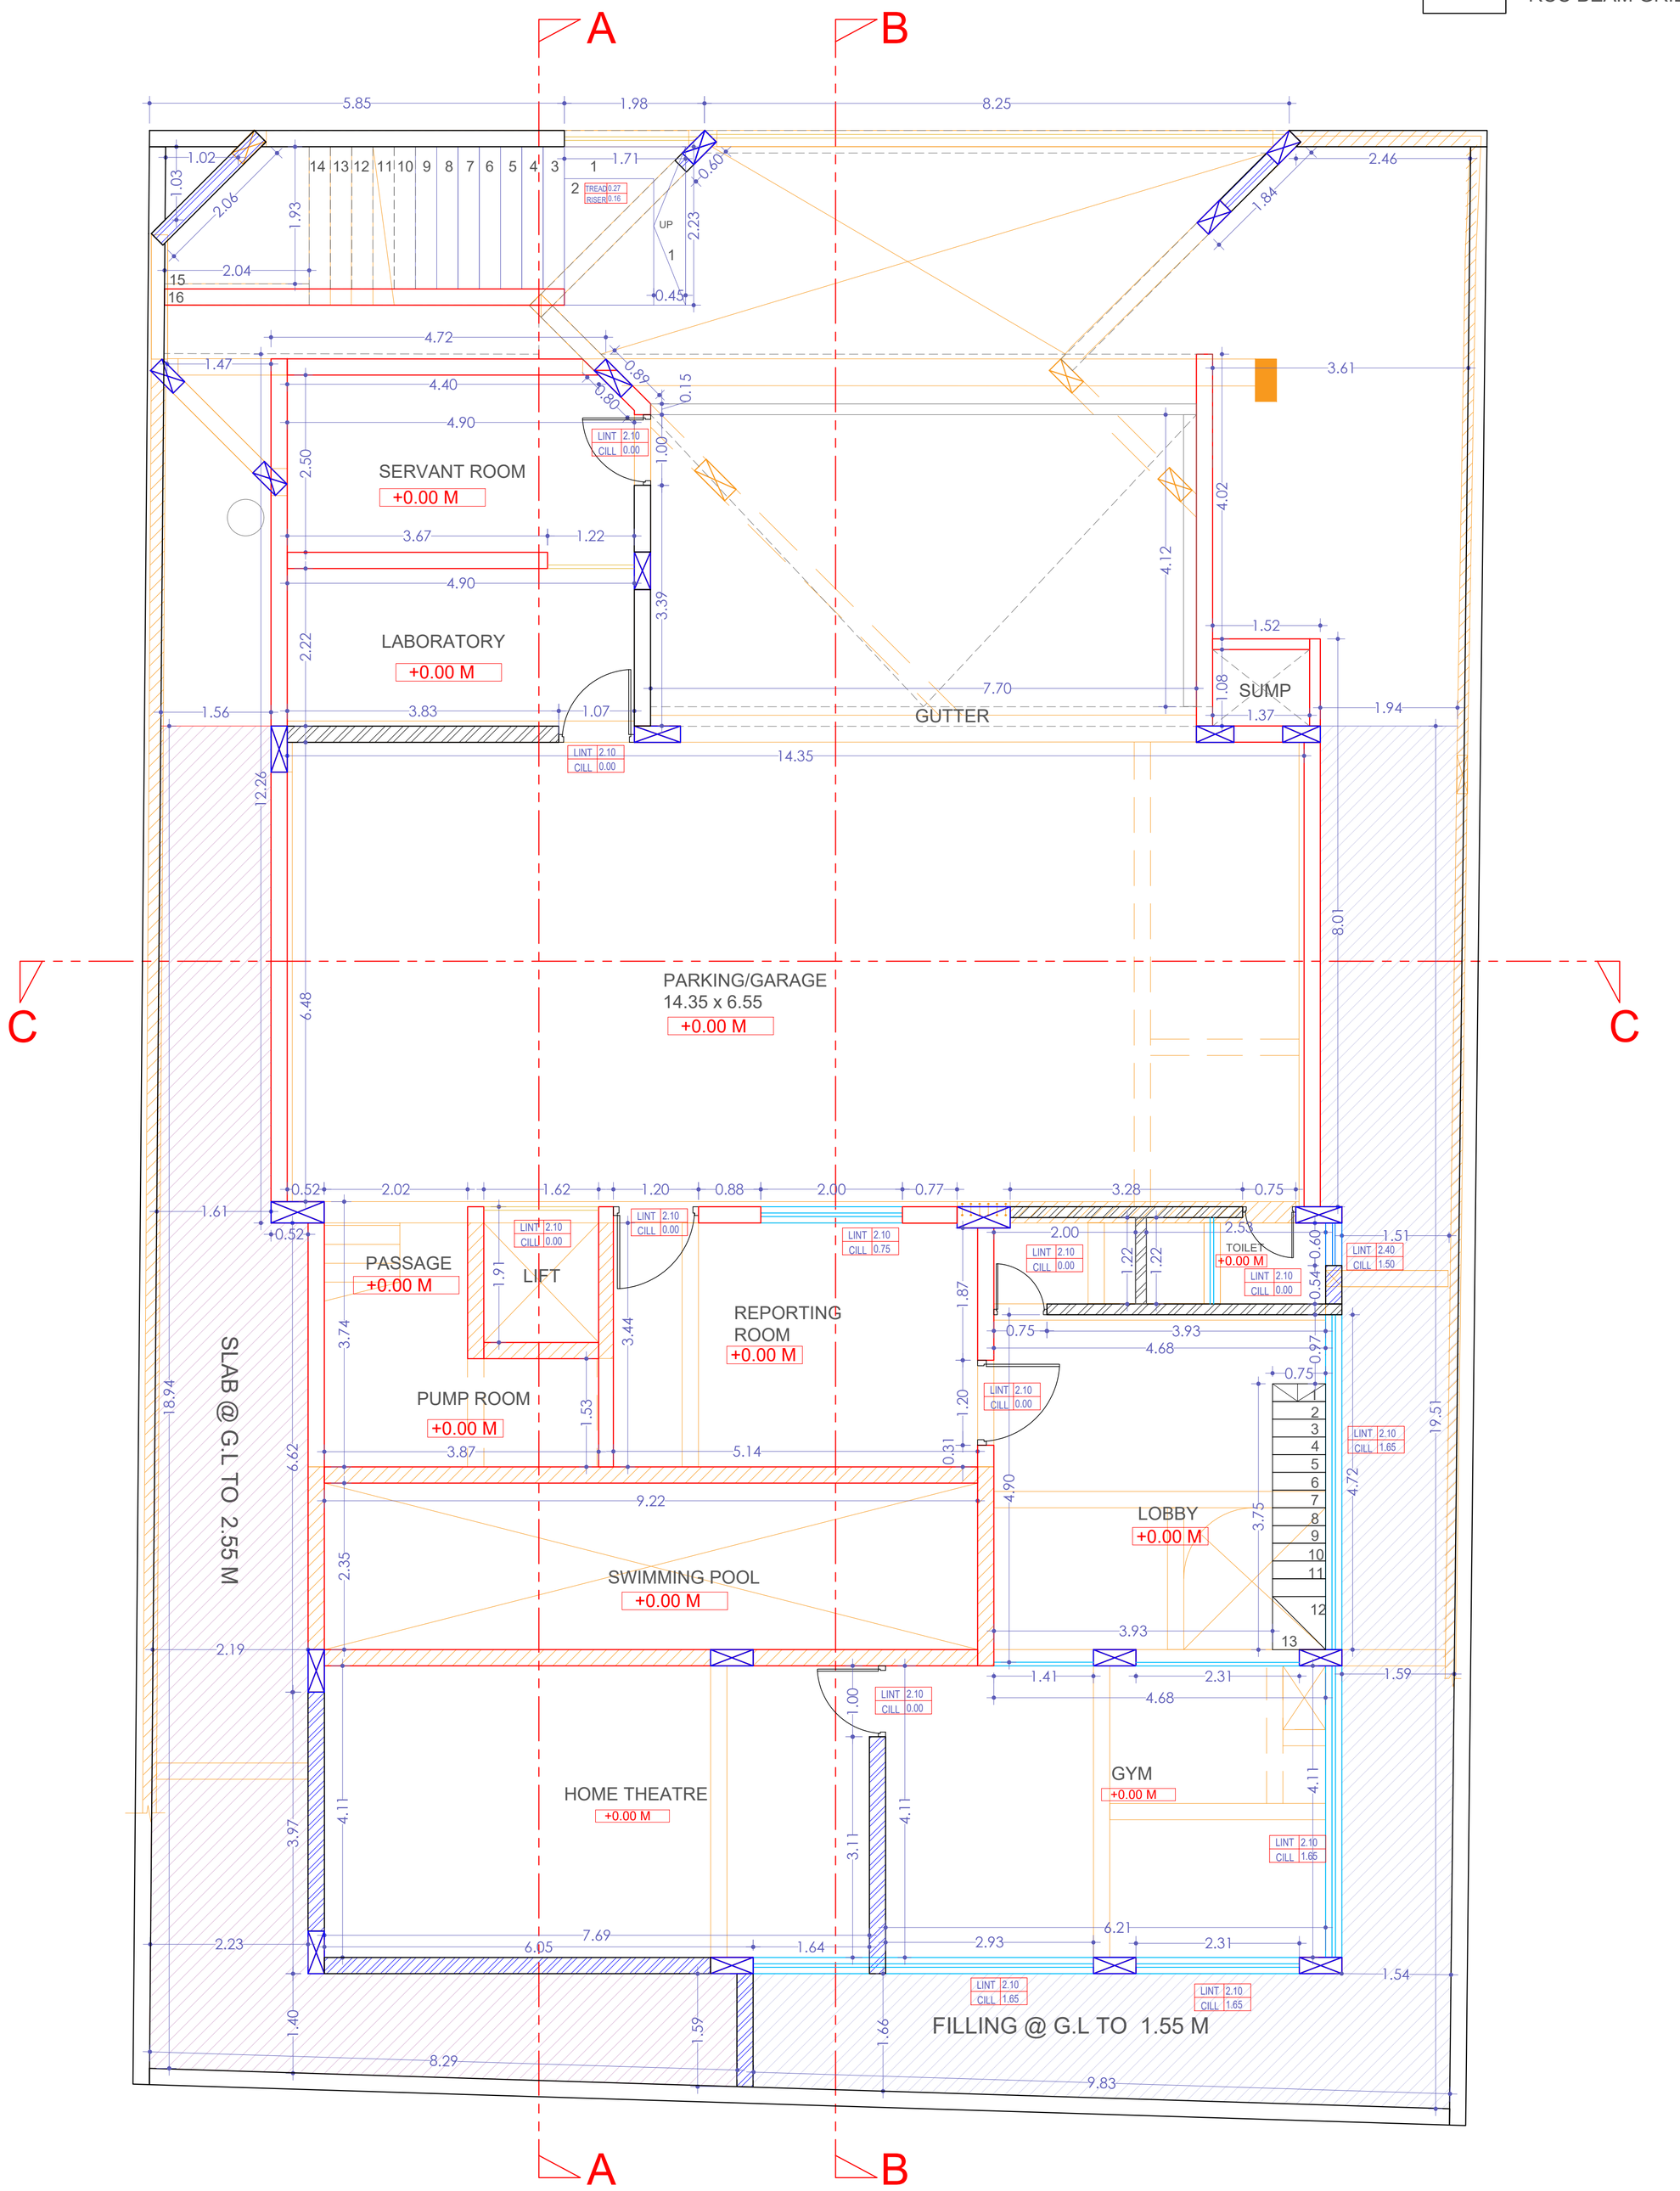

GROUND FLOOR PLAN - @0.00LVL

PROJECT : PROPOSED WORKING DRAWING FOR DR.NIKAM AT KARAD.	JOB NO : P153	DRN BY : Sarthavi Shah	1. This Drawing is a copyright of PRANEEL MULICK ASSOCIATE. and should not be retained, copied or used Without their authority. 2. Do not scale the drawing. 3. This Drawing to be read along with other relevant drawings. 4. Any variation between the drawing & specification should be brought to the notice of the architects by the contractors in writing prior to the construction.
TITLE : GROUND FLOOR PLAN	DWG NO : P153-WD-GF-01	CHK BY : Praneel Mulick	
	SCALE : 1:100	ISSUE DATE : 01-01-26	

architecture
interior design
space planning


MULICK ASSOCIATE, SANGAM GAS,
NEAR HOTEL SANGAM
P.B.HIGHWAY. KARAD.415110
PH : 9970266774.
Email: praneelmulick@gmail.com

mulick associate

0.23m Wall

0.15m Wall

RCC BEAM GRID

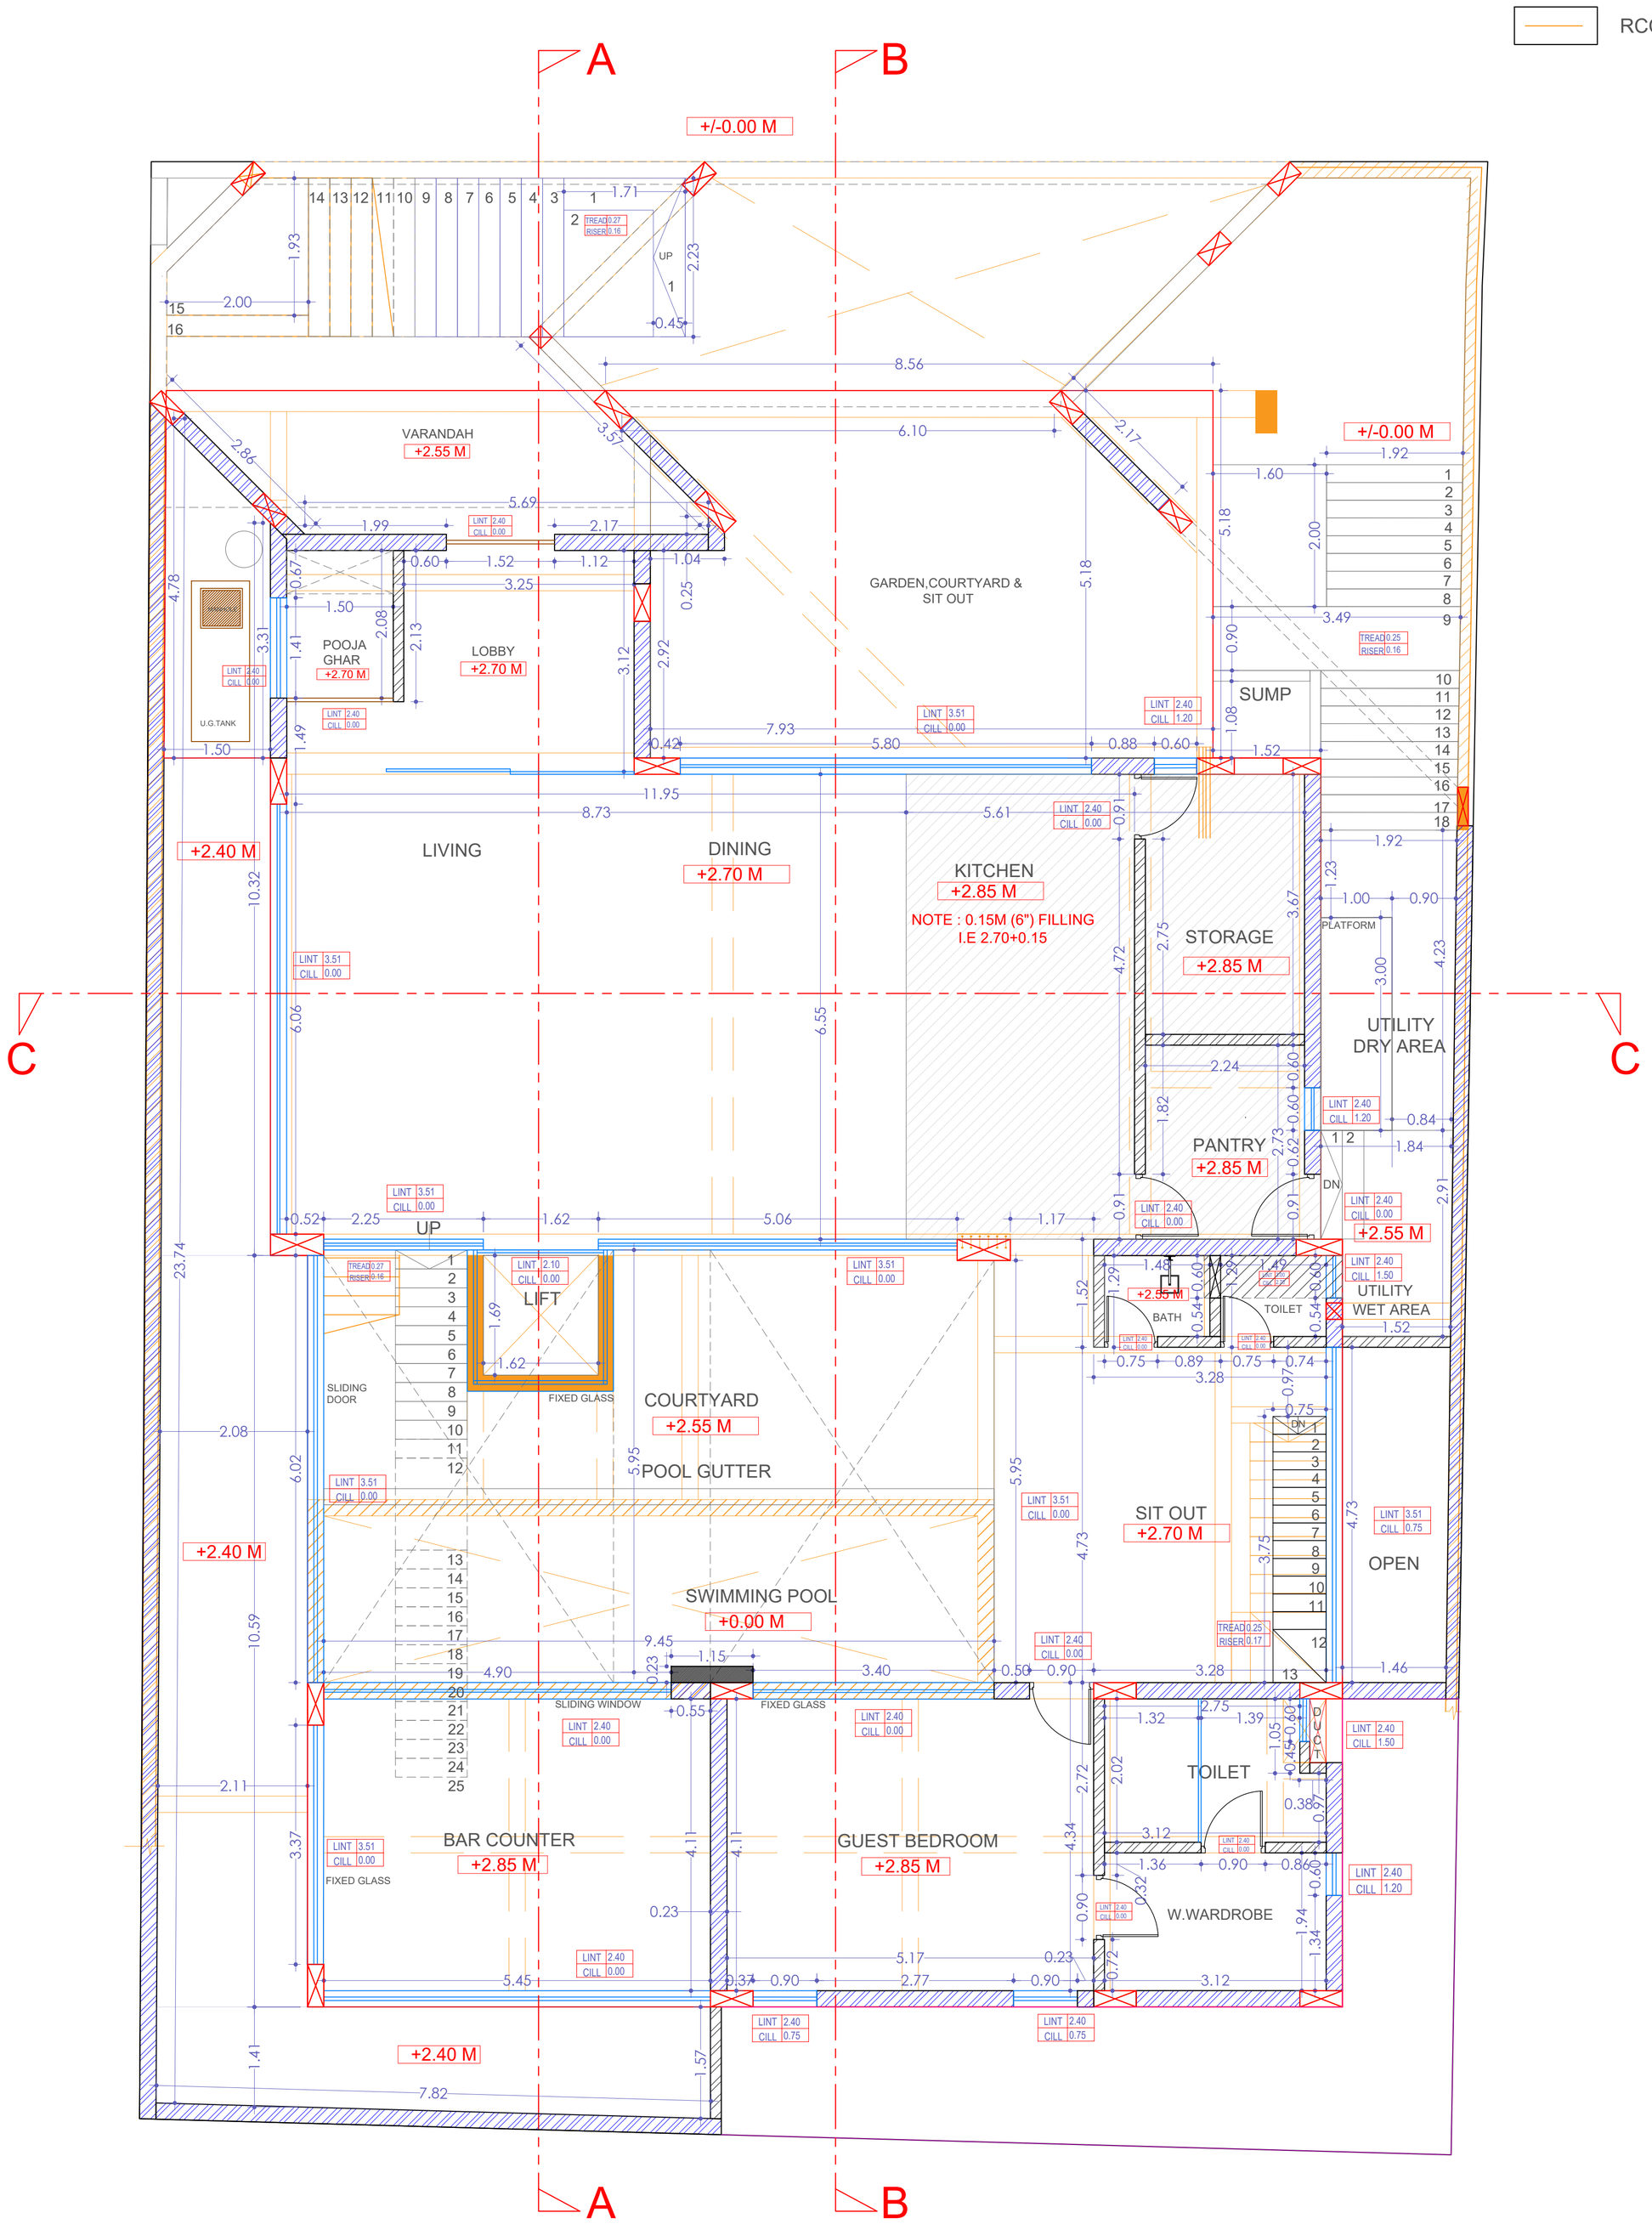


FIRST FLOOR PLAN - @2.70 LVL FROM 0.00

PROJECT : PROPOSED WORKING DRAWING FOR DR.NIKAM AT KARAD.	JOB NO : P153	DRN BY : Sarthavi Shah	1. This Drawing is a copyright of PRANEEL MULICK ASSOCIATE. and should not be retained, copied or used Without their authority. 2. Do not scale the drawing. 3. This Drawing to be read along with other relevant drawings. 4. Any variation between the drawing & specification should be brought to the notice of the architects by the contractors in writing prior to the construction.
TITLE : FIRST FLOOR PLAN	DWG NO : P153-WD-FF-01	CHK BY : Praneel Mulick	
	SCALE : 1:100	ISSUE DATE : 01-01-26	

architecture
interior design
space planning

MULICK ASSOCIATE, SANGAM GAS,
NEAR HOTEL SANGAM
P.B.HIGHWAY. KARAD.415110
PH: 9970266774.
Email: praneelmulick@gmail.com

mulick associate

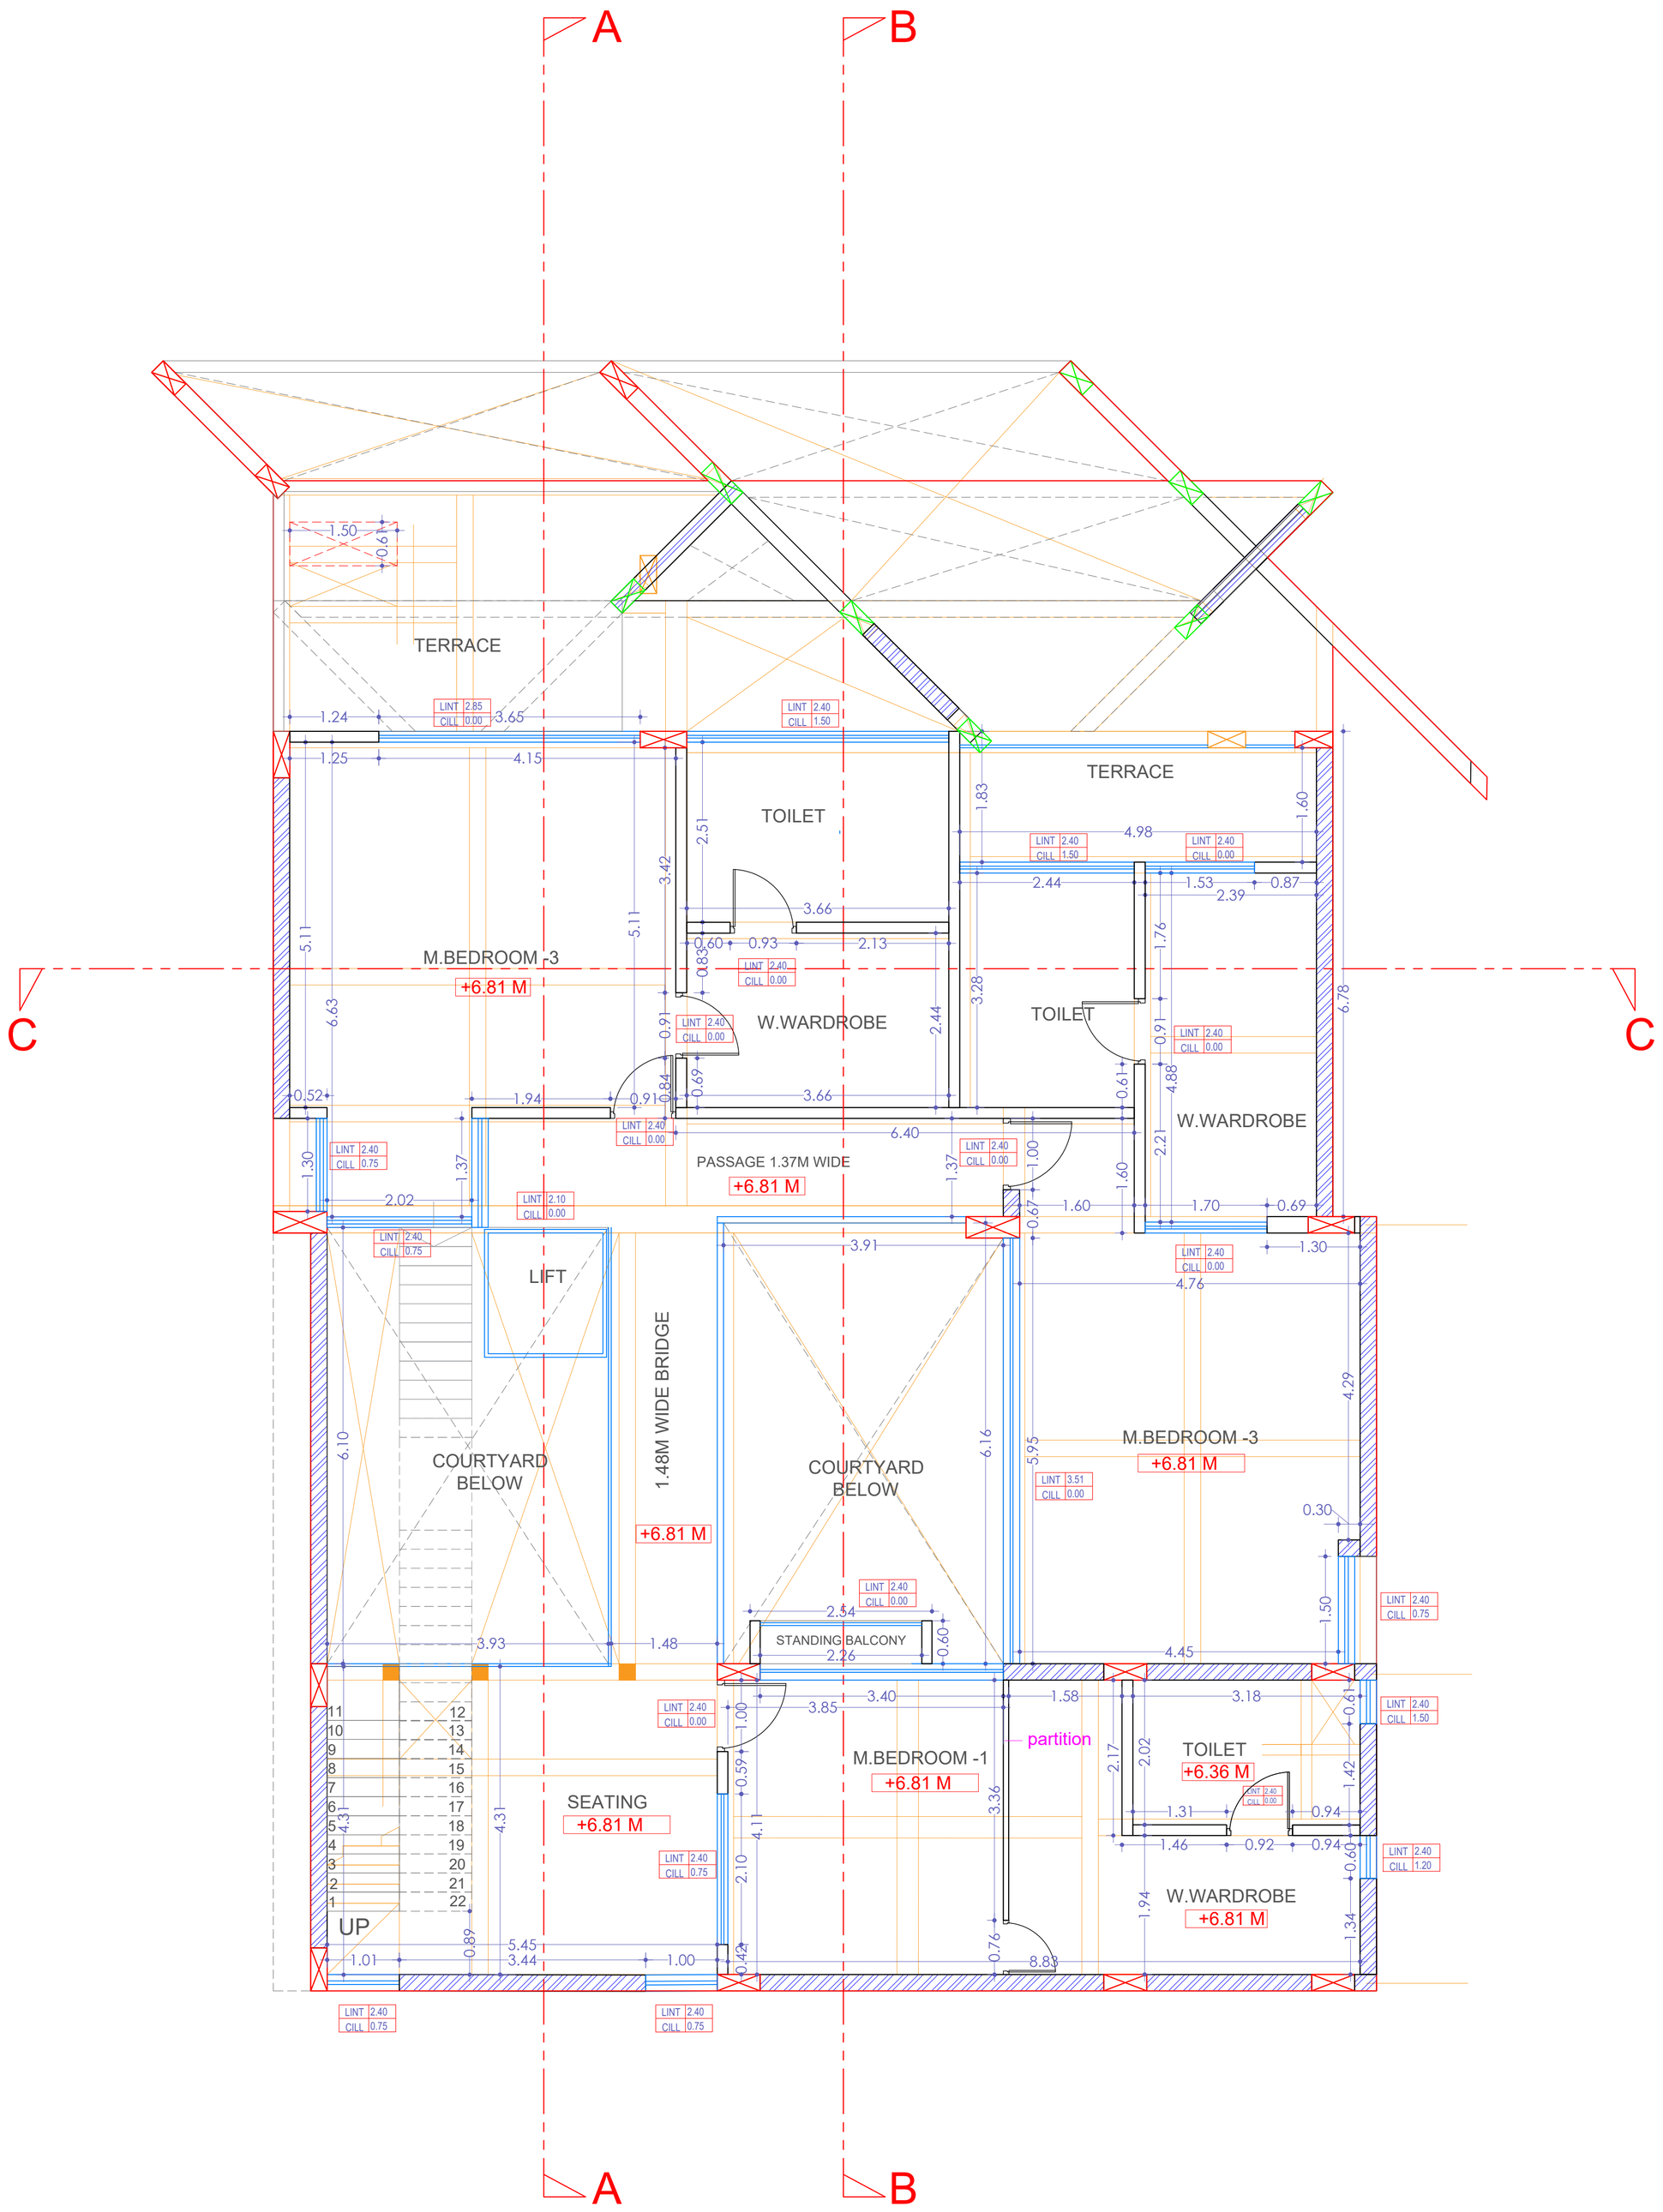


SECOND FLOOR PLAN - @6.81LVL FROM 0.00

PROJECT : PROPOSED WORKING DRAWING FOR DR.NIKAM AT KARAD.	JOB NO : P153	DRN BY : Sarthavi Shah	1. This Drawing is a copyright of PRANEEL MULICK ASSOCIATE. and should not be retained, copied or used Without their authority. 2. Do not scale the drawing. 3. This Drawing to be read along with other relevant drawings. 4. Any variation between the drawing & specification should be brought to the notice of the architects by the contractors in writing prior to the construction.
TITLE : SECOND FLOOR PLAN	DWG NO : P153-WD-SF-01	CHK BY : Praneel Mulick	
	SCALE : 1:100	ISSUE DATE : 01-01-26	

architecture
interior design
space planning

MULICK ASSOCIATE, SANGAM GAS,
NEAR HOTEL SANGAM
P.B.HIGHWAY. KARAD.415110
PH : 9970266774.
Email: praneelmulick@gmail.com

mulick associate

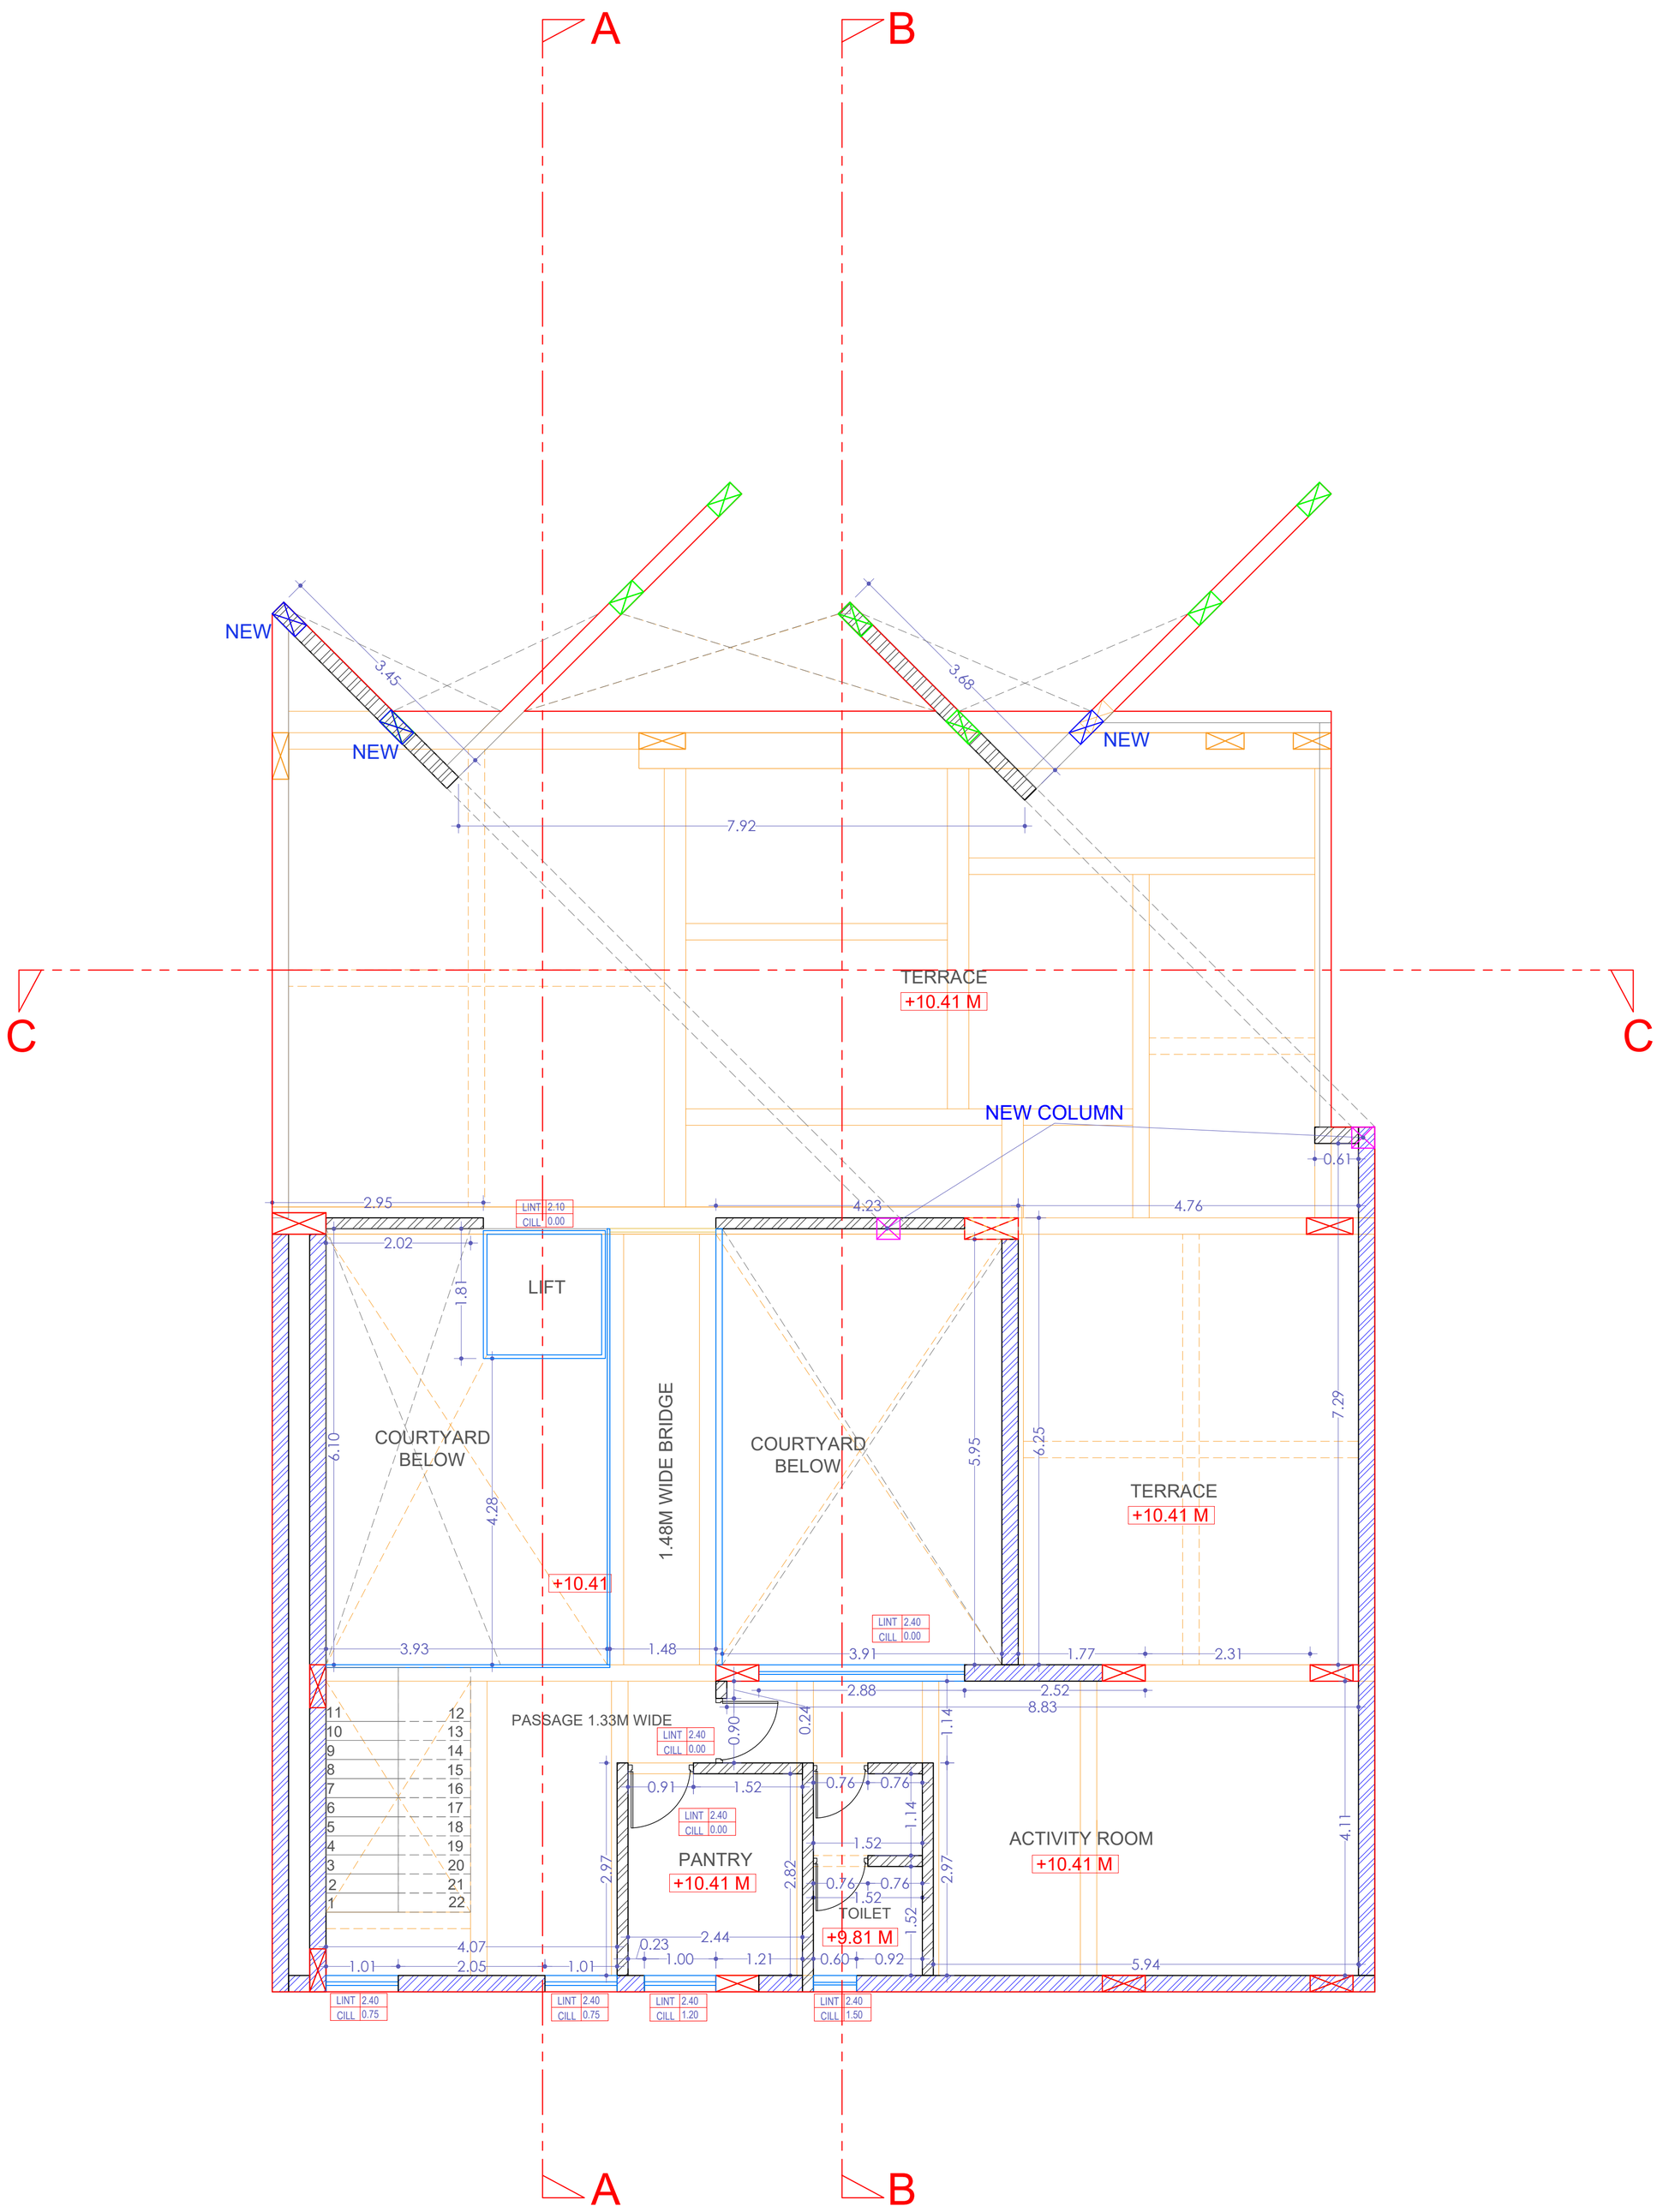

THIRD FLOOR PLAN - @10.41LVL

PROJECT : PROPOSED WORKING DRAWING FOR DR.NIKAM AT KARAD.	JOB NO : P153	DRN BY : Sarthavi Shah	1. This Drawing is a copyright of PRANEEL MULICK ASSOCIATE. and should not be retained, copied or used Without their authority. 2. Do not scale the drawing. 3. This Drawing to be read along with other relevant drawings. 4. Any variation between the drawing & specification should be brought to the notice of the architects by the contractors in writing prior to the construction.
TITLE : THIRD FLOOR PLAN	DWG NO : P153-WD-TF-01	CHK BY : Praneel Mulick	
	SCALE : 1:100	ISSUE DATE : 18-11-25	

architecture
interior design
space planning

MULICK ASSOCIATE, SANGAM GAS,
NEAR HOTEL SANGAM
P.B.HIGHWAY. KARAD.415110
PH : 9970266774.
Email: praneelmulick@gmail.com

mulick associate