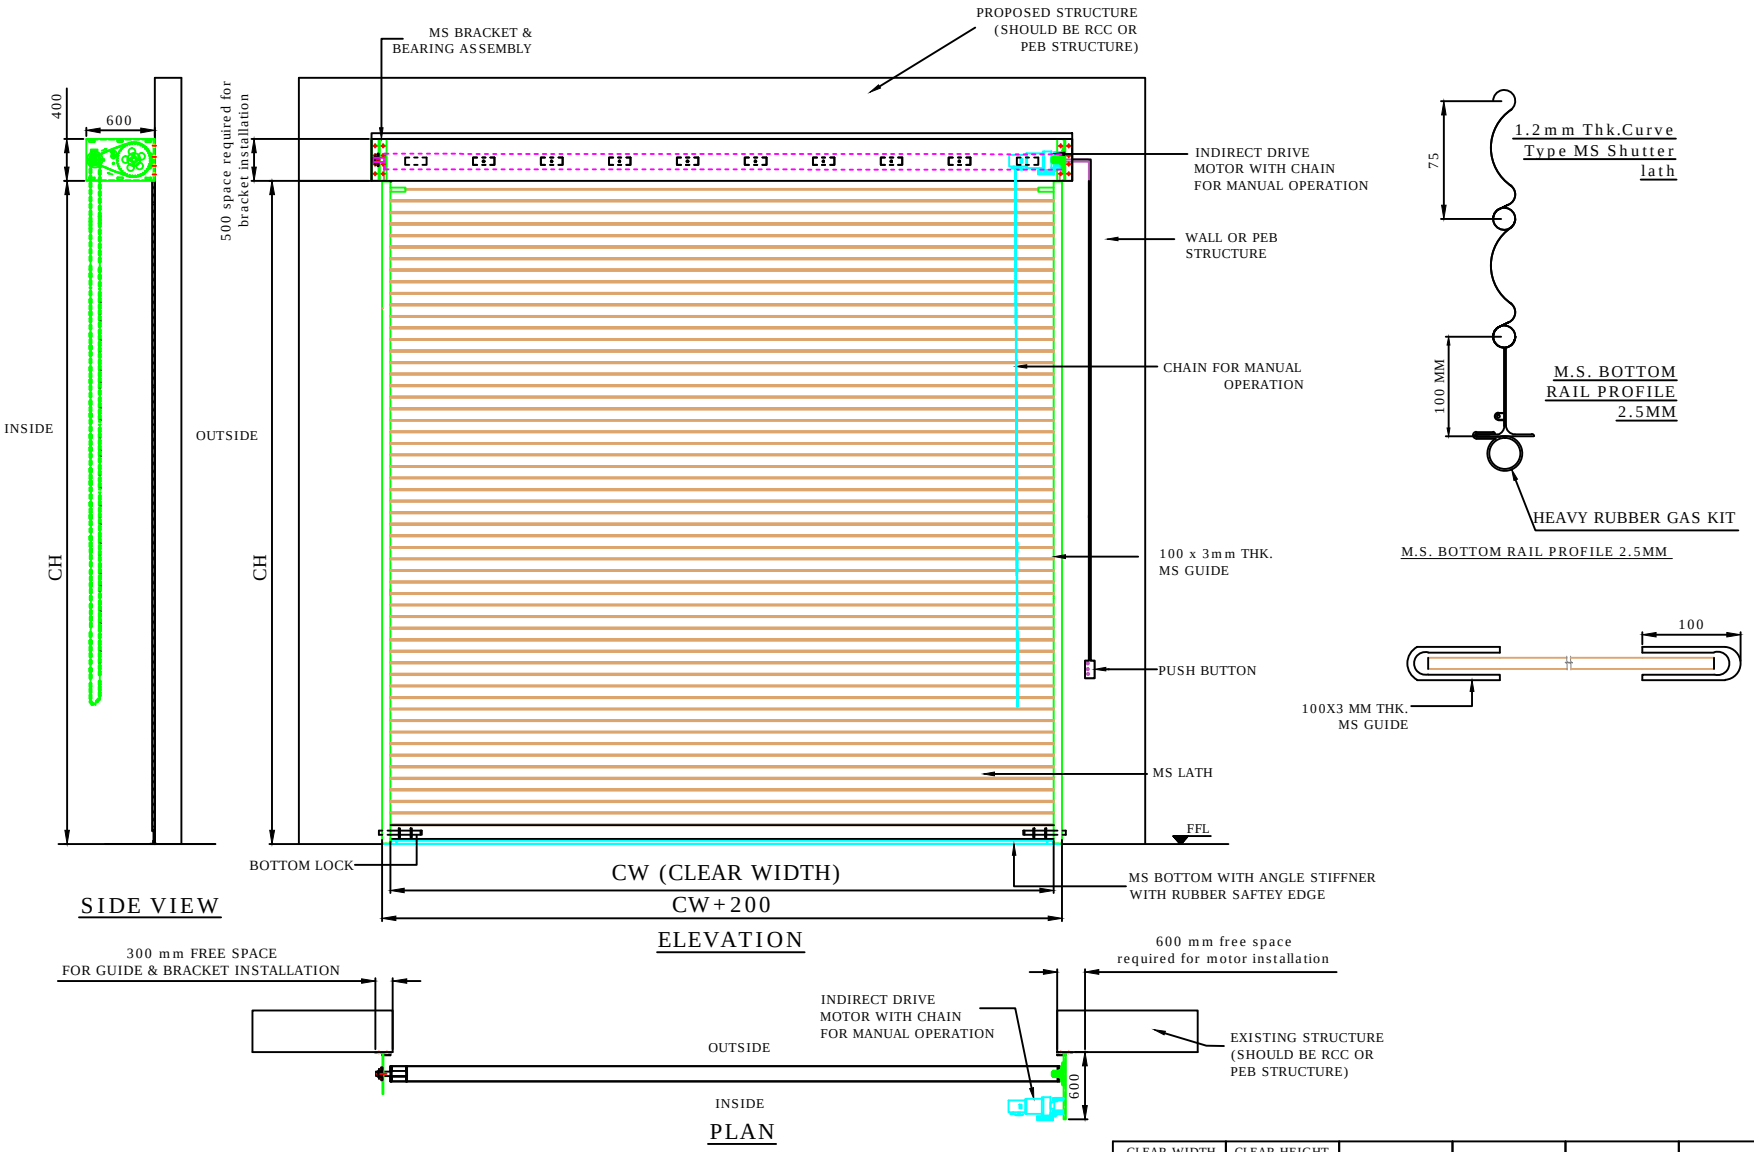


CLEAR WIDTH (CW)	CLEAR HEIGHT (CH)	GUIDE SIZE	BRACKET SIZE	SHAFT SIZE (O.D)	QUANTITY
4000	4200	100X3mm	400X400mm	140mm	2
3000	4000	100X3mm	400X400mm	140mm	6
4000	4000	100X3mm	400X400mm	140mm	3
3000	3600	100X3mm	400X400mm	140mm	1

TECHNICAL DATA

COMPONENTS	MATERIAL	SPECIFICATION
SLATS	MS	1.2mm CURVED TYPE MS SLAT
SIDE GUIDE	MS	100X2.5 mm
BOTTOM PROFILE WITH ANGLE STIFFNER	MS	125X2.5mm BOTTOM PROFILE WITH 40mm MS ANGLE.
BRACKET PLATES	MS	—
ROLLER SHAFT	MS	—
HOOD COVER	GI	0.9mm THK.
AUTOMATION SYSTEM	—	JIELONG MAKE INDIRECT DRIVE MOTOR (MADE IN CHINA)
PRIMER	—	A COAT OF RED OXIDE ZINC CHROMATE WILL BE GIVEN.
STANDARD FINISH	—	FINAL COLOR SHADE WILL BE IN CLIENT'S SCOPE.

NOTE:
1.REQUIRED STRUCTURE FOR SHUTTER SHALL BE IN CLIENT SCOPE.
2.SINGLE PHASE POWER SUPPLY REQUIRE.
3.FOR POWER SUPPLY 3 CORE 1.5 SQ.mm CABLE REQUIRE.

LOCATION OF SHUTTER

CLEAR WIDTH	CLEAR WIDTH	QUANTITY	LOCATION
4000mm	4200mm	2	MRS BUILDING
3000mm	4000mm	4	SUBSTATION
4000mm	4000mm	3	COMPRESSOR ROOM
3000mm	4000mm	2	COMPRESSOR ROOM
3000mm	3600mm	1	UG TANK

CLIENT:
& BOYCE MFG. CO. LTD.
CONSULTANCY SERVICES FOR DETAILED ENGINEERING OF INDUSTRIAL EXPANSION PROJECT

PROJECT:
GODREJ & BOYCE MFG. CO. LTD.
PROPOSED INDUSTRIAL EXPANSION AT VILLAGE VADVAL AND TAMBATI. TAL. KHALAPUR, DIST. RAIGAD.

ARCHITECT/CONSULTANT:
TATA CONSULTING ENGINEERS LIMITED
MUMBAI

PMC:
CUSHMAN & WAKEFIELD
Cushman wakefield India Pvt. Ltd. Onyx 11th Floor, North Main Road, Next to Westin Hotel, Koregaon Park, Pune 411001, India.

CONTRACTOR:
RATILAL BHAGWANDAS CONSTRUCTION COMPANY PVT. LTD. PUNE.

NIHVA TECHNOLOGY PVT. LTD. PUNE
NIHVA TECHNOLOGIES PVT. LTD.
Email:- info@nihva.com
Website:- www.nihva.com

DWG TITLE:
MOTORIZED ROLLING SHUTTER

SO Ref. No- SO/16-17/0073

DRN BY:	SCALE:	DWG NO:	REV NO:
OMKAR	NTS	NIHVA/16-17/0086/R01	1
CHKD BY: SAGAR P	DATE: 15-11-2016		

If any queries contact : projects@nihva.com

NOTE: ALL DIMENSION ARE IN mm

THIS DRAWING & DESIGNING IS THE PROPERTY OF NIHVA TECHNOLOGIES. NOT BE SOLD OR COPY TO ANY OTHER CONCERN.