



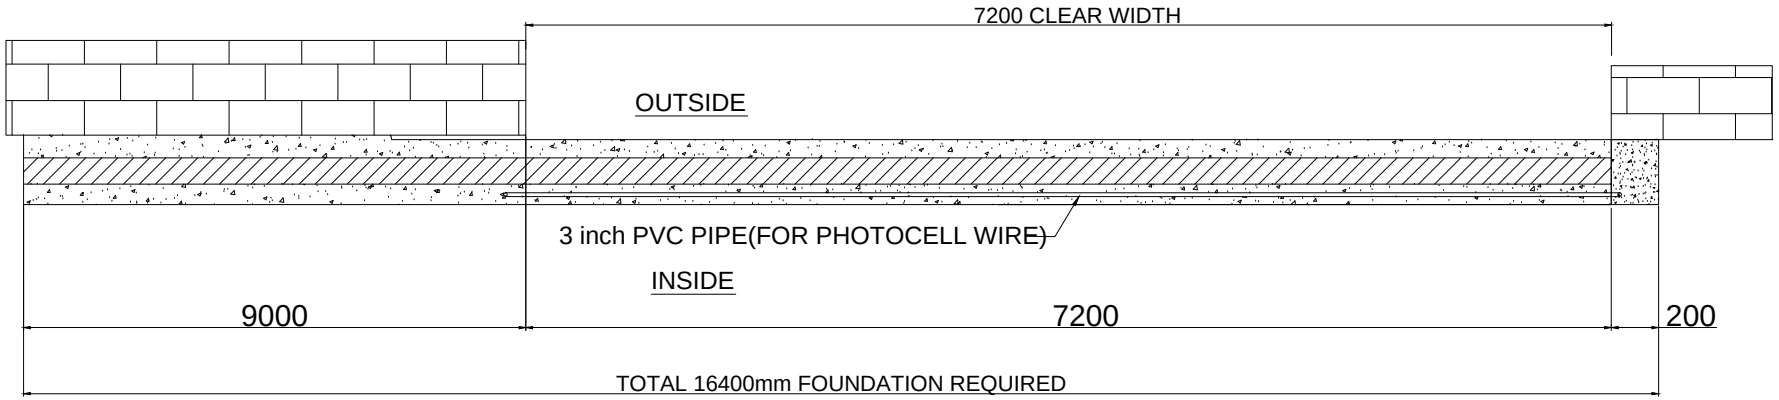

PLAN

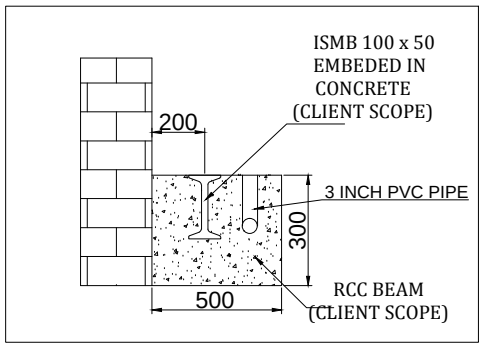

REVISION 2(25/04/2018)- FOUNDATION REVISED AS PER 7.2m WIDTH

This drawing & design is the property of NIHVA TECHNOLOGIES. Not to be sold or copied to any other concern.

TITLE: FOUNDATION OF SLIDING GATE 7.2X1.8m GATE NO 6			NIHVA TECHNOLOGIES PVT. LTD. PUNE Tel : 020 66304033 Email:- info@nihva.com Website:- www.nihva.com
	SIGN	DATE	
DRAWN	SURAJ	15/09/17	CLIENT - TATA PROJECT
CHECK	SAGAR P.	15/09/17	PROJECT - ALSTOM
REV.			SITE LOCATION -MADHEPURA,BIHAR
APPROVAL	S.S	15/09/17	DWG. NO. : NIHVA/17-18/0088/R02 / REV- 02
If any queries contact : projects@nihva.com			SCALE: NTS / WT: / SHEET: 01 OF 01
ALL DIMENSION ARE IN mm			