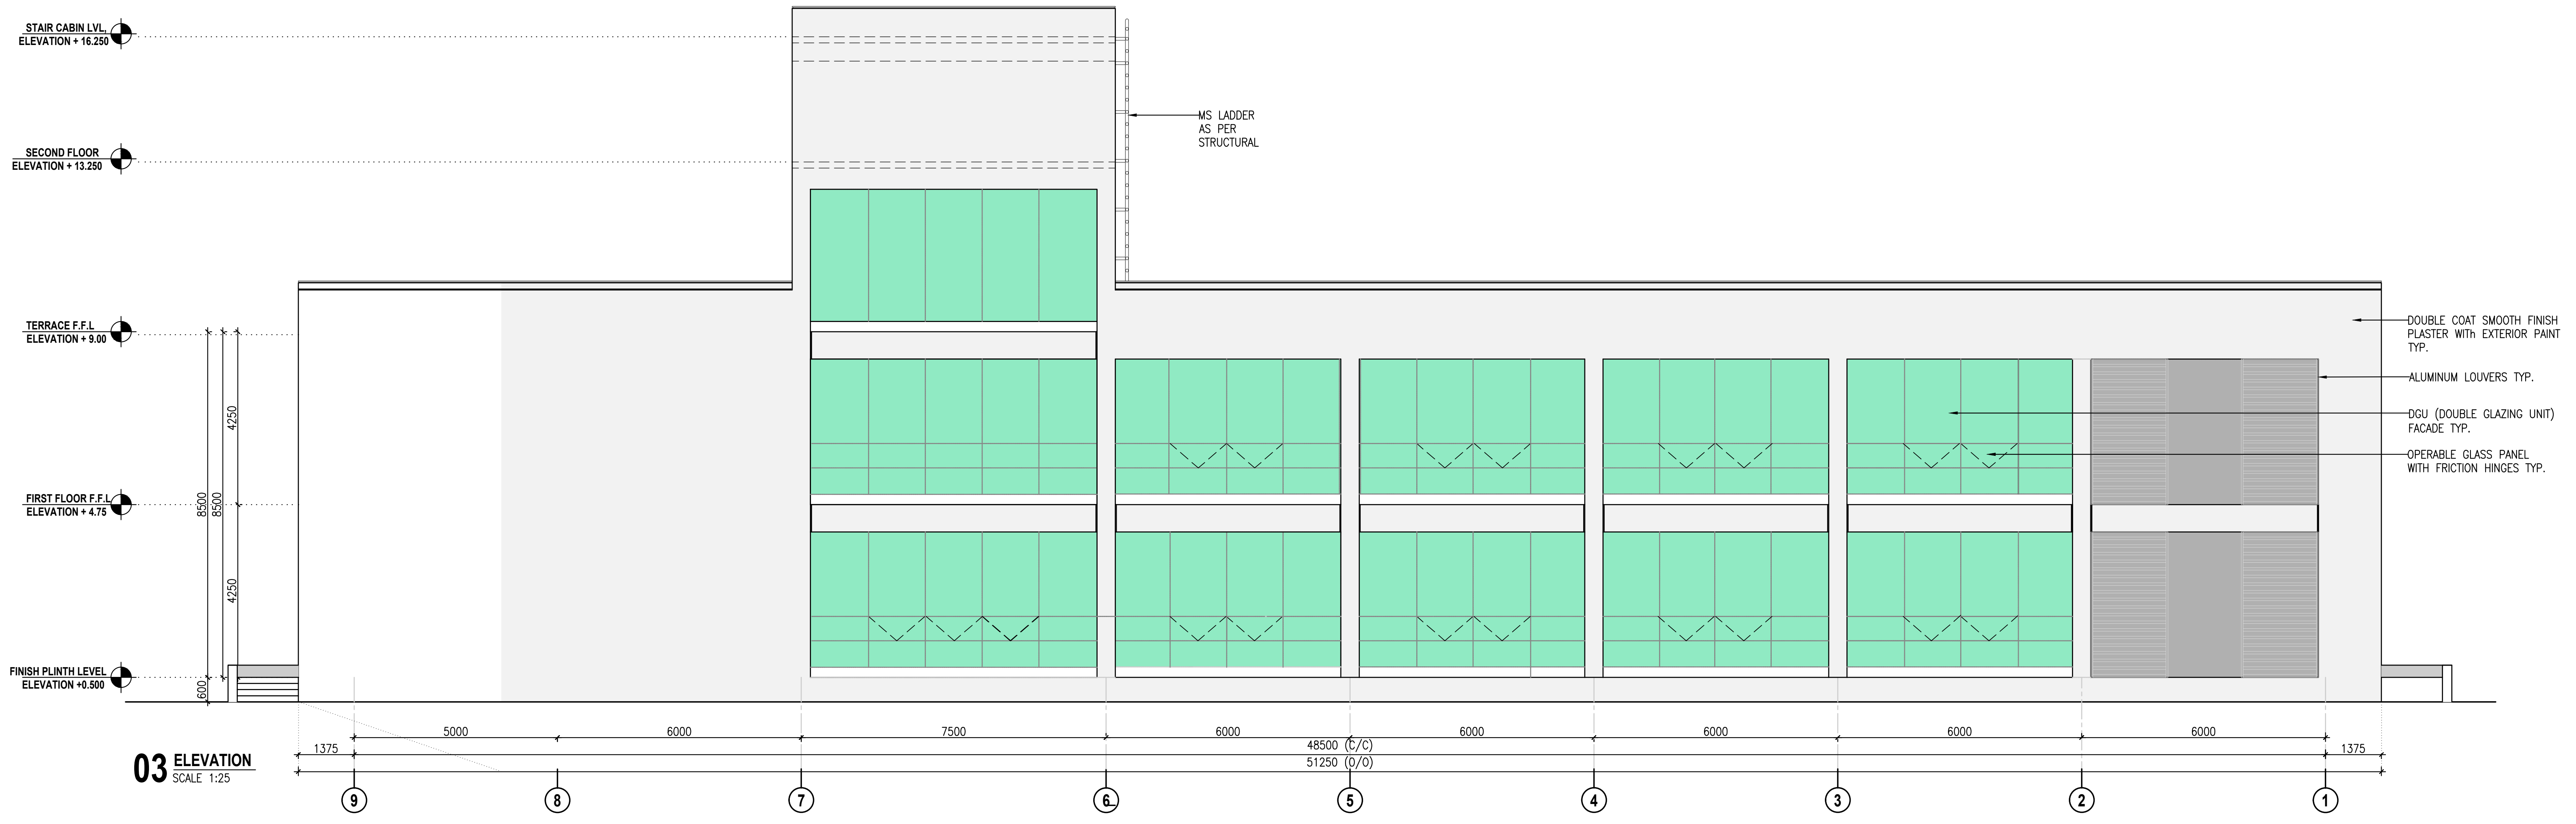

03 ELEVATION
SCALE 1:25

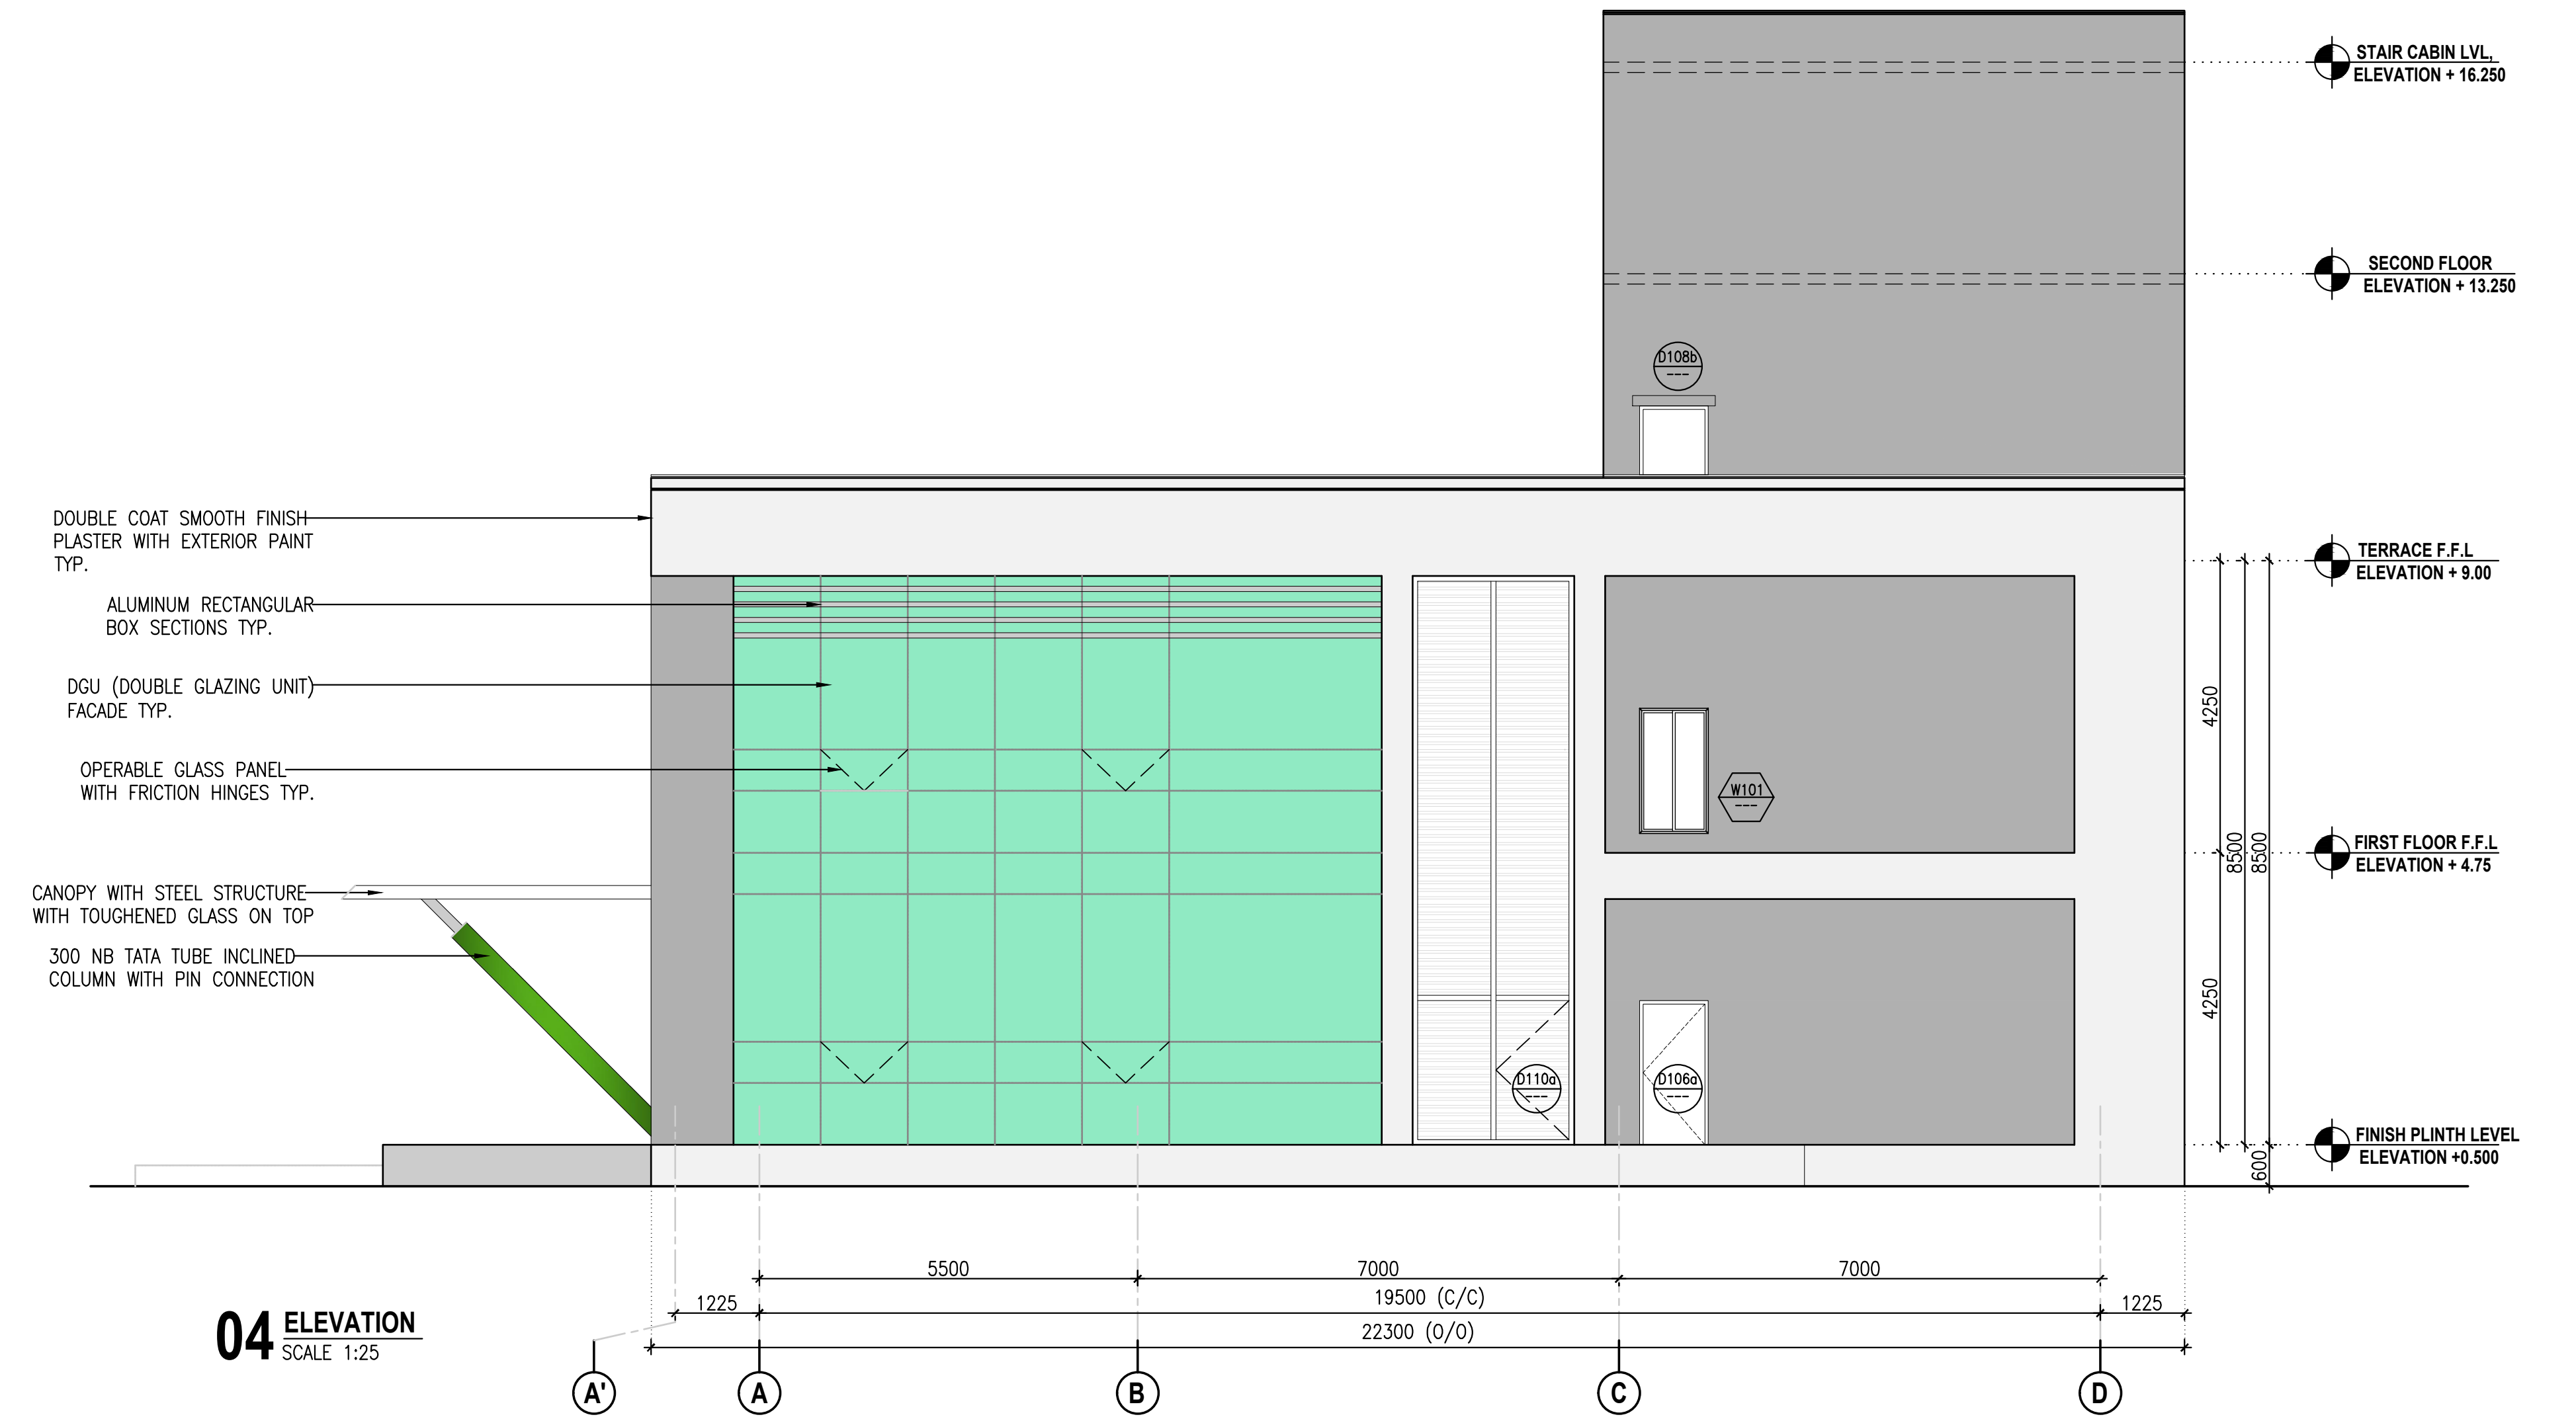
DOUBLE COAT SMOOTH FINISH PLASTER WITH EXTERIOR PAINT TYP.
ALUMINUM RECTANGULAR BOX SECTIONS TYP.
DGU (DOUBLE GLAZING UNIT) FACADE TYP.
OPERABLE GLASS PANEL WITH FRICTION HINGES TYP.
CANOPY WITH STEEL STRUCTURE WITH TOUGHENED GLASS ON TOP
300 NB TATA TUBE INCLINED COLUMN WITH PIN CONNECTION
D108b
W101
D110a
D106a
STAIR CABIN LVL,
ELEVATION + 16.250
SECOND FLOOR
ELEVATION + 13.250
TERRACE F.F.L
ELEVATION + 9.00
FIRST FLOOR F.F.L
ELEVATION + 4.75
FINISH PLINTH LEVEL
ELEVATION +0.500
4250
8500
8500
4250
600
5500
7000
7000
1225
19500 (C/C)
1225
22300 (O/O)
A'
A
B
C
D

04 ELEVATION
SCALE 1:25

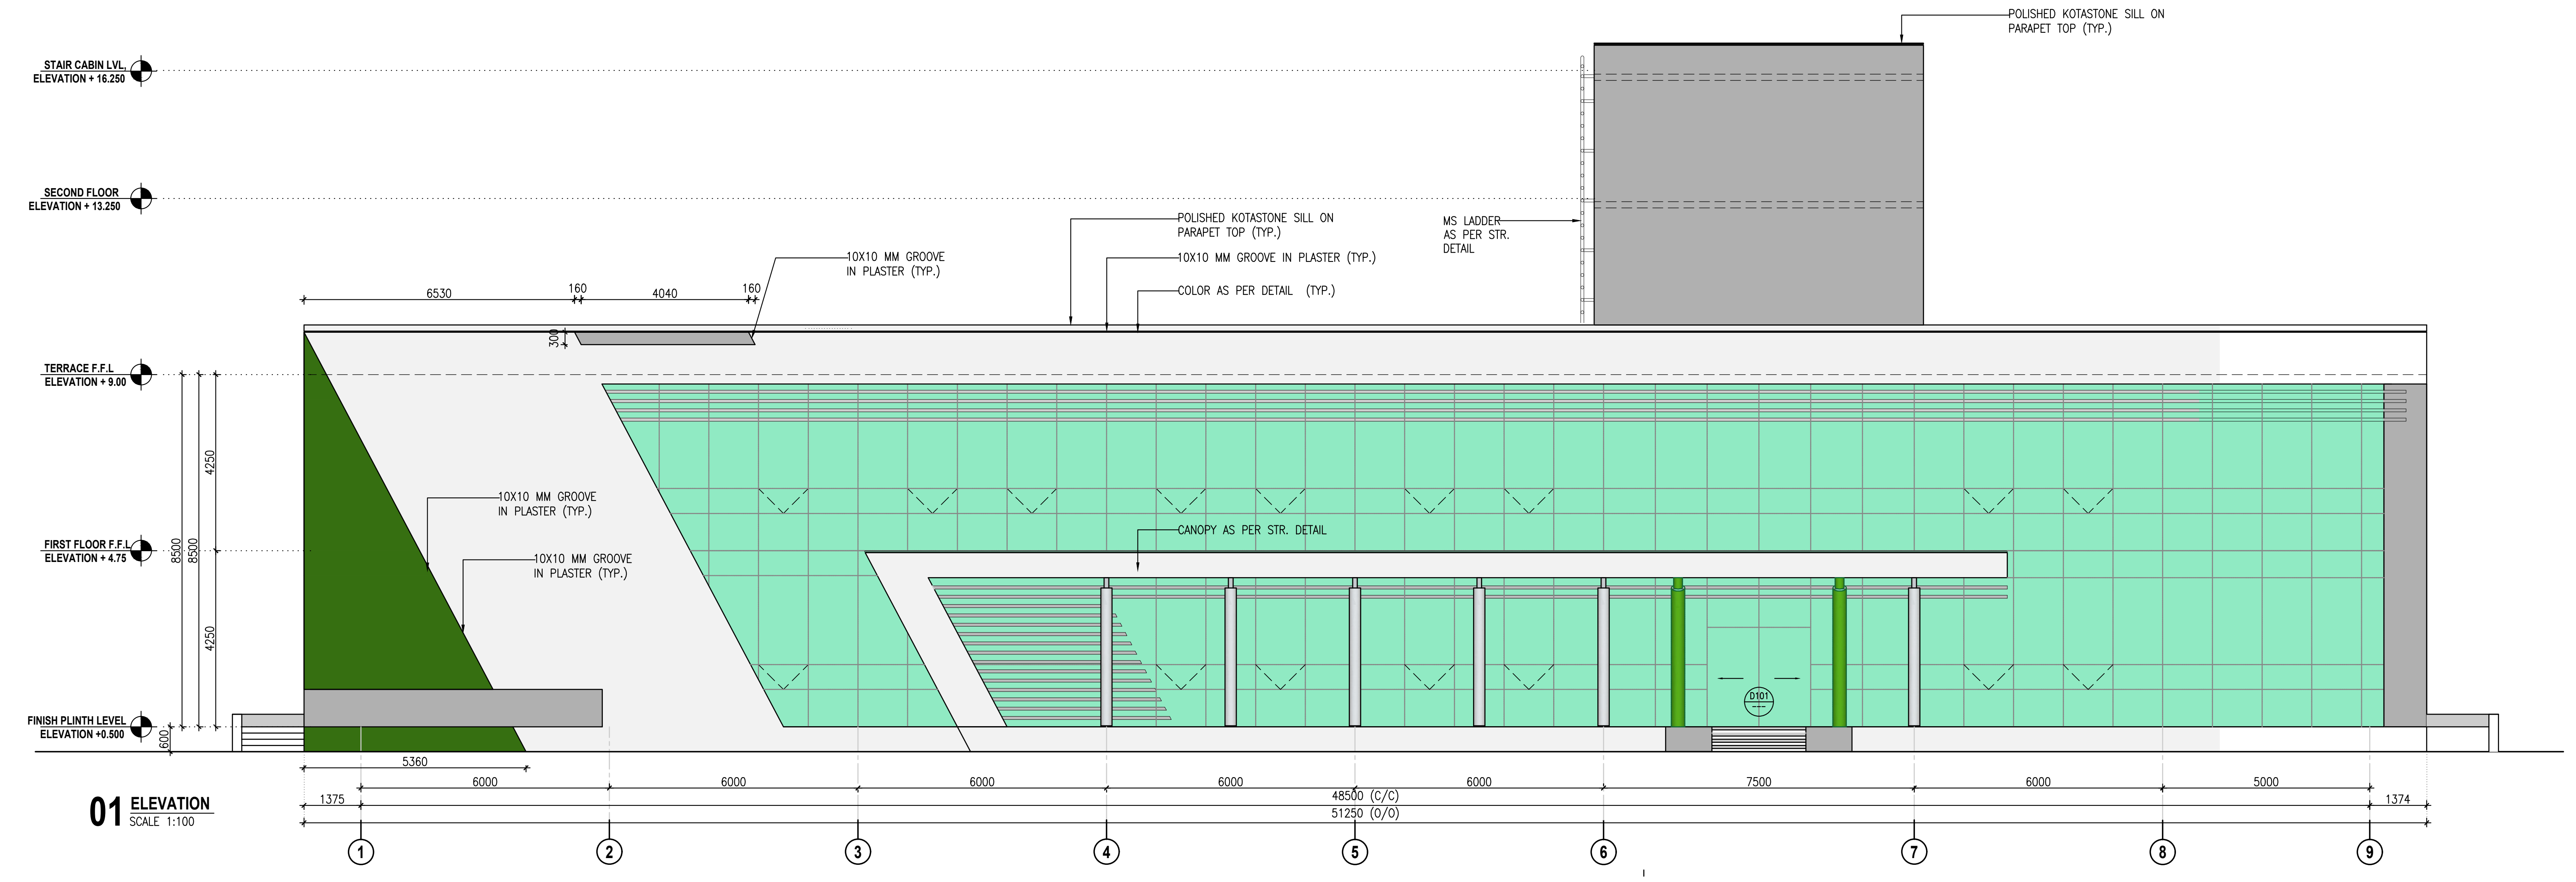

01 ELEVATION
SCALE 1:100

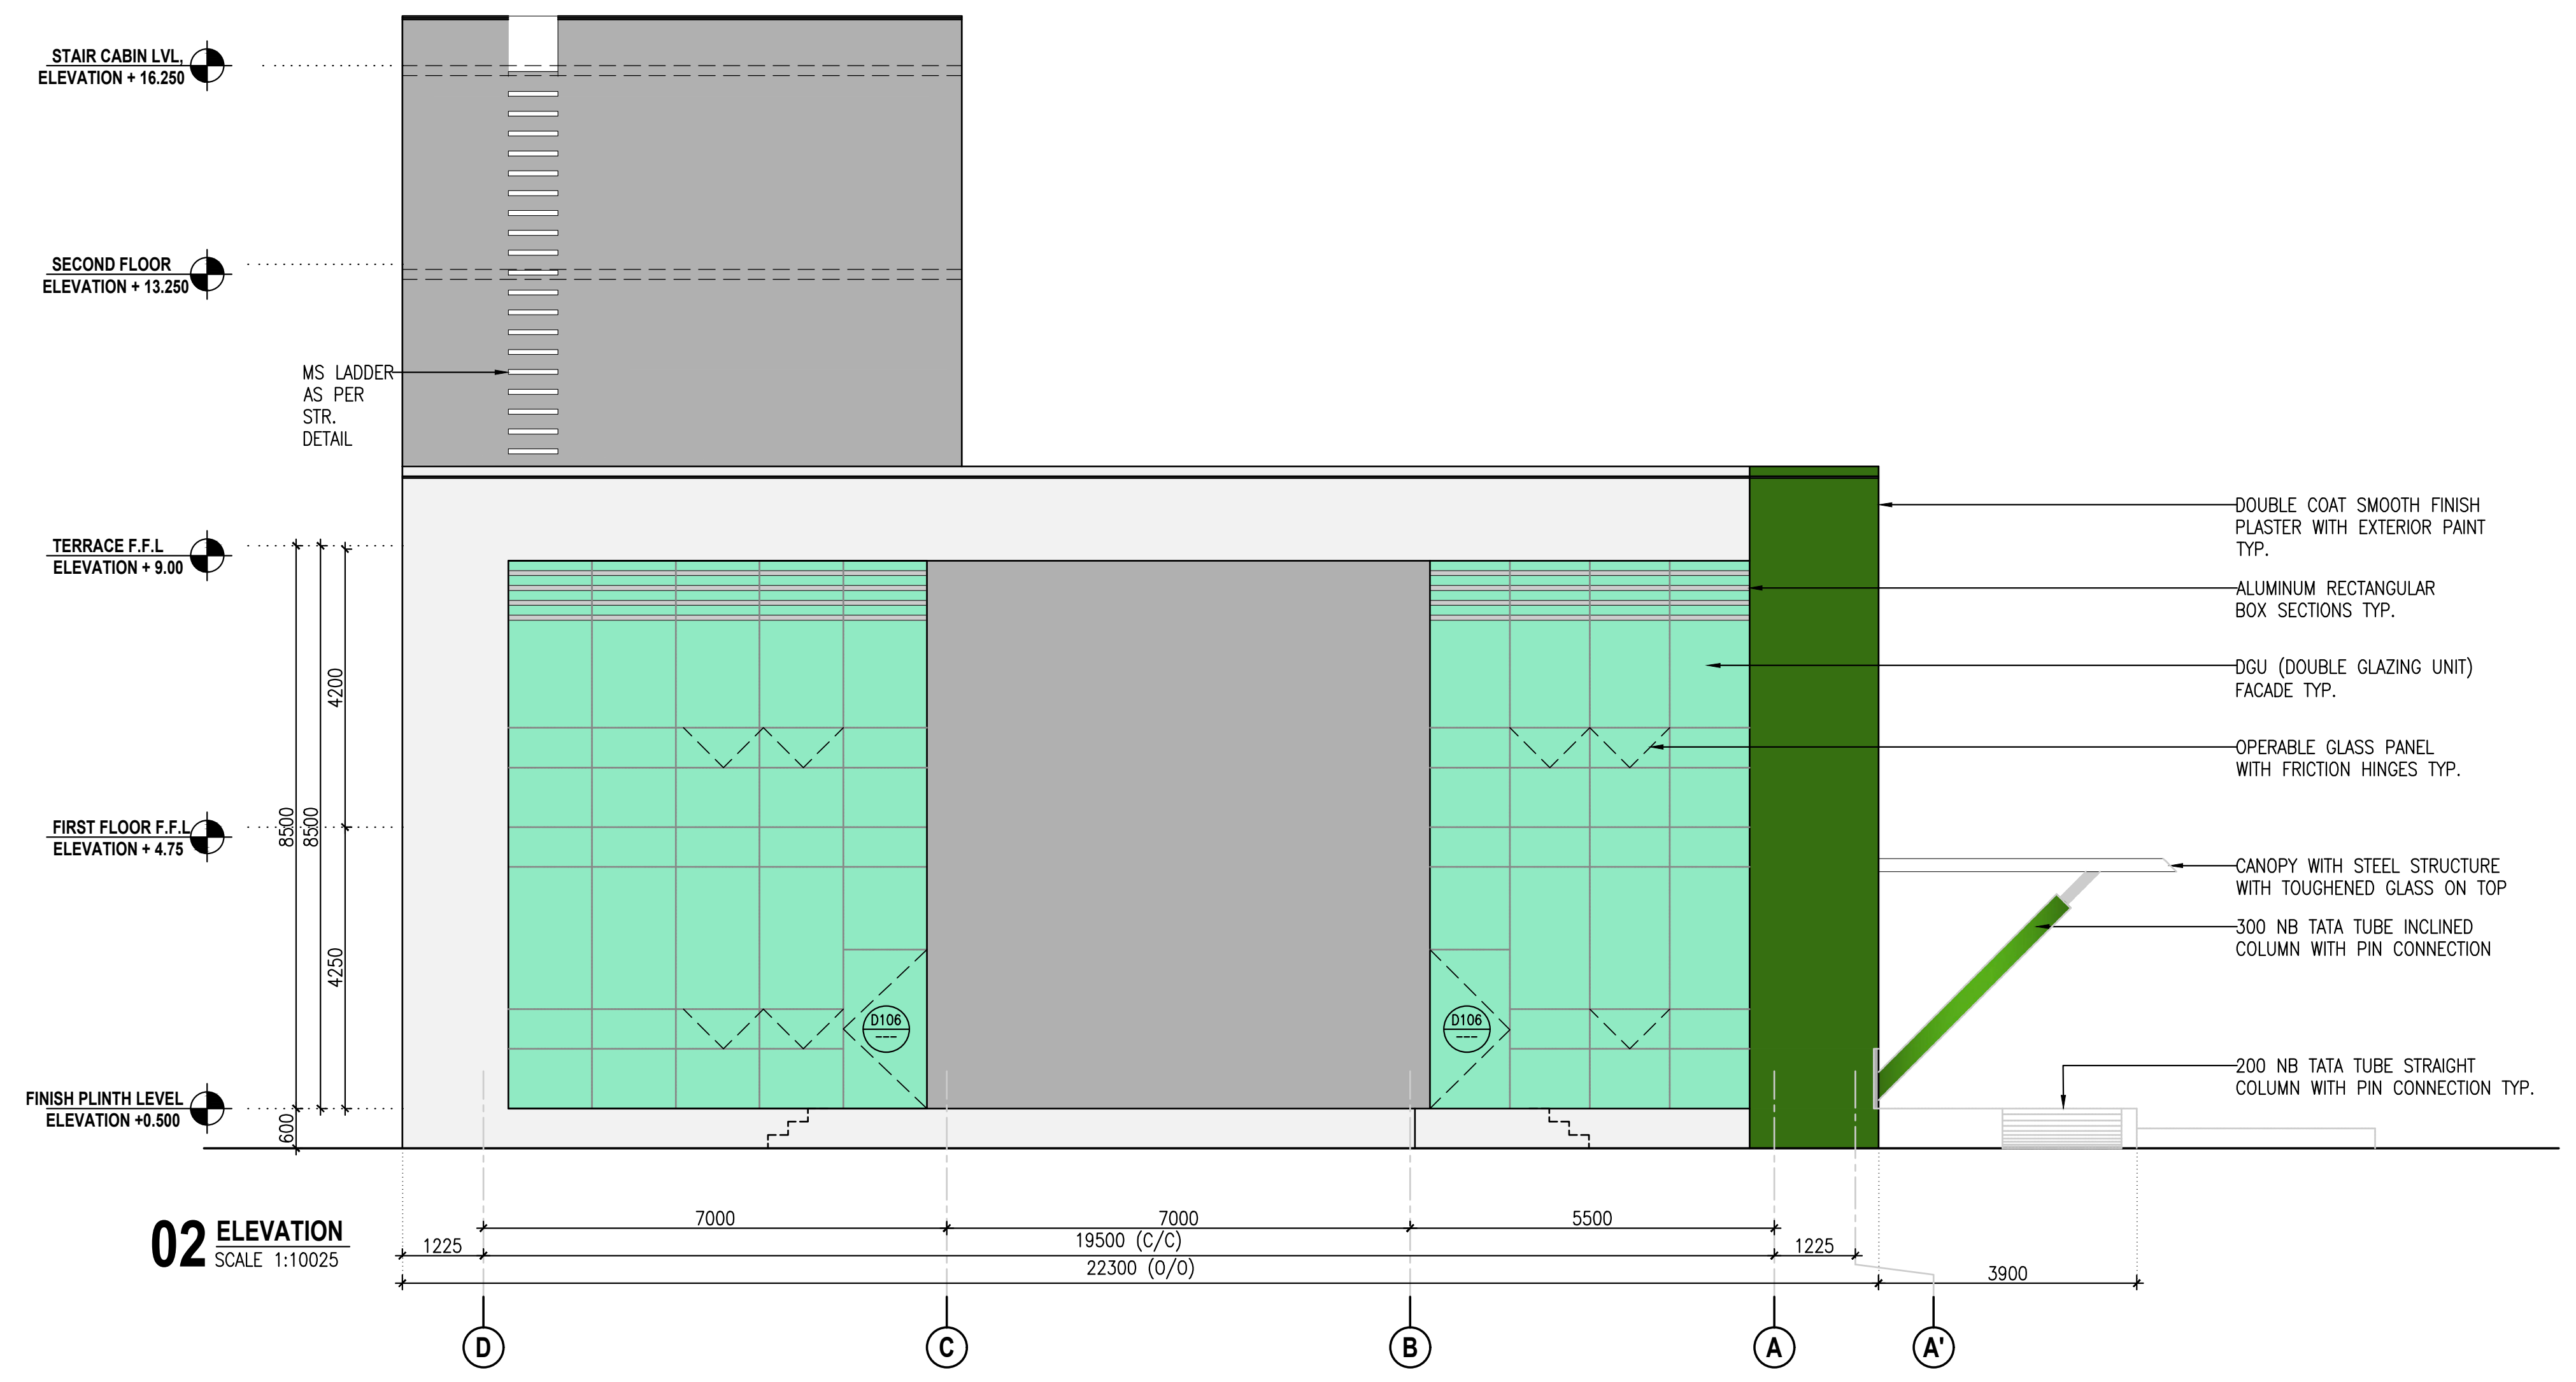
STAIR CABIN LVL,
ELEVATION + 16.250
SECOND FLOOR
ELEVATION + 13.250
MS LADDER AS PER STR. DETAIL
TERRACE F.F.L
ELEVATION + 9.00
FIRST FLOOR F.F.L
ELEVATION + 4.75
FINISH PLINTH LEVEL
ELEVATION +0.500
DOUBLE COAT SMOOTH FINISH PLASTER WITH EXTERIOR PAINT TYP.
ALUMINUM RECTANGULAR BOX SECTIONS TYP.
DGU (DOUBLE GLAZING UNIT) FACADE TYP.
OPERABLE GLASS PANEL WITH FRICTION HINGES TYP.
CANOPY WITH STEEL STRUCTURE WITH TOUGHENED GLASS ON TOP
300 NB TATA TUBE INCLINED COLUMN WITH PIN CONNECTION
200 NB TATA TUBE STRAIGHT COLUMN WITH PIN CONNECTION TYP.
D106
D106
4200
8500
8500
4250
600
1225
7000
7000
5500
1225
19500 (C/C)
22300 (O/O)
3900
D
C
B
A
A'

02 ELEVATION
SCALE 1:10025

IMPORTANT NOTE :

1. ± 0.000 LEVEL CORRESPONDS TO + 365.50 LEVEL

THIS DRAWING & DESIGN IS THE SOLE PROPERTY OF VMS & SHALL NOT BE COPIED,
TRACED OR REPRODUCED BY ANY MEANS WITHOUT PRIOR WRITTEN CONSENT OF THE FIRM.

GENERAL NOTES :

1. ALL THE DIMENSIONS ARE UNFINISHED DIMENSIONS.
2. ALL DIMENSIONS ARE IN MM AND LEVELS ARE IN MT, UNLESS OTHERWISE MENTIONED.
3. ALL THE DIMENSIONS SHALL BE READ & NOT TO BE MEASURED.
4. IN CASE OF ANY DISCREPANCY, BRING IT TO THE NOTICE OF THE ARCHITECT IMMEDIATELY.
5. DETAIL DRAWING PRECEDES THE GENERAL DRAWING

STANDARD DRAWING SYMBOLS:

+ FINISHED LEVEL
+ UNFINISHED LEVEL

01 --- SECTION SYMBOL
UPPER HALF INDICATES DIAGRAM NO. (NUMERICAL VALUE) IN DRAWING SHEET & LOWER HALF INDICATES DRAWING NO.

04 --- ELEVATION SYMBOL
UPPER HALF INDICATES DIAGRAM NO. IN DRAWING SHEET & LOWER HALF INDICATES DRAWING NO.

W100 A000 WINDOW SYMBOL
UPPER HALF INDICATES WINDOW NO. & LOWER HALF INDICATES DRAWING NO.

D100 A000 DOOR SYMBOL
UPPER HALF INDICATES DOOR NO. & LOWER HALF INDICATES DRAWING NO.

GRAPHIC LEGEND :

▨	230THK. FLY ASH BRICK WALL	☐	PUFF PANEL PARTITION
■	RCC COLUMN CUT IN PLAN.	▩	115THK. FLY ASH BRICK WALL 2.1MT. HT.

NOTE : FOR CIVIL CONTRACTORS

1. CIVIL CONTRACTOR–VENDOR NEEDS TO SUBMIT DETAILED SHOP DRAWINGS WITH NECESSARY JUNCTION & FIXING DETAILS FOR GLAZING, EXTERIOR CLADDING, GRILL–LOUVERS, PARTITIONS, FALSE CEILING, DOOR–WINDOWS, ETC. TO CLIENTS/ CONSULTANTS & GET IT APPROVED PRIOR TO THE EXECUTION.
2. BASED ON SCHEMATIC DRAWING PROVIDED BY CONSULTANT, CIVIL CONTRACTOR–VENDOR NEEDS TO PROVIDE DETAILED SHOP DRAWINGS OR ANY SPECIFIC SHOP DRAWINGS & SAMPLES ASK BY CLIENT/CONSULTANTS & GET IT APPROVED PRIOR TO THE EXECUTION.
3. NEED TO CONSIDER SUPPORTING PRIMARY & SECONDARY STRUCTURE FOR ABOVE MENTION ITEMS.

FOR TENDER

NO.	DATE	DESCRIPTION	DRAWN BY	CHECKED BY

REVISION HISTORY

KEY PLAN
SCALE : N.T.S.

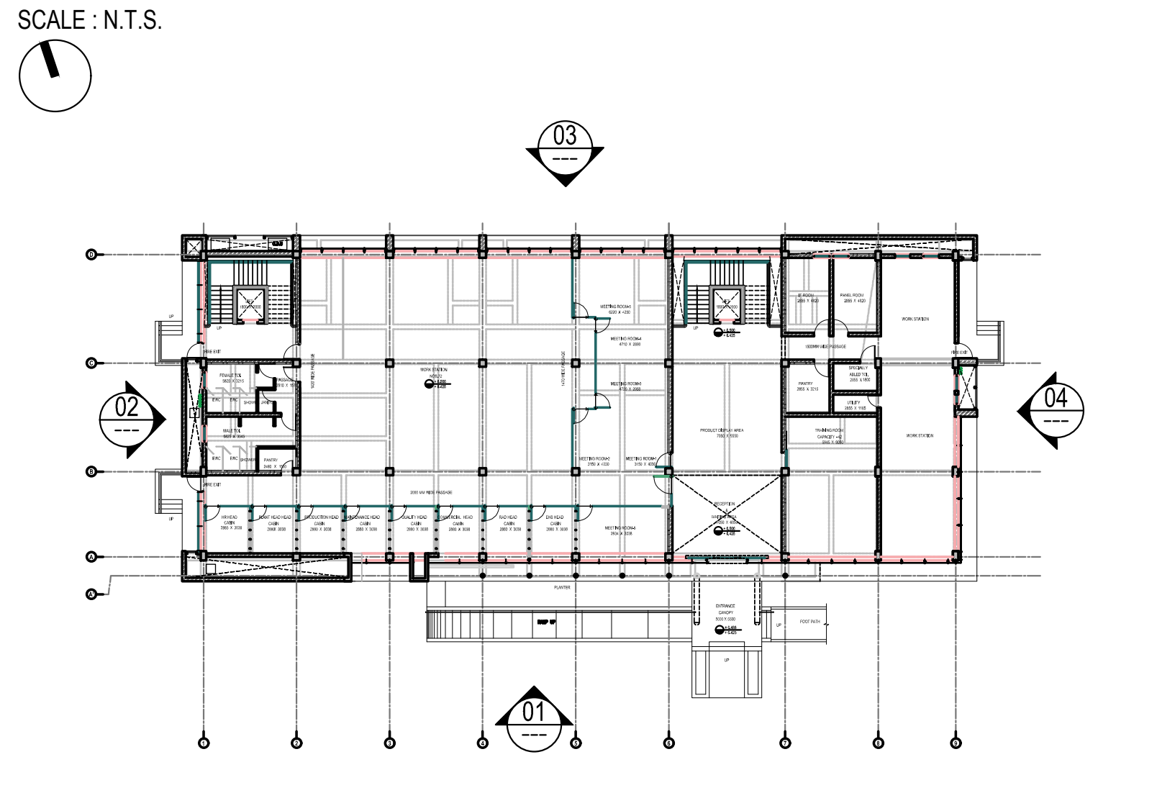

REFERENCE DRAWINGS :

01. ARCHITECTURAL : A.5.101, A.5.201, A.5.301
02. STRUCTURAL :
03. HVAC : -
04. ELECTRICAL : -
05. UTILITIES : -
-
-

ELEVATION
ADMIN BUILDING
AGRAWAL METAL WORKS(P) LTD.

PROJECT NO.	SCALE :	DRAWN :	NAMRATA
3824	AS NOTED	CHECKED:	DARSH
	DATE :	APPROVED:	DARSH
	02-12-2024	COORDINATION CHECKED:	DARSH

VMS
ENGINEERING + ARCHITECTURE

VMS ENGINEERING & DESIGN SERVICES (P) LTD.
CHITRAKOOT FLATS, B/H TIMES OF INDIA, OFF ASHRAM ROAD,
AHMEDABAD-380 009. PHONE: +91 (079) 2658-8829, 4023-6236
WWW.VMSCONSULTANTS.COM

SHEET SIZE	DRAWING NO.	TENDER	REVISION:
600x 1200	T.A.5.301	T	R0