
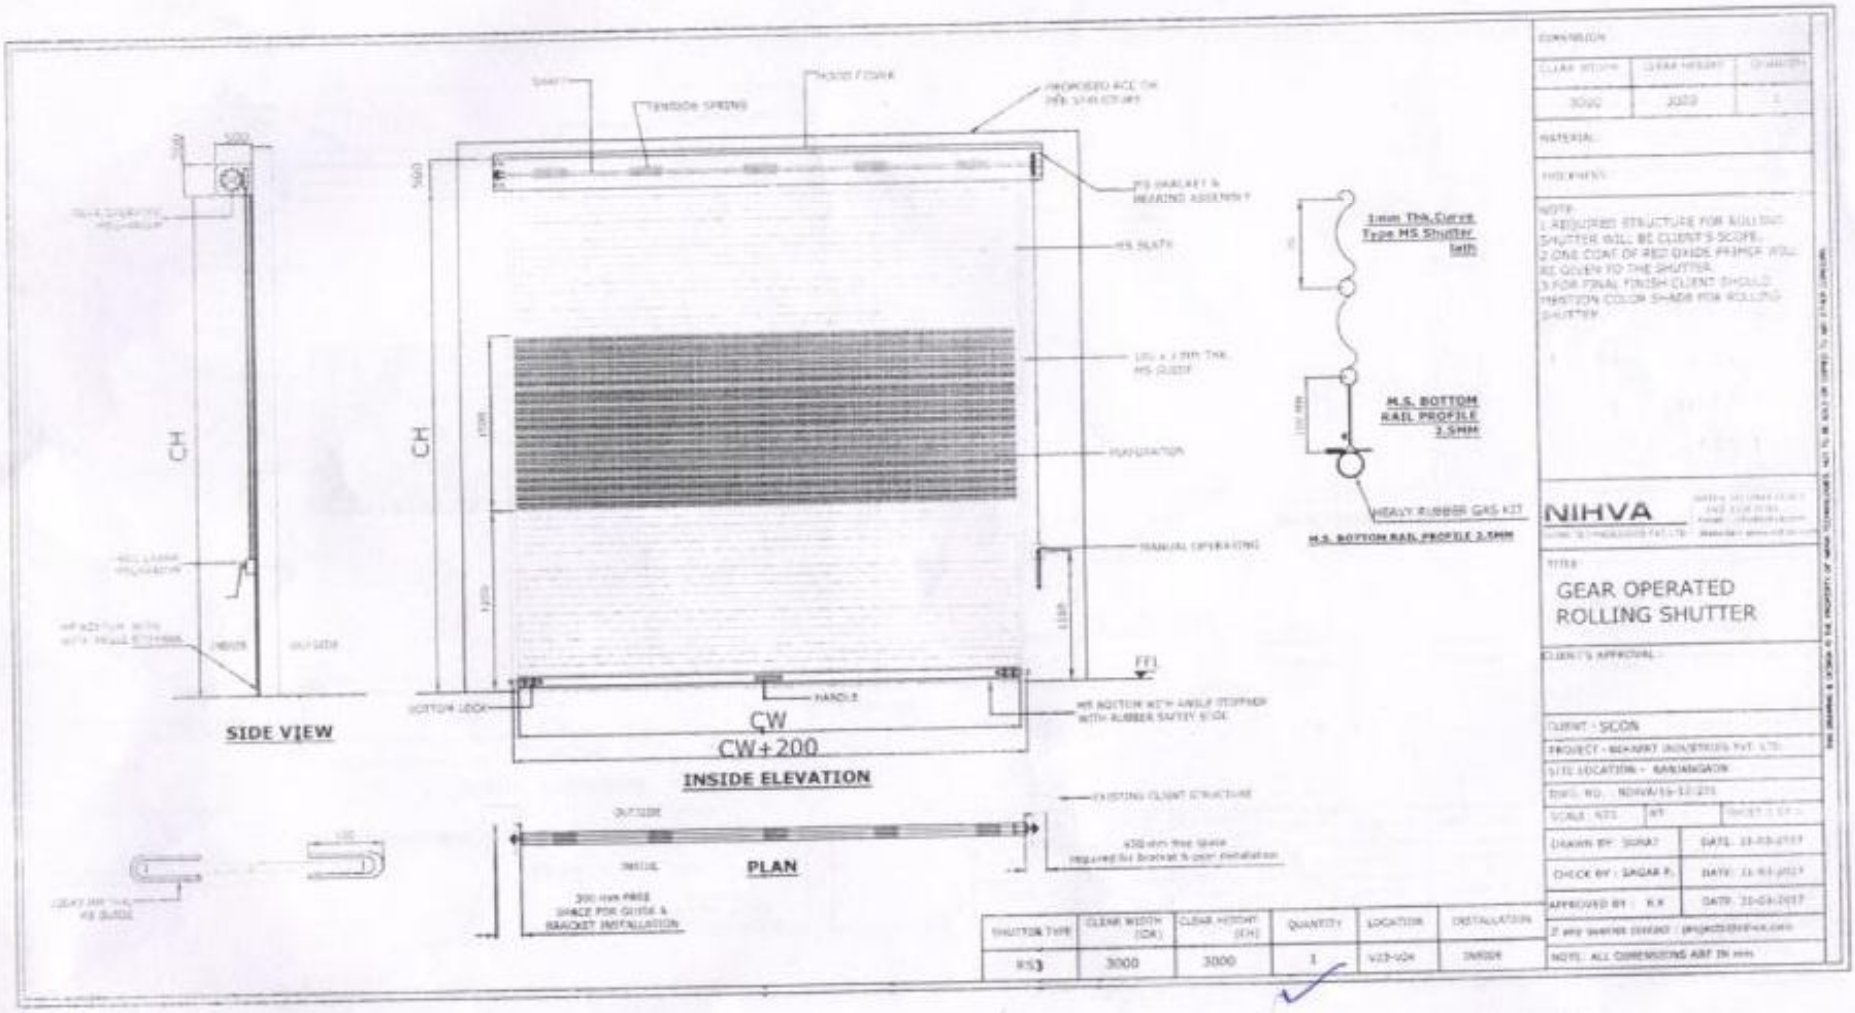


SHUTTER TYPE	CLEAR WIDTH (CW)	CLEAR HEIGHT (CH)	QUANTITY	LOCATION	INSTALLATION
RS3	3000	3000	1	V23-V24	INSIDE

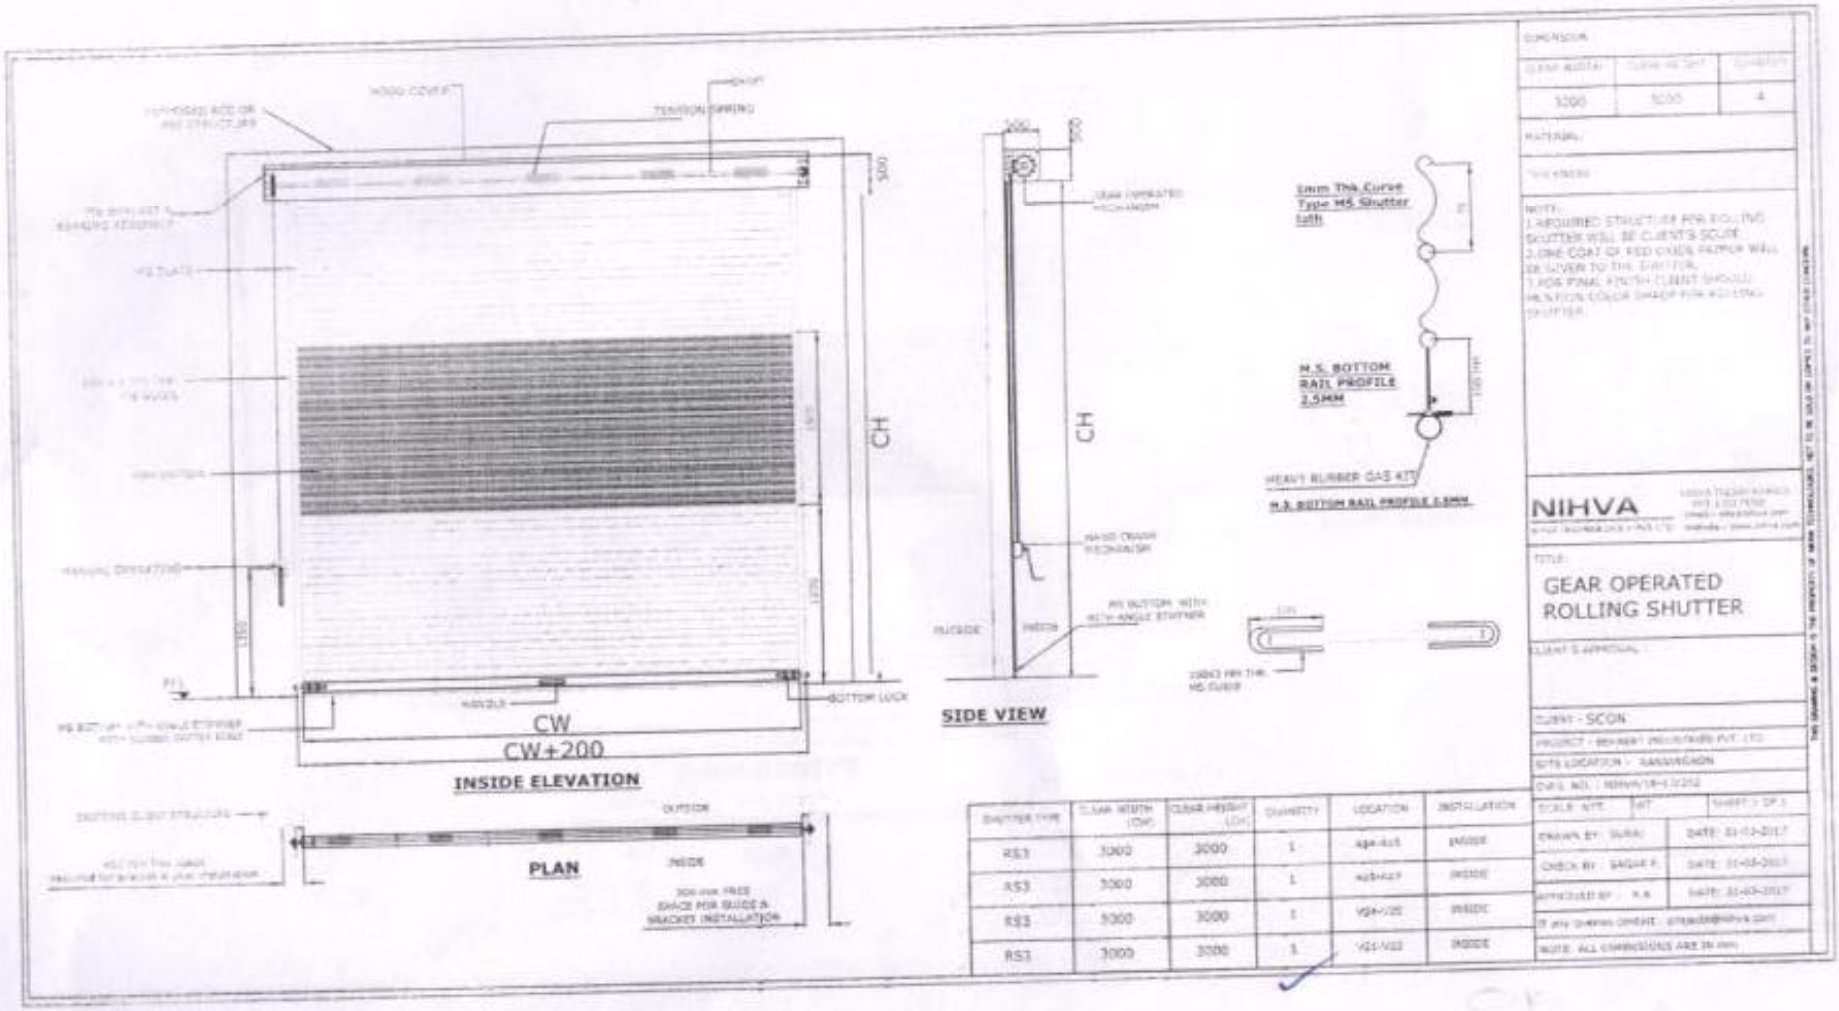

SHUTTER TYPE	CLEAR WIDTH (CW)	CLEAR HEIGHT (CH)	QUANTITY	LOCATION	INSTALLATION
RS3	3000	3000	1	[illegible]	[illegible]
RS3	3000	3000	1	[illegible]	[illegible]
RS3	3000	3000	1	[illegible]	[illegible]
RS3	3000	3000	1	[illegible]	[illegible]

DIMENSION		
CLEAR WIDTH	CLEAR HEIGHT	QUANTITY
3000	3000	4

MATERIAL:

THICKNESS:

NOTE:
1.REQUIRED STRUCTURE FOR ROLLING SHUTTER WILL BE CLIENT'S SCOPE.
2.ONE COAT OF RED OXIDE PAINT WILL BE GIVEN TO THE SHUTTER.
3.FOR FINAL FINISH CLIENT SHOULD MENTION COLOR SHADE FOR ROLLING SHUTTER.

NIHVA

TITLE:
GEAR OPERATED ROLLING SHUTTER

CLIENT'S APPROVAL :

CLIENT - SCON

PROJECT - [illegible]

SITE LOCATION - [illegible]

DWG. NO. : NIHVA/18-19/216


SCALE: NTS	QTY.	SHEET 1 OF 1
DRAWN BY : SURAJ		DATE: 31-03-2017
CHECK BY : SAGAR P.		DATE: 31-03-2017
APPROVED BY : N.K.		DATE: 31-03-2017

If any changes consult : [illegible]

NOTE: ALL DIMENSIONS ARE IN mm


THE DRAWING & DESIGN IS THE PROPERTY OF NIHVA TECHNOLOGIES PVT. LTD. & NOT TO BE USED OR COPIED TO ANY OTHER PERSON

10/04/17
BIR

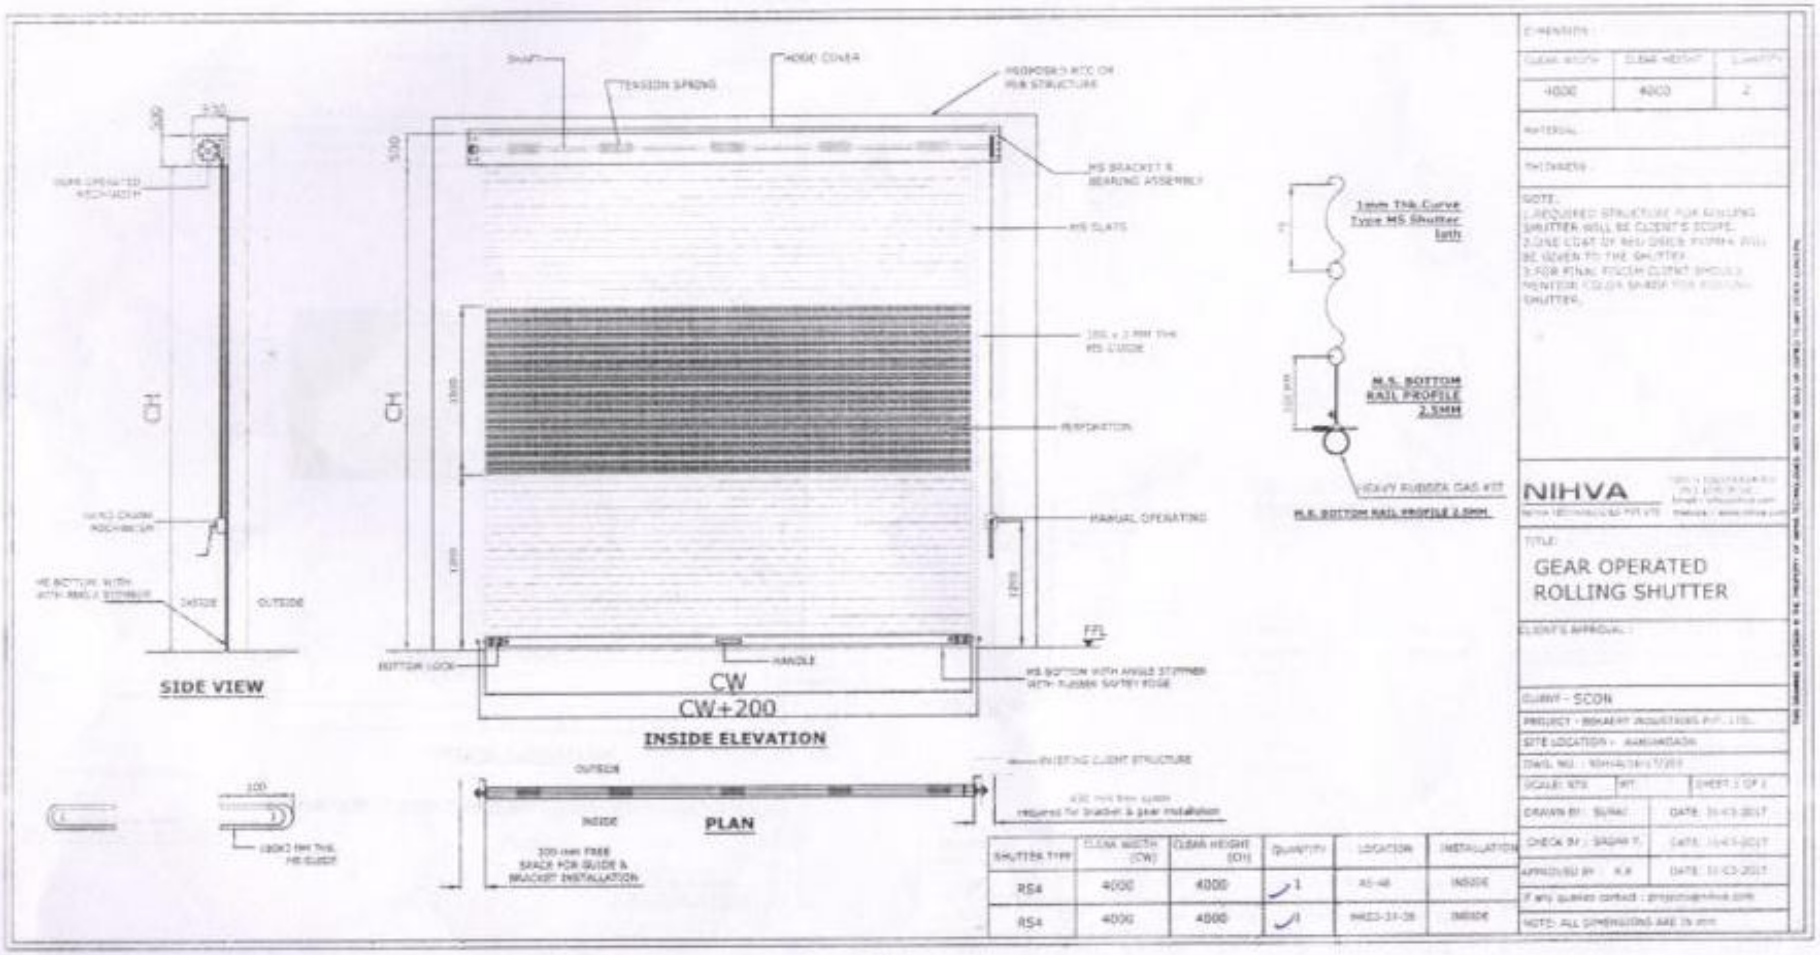

SHUTTER TYPE	CLEAR WIDTH (CW)	CLEAR HEIGHT (CH)	QUANTITY	LOCATION	INSTALLATION
RS4	4000	4000	1	AS-48	INSIDE
RS4	4000	4000	1	AHD-31-38	INSIDE

10/04/2017
BJ/c

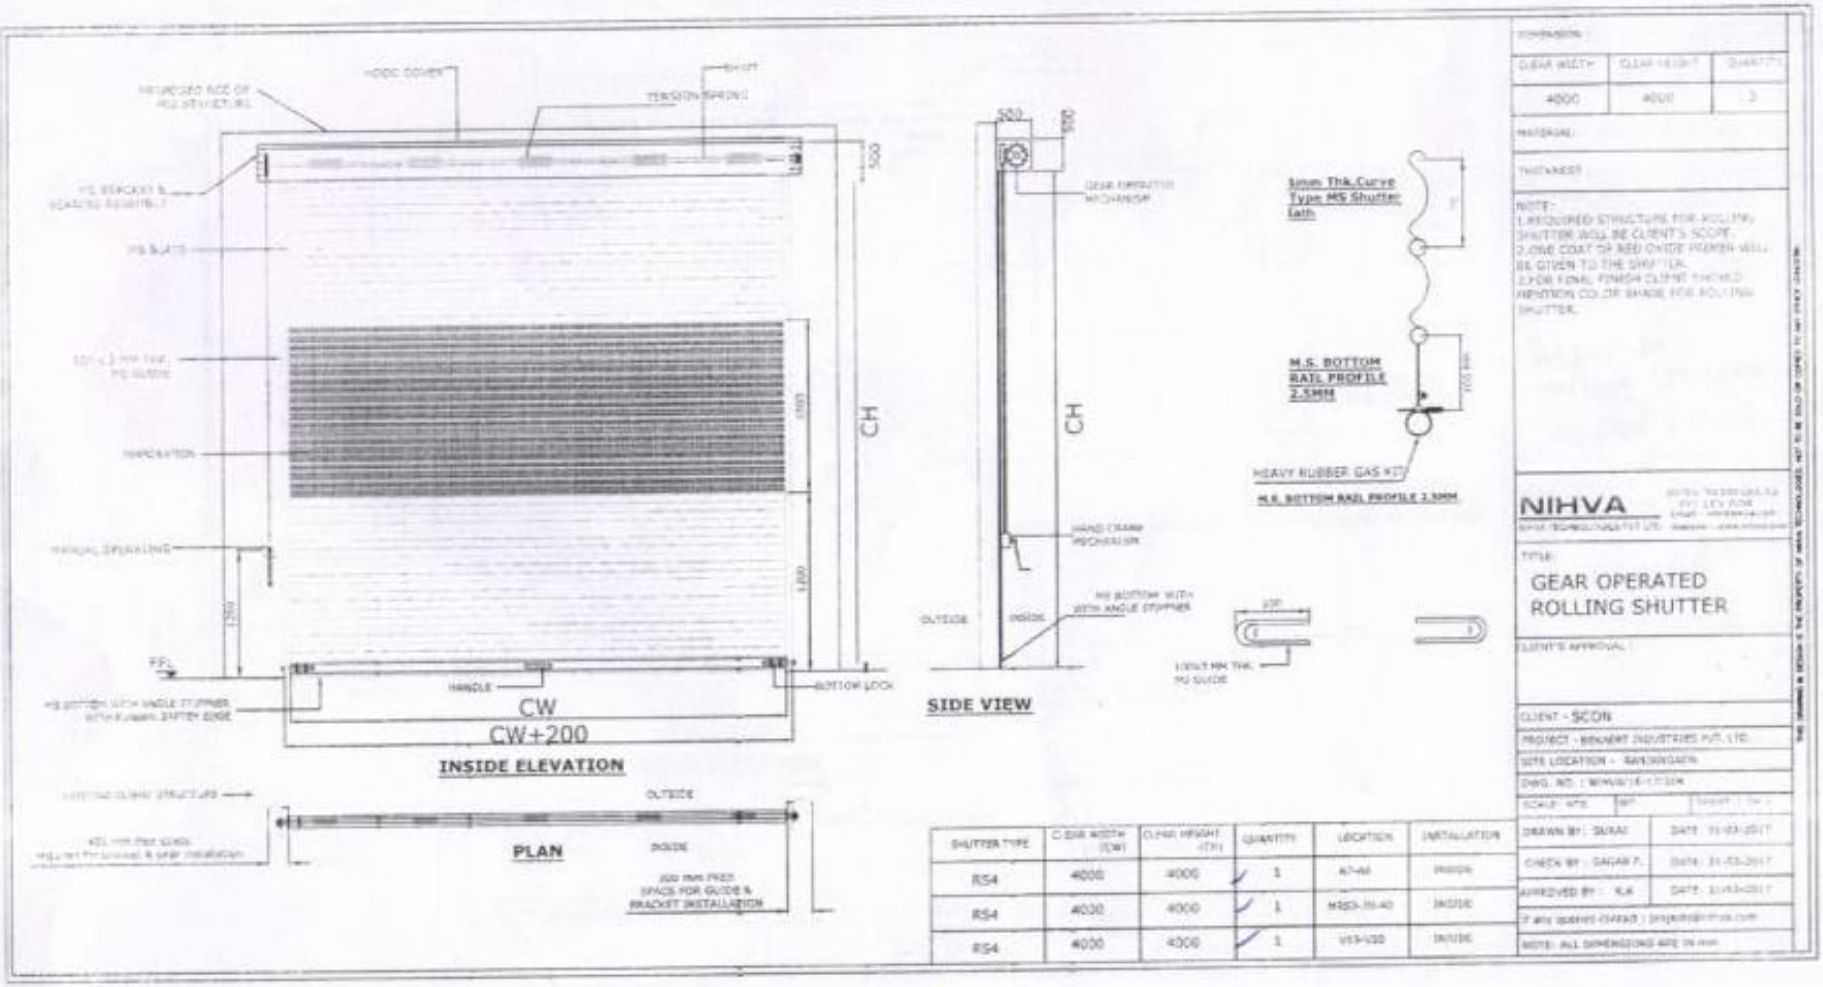


CLEAR WIDTH	CLEAR HEIGHT	QUANTITY
4000	4000	3

NOTE :-
1.RECOURED STRUCTURE FOR ROLLING SHUTTER WILL BE CLIENT'S SCOPE.
2.ONE COAT OF RED OXIDE PRIMER WILL BE GIVEN TO THE SHUTTER.
3.FOR FINAL FINISH CLIENT SHOULD MENTION COLOR SHADE FOR ROLLING SHUTTER.

SHUTTER TYPE	CLEAR WIDTH (CW)	CLEAR HEIGHT (CH)	QUANTITY	LOCATION	INSTALLATION
RS4	4000	4000	1	A7-A8	INSIDE
RS4	4000	4000	1	M3D3-M4D	INSIDE
RS4	4000	4000	1	V3-V2D	INSIDE

DRAWN BY : SURAJ
CHECK BY : SAGAR P.
APPROVED BY : K.K

10/04/2017
8 Pc

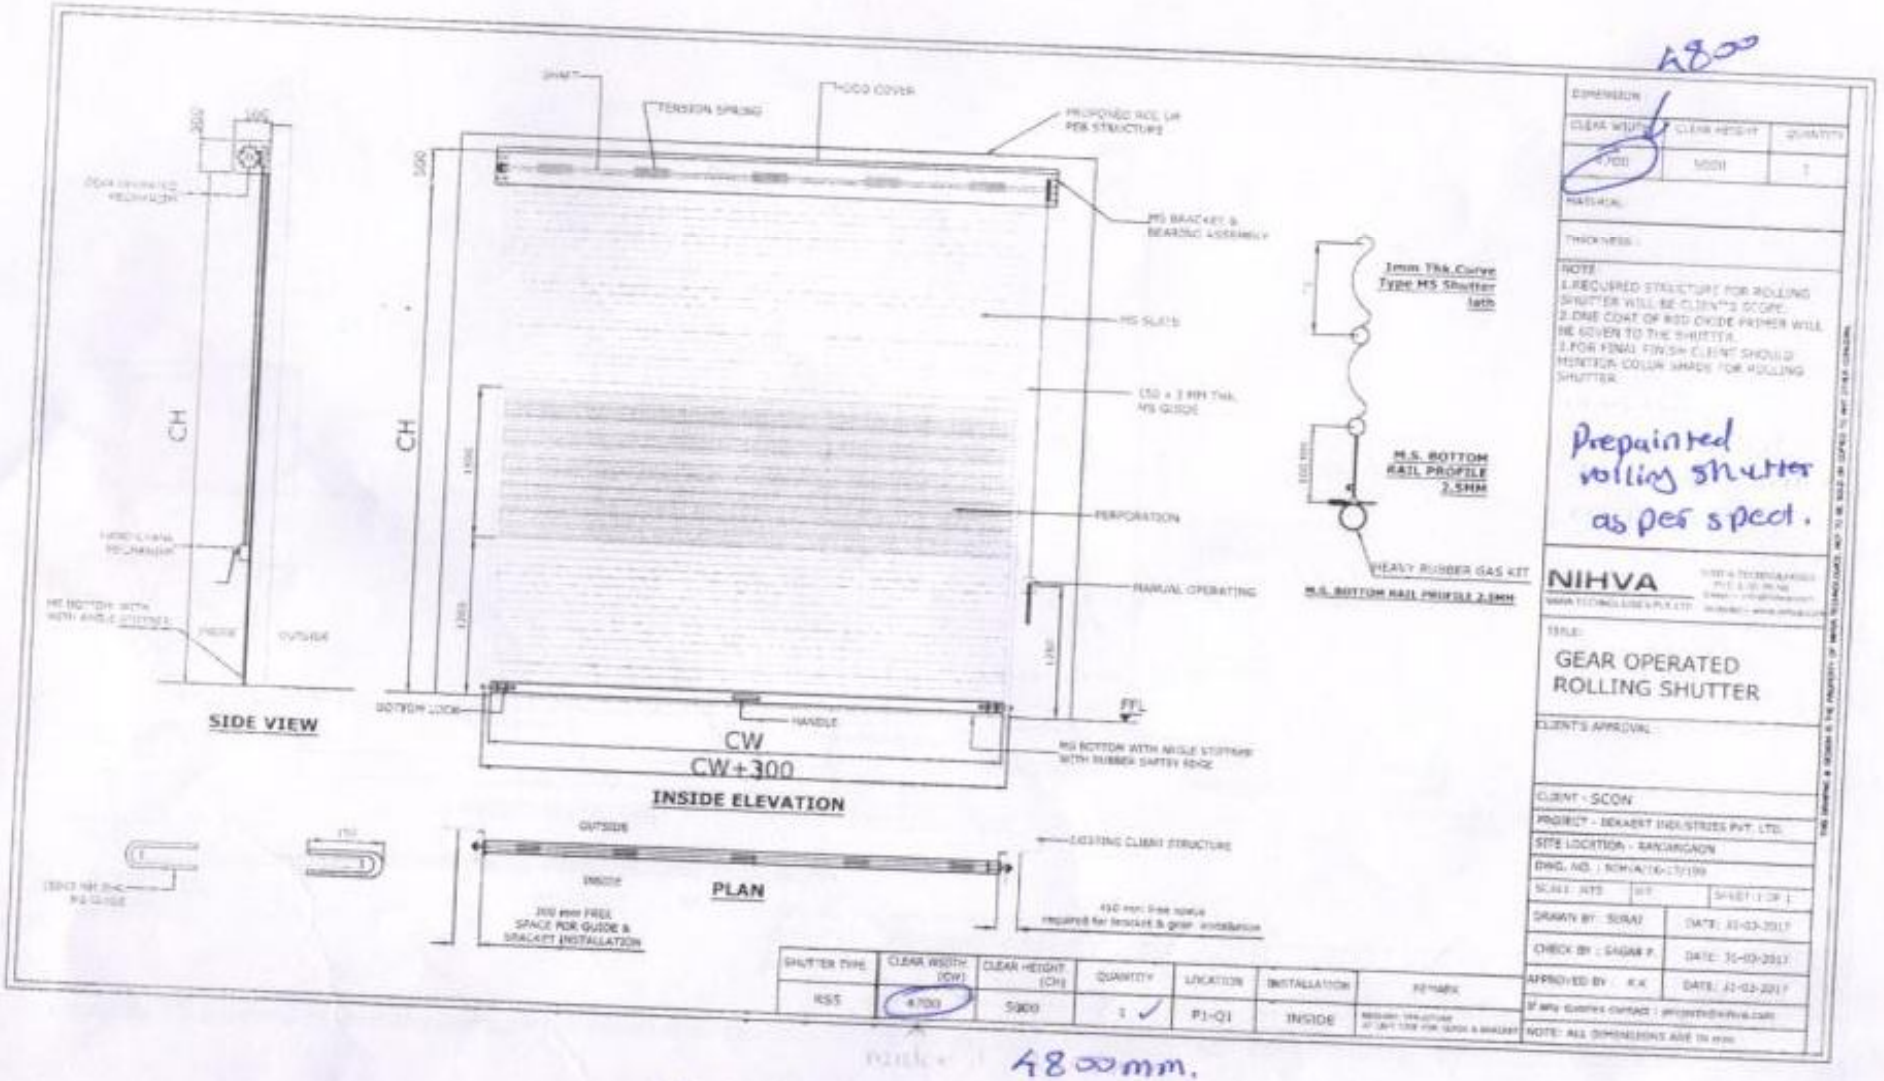

SHUTTER TYPE	CLEAR WIDTH (CW)	CLEAR HEIGHT (CH)	QUANTITY	LOCATION	INSTALLATION	REMARK
RSS	4700	5000	1	P1-Q1	INSIDE	

DIMENSION

CLEAR WIDTH	CLEAR HEIGHT	QUANTITY
4700	5000	1

MATERIAL :

THICKNESS :

NOTE
1.RECUIRED STRUCTURE FOR ROLLING SHUTTER WILL BE CLIENT'S SCOPE.
2.ONE COAT OF RED OXIDE PRIMER WILL BE GIVEN TO THE SHUTTER.
3.FOR FINAL FINISH CLIENT SHOULD MENTION COLOR SHADE FOR ROLLING SHUTTER.

Prepainted rolling shutter as per spect.

NIHVA

TITLE:
GEAR OPERATED ROLLING SHUTTER

CLIENT'S APPROVAL :


CLIENT - SCON
PROJECT - BEKAERT INDUSTRIES PVT. LTD.
SITE LOCATION - RANGARGAON
DWG. NO. : NIH/ATG-170199
SCALE : NTS
SHEET 1 OF 1
DRAWN BY : SURAJ DATE: 31-03-2017
CHECK BY : SAGAR P. DATE: 31-03-2017
APPROVED BY : K.K. DATE: 31-03-2017
NOTE: ALL DIMENSIONS ARE IN mm

4800

4800mm.

10/04/2017

BJPL

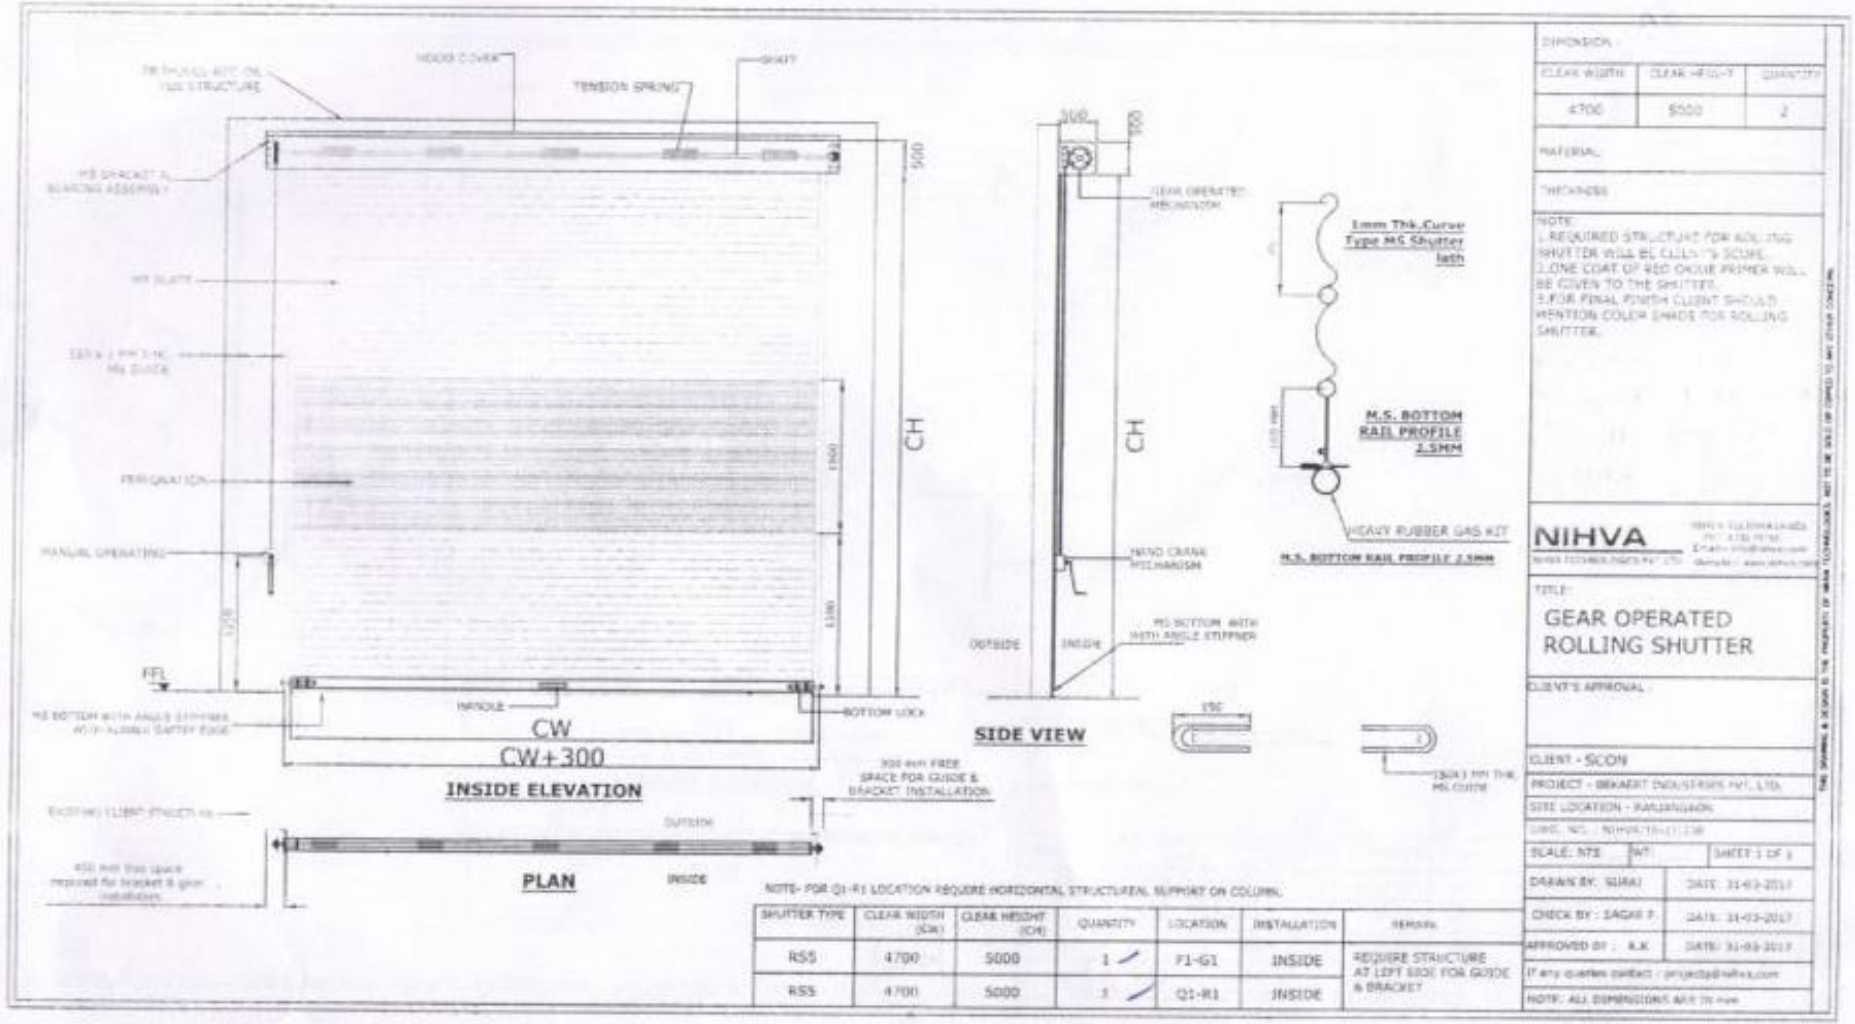

DIMENSION

CLEAR WIDTH	CLEAR HEIGHT	QUANTITY
4700	5000	2

MATERIAL

THICKNESS

NOTE:
1. REQUIRED STRUCTURE FOR ROLLING SHUTTER WILL BE CLIENT'S SCOPE.
2. ONE COAT OF RED OXIDE PRIMER WILL BE GIVEN TO THE SHUTTER.
3. FOR FINAL FINISH CLIENT SHOULD MENTION COLOR SHADE FOR ROLLING SHUTTER.

NIHVA

TITLE:
GEAR OPERATED ROLLING SHUTTER

CLIENT'S APPROVAL :

CLIENT - SCON

PROJECT - BEKAERT INDUSTRIES PVT. LTD.

SITE LOCATION - RANJANGAON

SCALE: NTS | WT. | SHEET 1 OF 1

DRAWN BY: SURAJ | DATE: 31-03-2017

CHECK BY : SAGAR P. | DATE: 31-03-2017

APPROVED BY : A.K. | DATE: 31-03-2017

If any queries contact : projects@nihva.com


NOTE: ALL DIMENSIONS ARE IN mm

NOTE- FOR Q1-R1 LOCATION REQUIRE HORIZONTAL STRUCTUREAL SUPPORT ON COLUMN.

SHUTTER TYPE	CLEAR WIDTH (CW)	CLEAR HEIGHT (CH)	QUANTITY	LOCATION	INSTALLATION	REMARK
RSS	4700	5000	1	F1-G1	INSIDE	REQUIRE STRUCTURE AT LEFT SIDE FOR GUIDE & BRACKET
RSS	4700	5000	1	Q1-R1	INSIDE	


Suraj
10/04/2017
BZPC

Sonwane

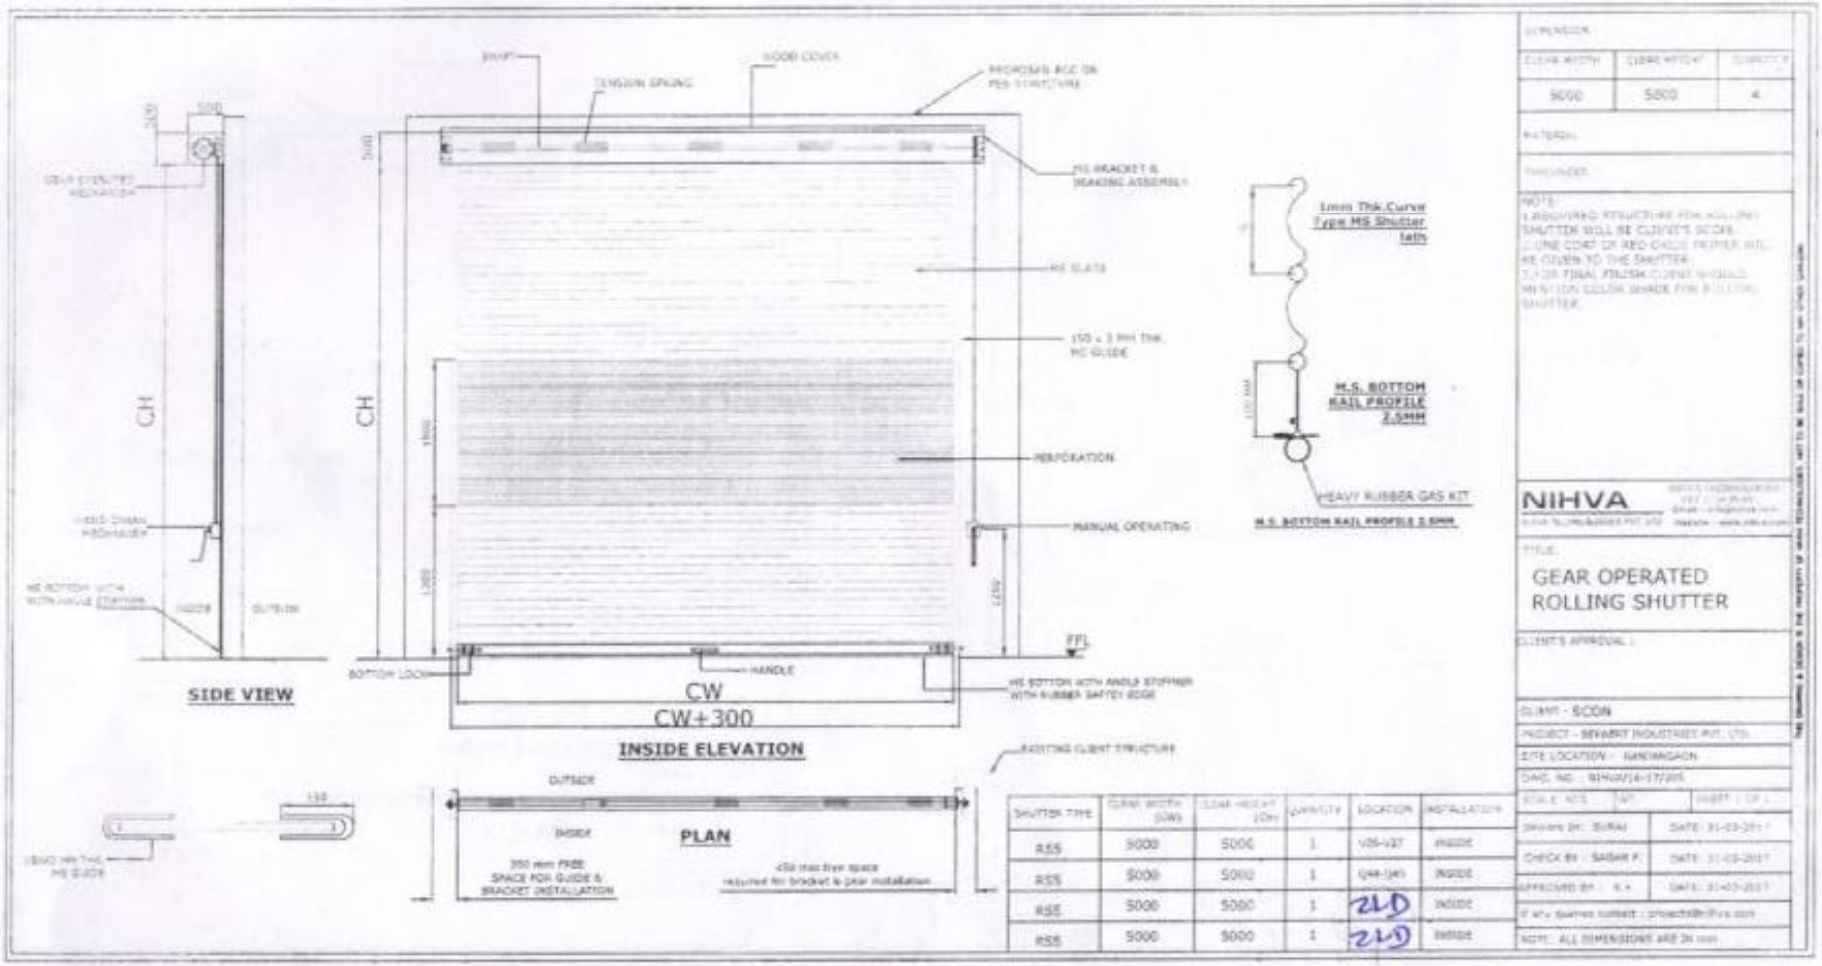


SHUTTER TYPE	CLEAR WIDTH (CW)	CLEAR HEIGHT (CH)	QUANTITY	LOCATION	INSTALLATION
RSS	5000	5000	1	GF-1F	INSIDE
RSS	5000	5000	1	GF-1F	INSIDE
RSS	5000	5000	1	2ND	INSIDE
RSS	5000	5000	1	2ND	INSIDE

10/04/2017
BIPL

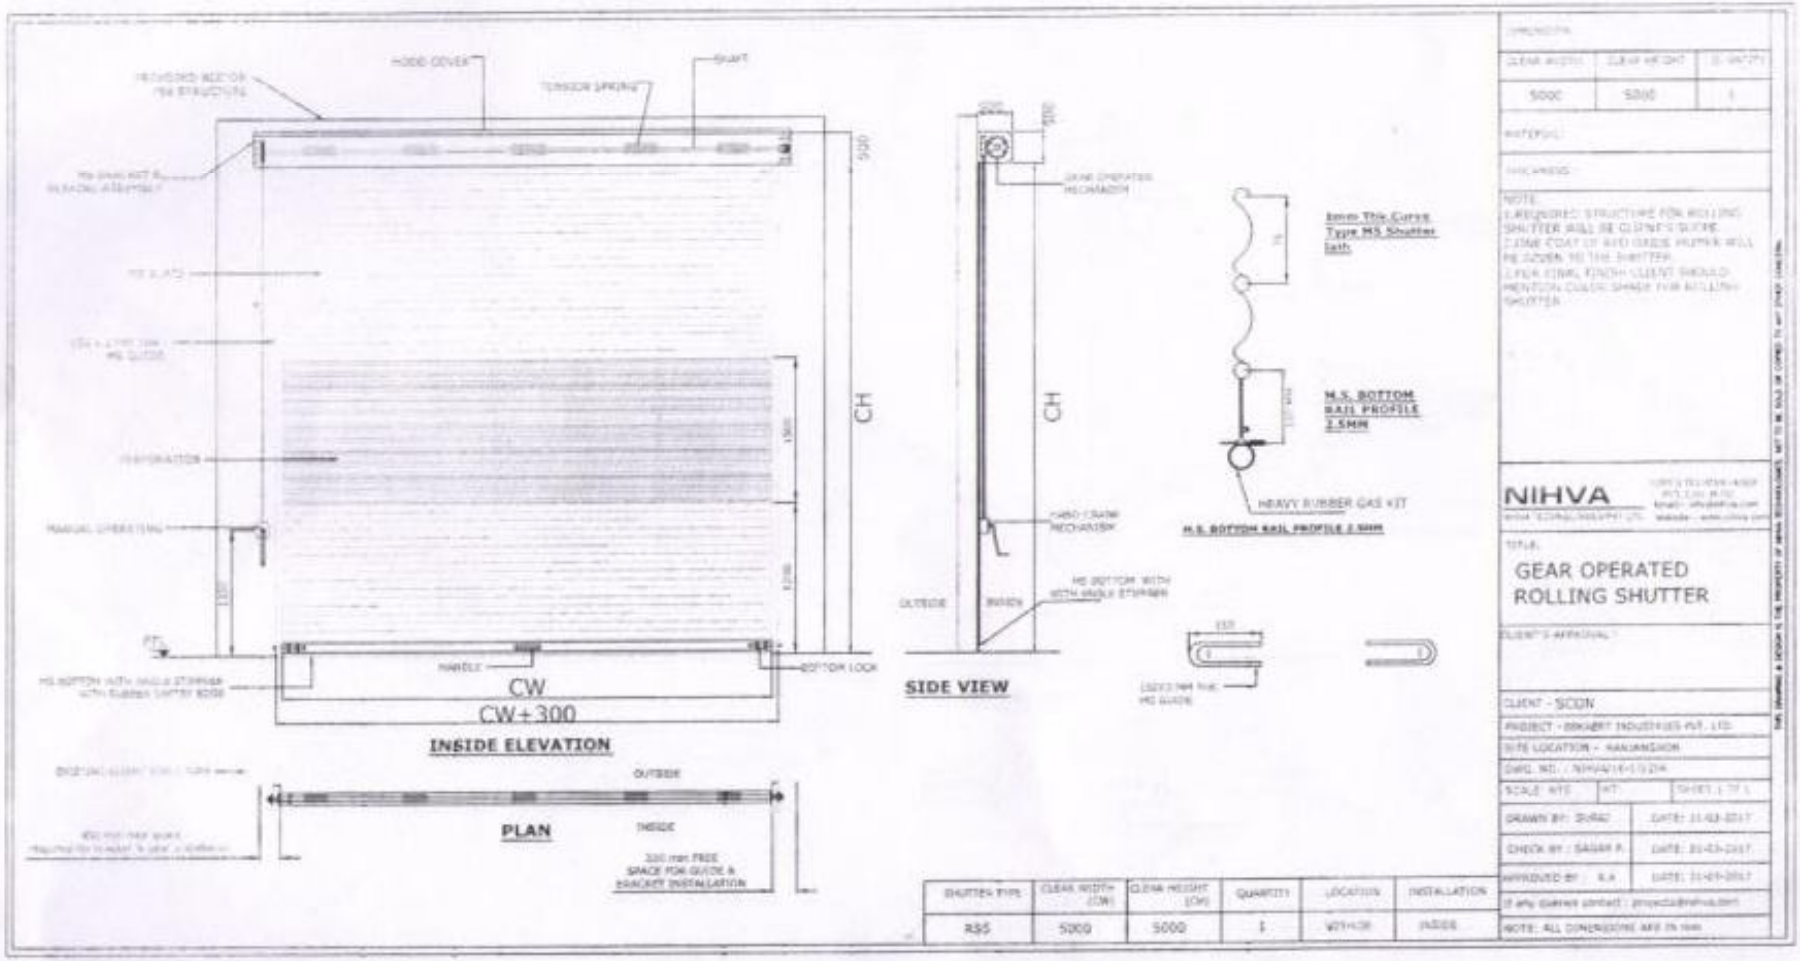

SHUTTER TYPE	CLEAR WIDTH (CW)	CLEAR HEIGHT (CH)	QUANTITY	LOCATION	INSTALLATION
RSS	5000	5000	1	WITHIN	INSIDE

10/04/2017

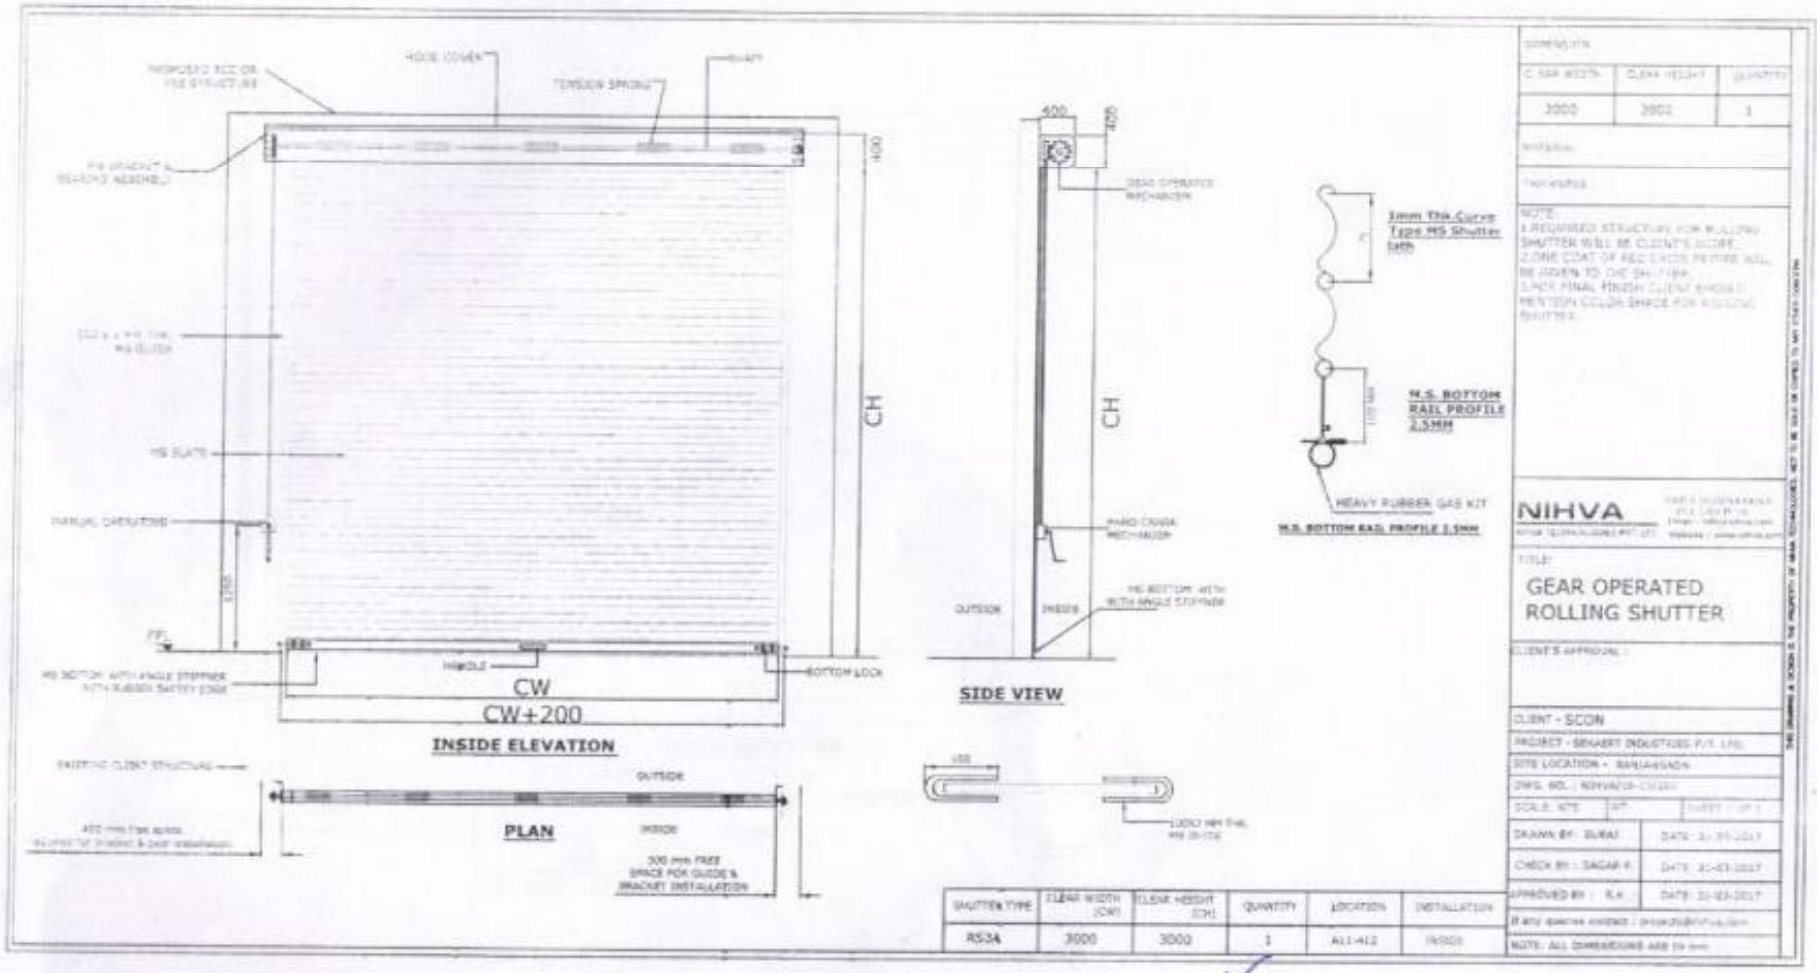


SHUTTER TYPE	CLEAR WIDTH (CW)	CLEAR HEIGHT (CH)	QUANTITY	LOCATION	INSTALLATION
RS3A	3000	3000	1	A11-A12	INSIDE

CLEAR WIDTH	CLEAR HEIGHT	QUANTITY
3000	3002	1

10/09/2015

BJP

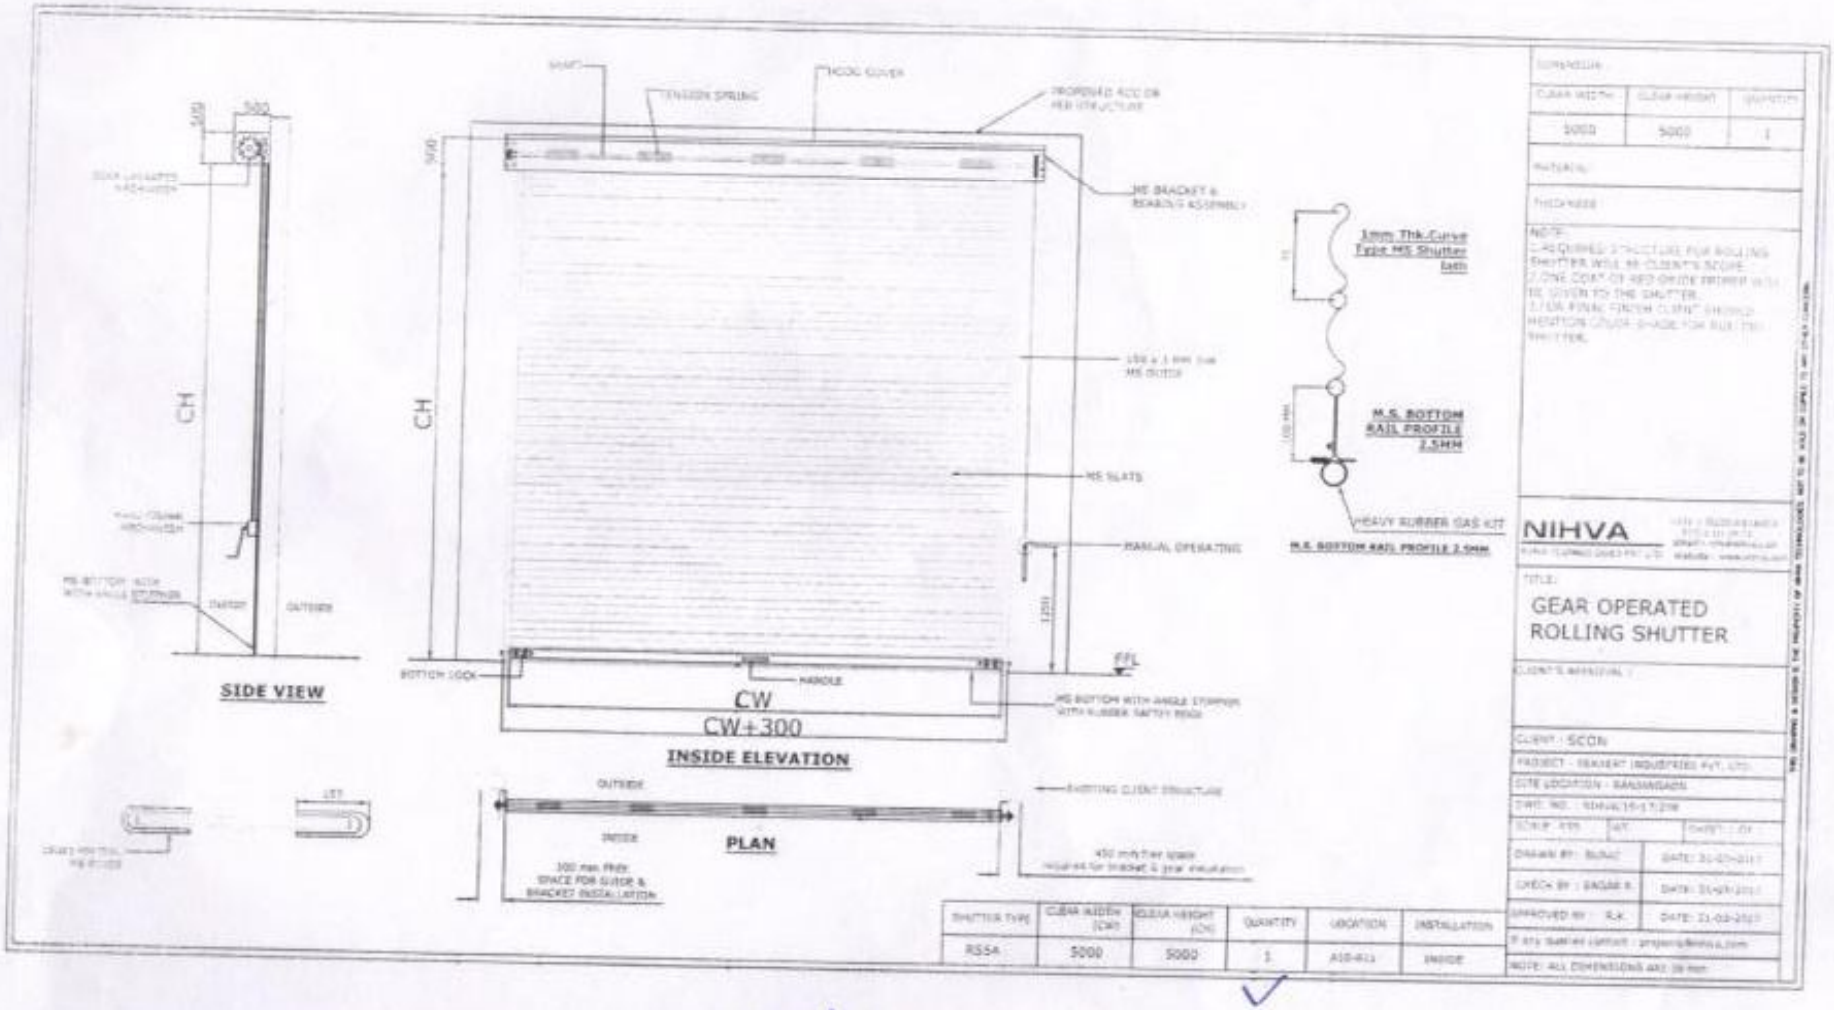
SIDE VIEW
INSIDE ELEVATION
PLAN
CW
CW+300
CH
FFL
MANUAL OPERATING
MS SLATS
HEAVY RUBBER GAS KIT
M.S. BOTTOM RAIL PROFILE 2.5MM
3mm Thk Curve Type MS Shutter Patti
GEAR OPERATED ROLLING SHUTTER
NIHVA
SCON
RSSA
5000
5000
1

10/04/2017