


BOM			
SL NO.	DESCRIPTION	SPECIFICATION	QTY
1	MS SQ. TUBE	60X60X2.6X1695L	2NOS
2	MS SQ. TUBE	60X60X2.6X2345L	2NOS
3	MS SQ. TUBE	40X40X2.6X1575L	1NO
4	MS FLAT	25X5X1575L	2NOS

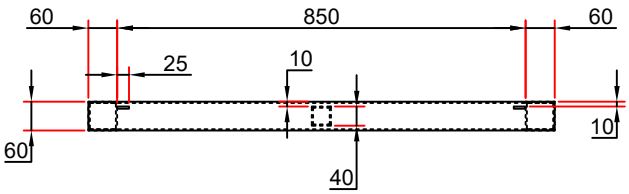

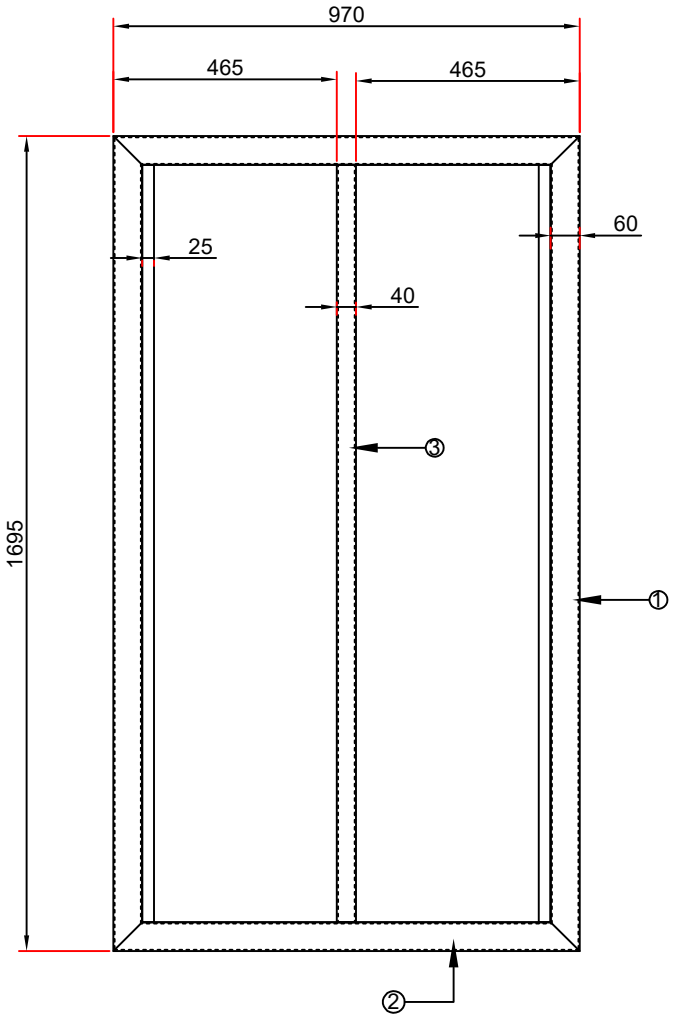

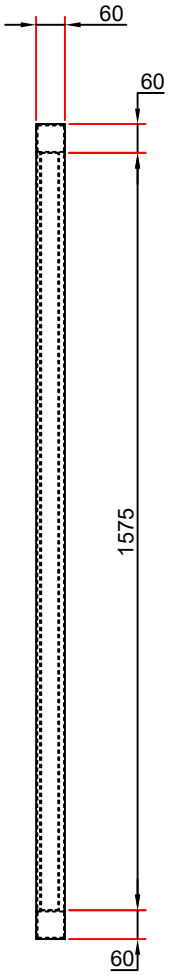

Note:-

1.All dimension are in MM.

2.Kindly maintain the given dimensions.

This drawing & design is the property of NIHVA TECHNOLOGIES. Not to be sold or copied to any other concern.

TITLE:- WICKET GATE

NIHVA TECHNOLOGIES PVT. LTD.
NIHVA TECHNOLOGIES PVT. LTD. PUNE
Tel : 020 66304033
Email:- info@nihva.com
Website:- www.nihva.com

	NAME	DATE	SIGN
DRAWN	SUJATA.B	02/08/2022	
CHECK	MAHESH.S	02/08/2022	
APPRD.	AMIT.K	02/08/2022	

If any queries contact : design@nihva.com

ALL DIMENSION ARE IN mm

CLIENT - Rohit Nair

LOCATION - Undri

PRODUCT - Wicket Gate | QTY:-01 NO

DWG NO:-NIHVA/22-23/MFG/0052 | REV- 0

SCALE: NTS | SCALE:-- 1:1 | SHEET: 01 OF 01

Rev No.	Revision	Date	Revised By