



BOM			
SL NO.	DESCRIPTION	SPECIFICATION	QTY
1	MS SQ. TUBE	60X60X2.6X5650L	2NOS
2	MS SQ. TUBE	60X60X2.6X2345L	2NOS
3	MS SQ. TUBE	60X60X2.6X4470L	1NO
4	MS SQ. TUBE	60X60X2.6X1725L	1NO
5	MS SQ. TUBE	40X40X2.6X1665L	3NOS
6	SQ.BAR	16X16X5530L	2NOS
7	MS FLAT	25X5X1665L	2NOS

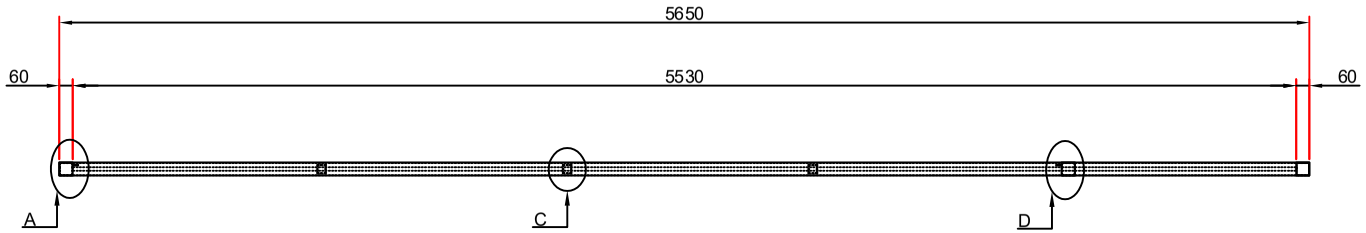


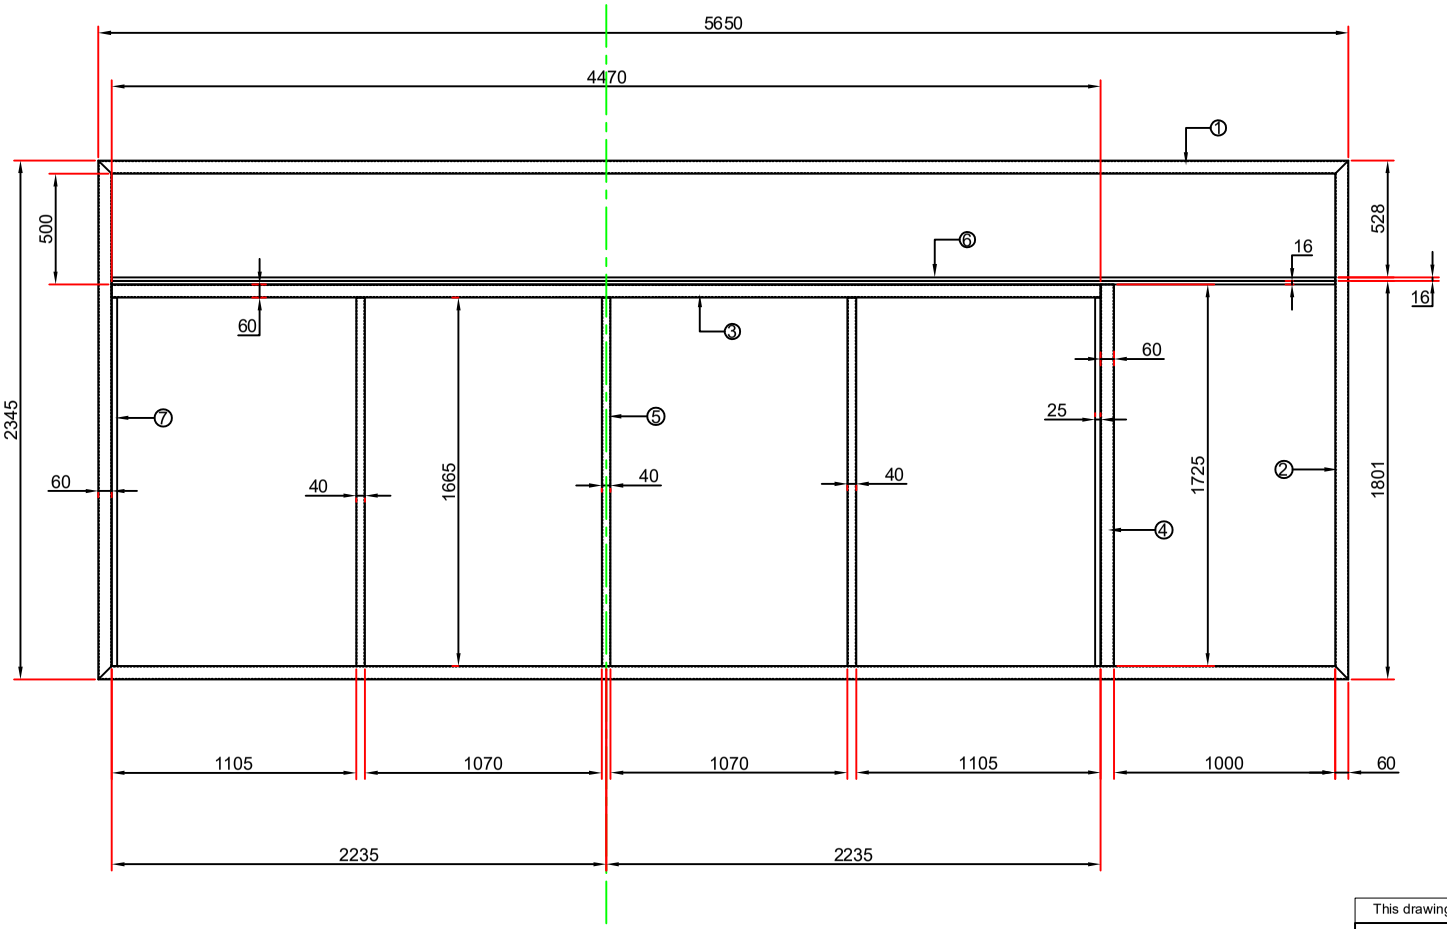

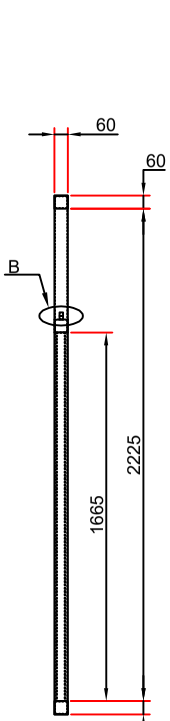


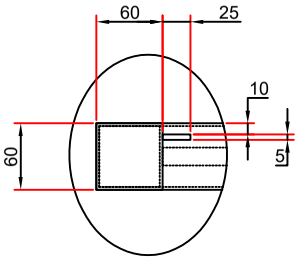


Details: A

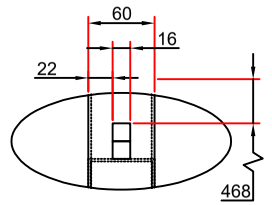

Details: B

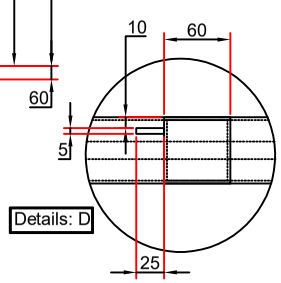

Details: D

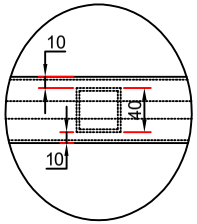

Details: C

Note:-

1.All dimension are in MM.

2.Kindly maintain the given dimensions.

This drawing & design is the property of NIHVA TECHNOLOGIES. Not to be sold or copied to any other concern.

TITLE:- SLIDING GATE

NIHVA TECHNOLOGIES PVT. LTD.

NIHVA TECHNOLOGIES PVT. LTD. PUNE
Tel : 020 66304033
Email:- info@nihva.com
Website:- www.nihva.com

	NAME	DATE	SIGN
DRAWN	SUJATA.B	02/08/2022	
CHECK	MAHESH.S	02/08/2022	
APPRD.	AMIT.K	02/08/2022	

If any queries contact : design@nihva.com

ALL DIMENSION ARE IN mm

CLIENT - Rohit Nair

LOCATION - Undri

PRODUCT -Sliding Gate | QTY-01

DWG NO:- NIHVA/22-23/MFG/0051 | REV-00

SCALE: NTS | SCALE:-- 1:1 | SHEET: 01 OF 01

Rev No.	Revision	Date	Revised By