

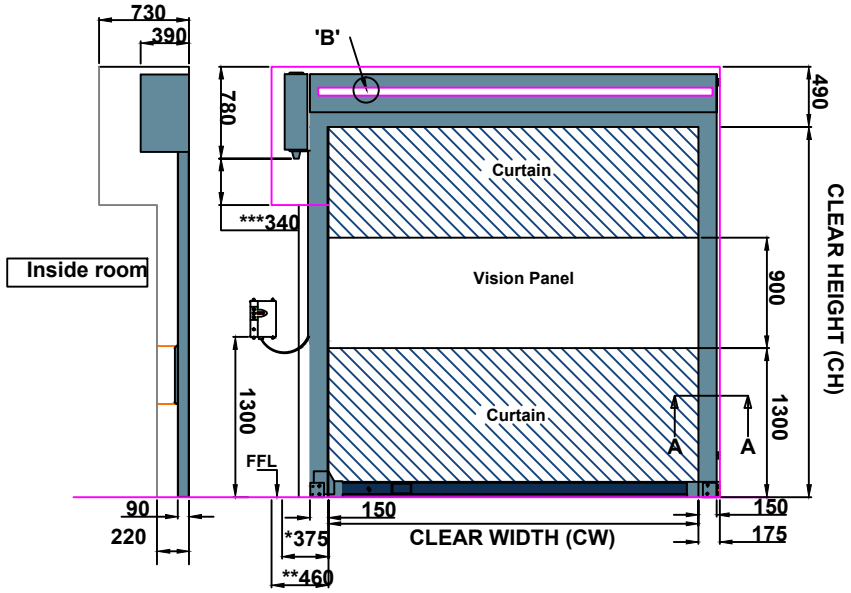


INSIDE ELEVATION

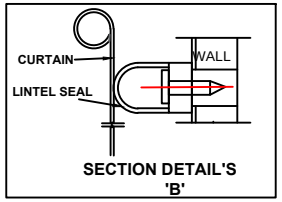


SECTION DETAIL'S 'B'

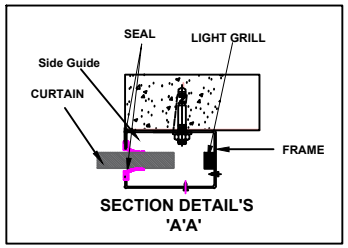

SECTION DETAIL'S 'A'A'

ELCTRICAL REQUIREMENT FROM CLIENT AT SITE-

1) 16A 3 Pin Industrial type female Metal clad socket 230V, 50Hz, with earthing around 1/2 Meter From Controller
2) Clean Uninterrupted Power Supply WithOut Voltage Fluctuations Needed.
3) Solid State Inline (UPS/Stabilizer) 2kva Capacity Required

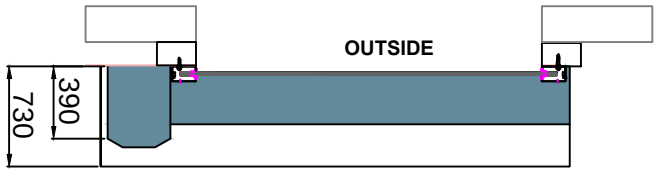

HORIZONTAL SECTION

INSIDE

REV NO	DATE	DRAWN	REMARK
R02	7.12.2020	S.M.S.	(1) MODIFICATION IN EXISTING STRUCTURE (2) DIMENSIONS OF CW & CH CHANGED
R01	3.12.2020	S.M.S.	(1) MOTOR POSITION ON LEFT SIDE FROM INSIDE (2) STRUCTURE MOUNTED (3) DIMENSIONS OF CW & CH CHANGED

Notes:

1) Operator is on Left side.
2) Controller is Always On Operator Side
3) Required All Civil work , MS Structure & Fitting is in client scope.
4) High Speed door will be installed after readiness of structure as per drawing provided.

* Space for fiting the door
** Space require for fit and dismantle the operator
*** For Emergency Crank Handle

3415 MM	4300 MM	1 NO	RAL 5010	ON STRUCTURE
CLEAR WIDTH (CW)	CLEAR HEIGHT (CH)	QTY	RAL COLOUR CURTAIN PANEL	MOUNTING

This drawing & design is the property of NIHVA TECHNOLOGIES. Not to be sold or copied to any other concern.

TITLE- HIGH SPEED DOOR

NIHVA TECHNOLOGIES PVT. LTD.

NIHVA TECHNOLOGIES PVT. LTD. PUNE
Tel : 020 66304033
Email:- info@nihva.com
Website:- www.nihva.com

	NAME	SIGN	DATE
DRAWN	SIDDHESHWAR		1.12.2020
CHECK	K.P.		1.12.2020
APPRD.			

CLIENT - CONGLOMERATE
PROJECT - CONGLOMERATE
SITE LOCATION - PUNE
If any queries contact : projectsupport@nihva.com
DWG. NO. : NIHVA/20-21/0097/R02 REV- R01
ALL DIMENSION ARE IN mm
SCALE: NTS WT: SHEET: