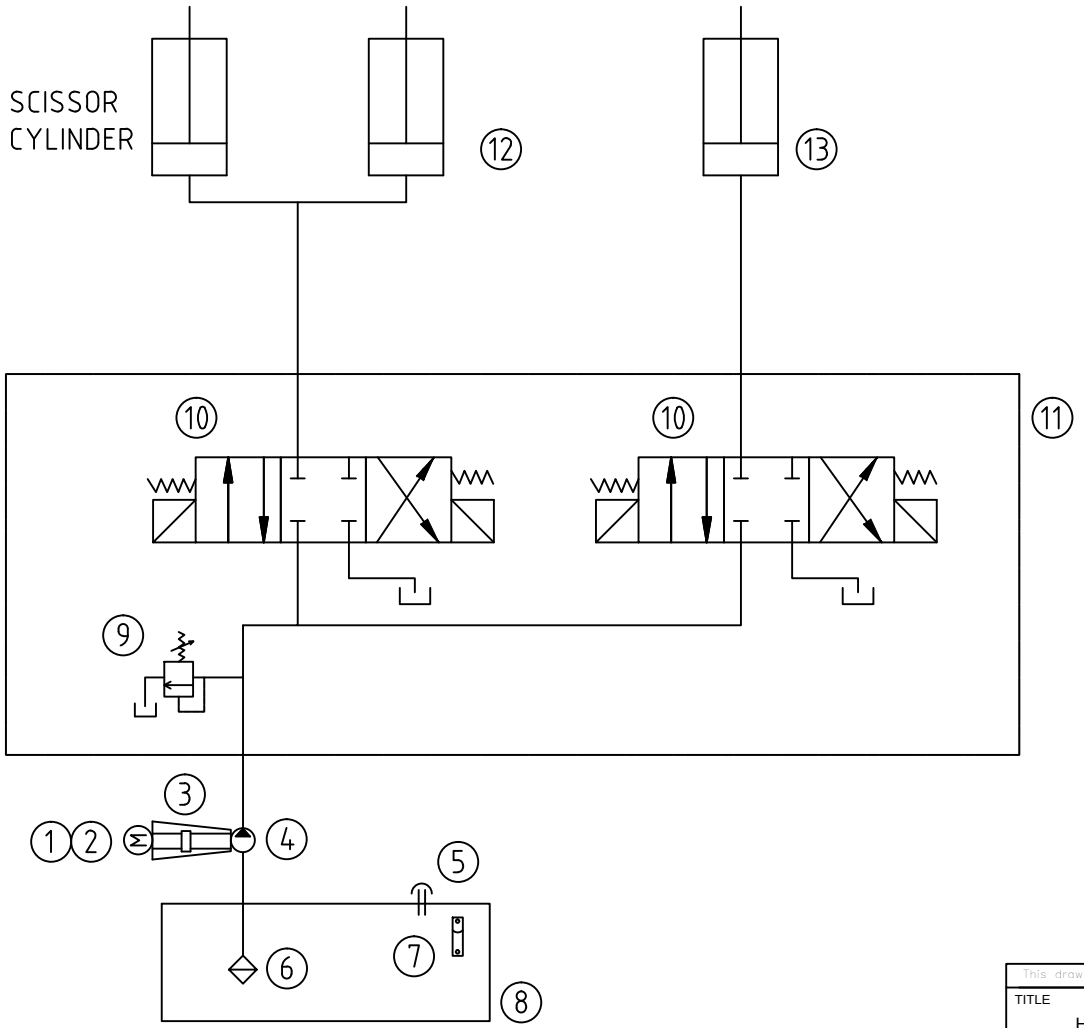


NO.	DESCRIPTION	MAKE	QTY.
13	SINGLE ACTING LIP CYLINDER	NIHVA	1
12	SINGLE ACTING DECK CYLINDER	NIHVA	2
11	MANIFOLD BLOCK	NIHVA	1
10	DIRECTION CONTROL VALVE DSG 13 C2 D24	YUKEN	1
9	PRESSURE RELIEF VALVE DPRS 06	POLYHYDRON	1
8	OIL RESERVOIR 10 LTR	NIHVA	1
7	OIL LEVEL GAUGE LG 3	HYDROLINE	1
6	SUCTION STRAINER SC3 002	HYDROLINE	1
5	FILTER BREATHER FSB 05	HYDROLINE	1
4	GEAR PUMP 2.5 LPM	DOWTY	1
3	GEAR COUPLING	JACKTECH	1
2	1 HP BELL HOUSING	JACKTECH	1
1	ELECTRIC MOTOR 1 HP FOOT. FLAME PROOF	HINDUSTAN ELE.	1

BILL OF MATERIAL

This drawing & design is the property of NIHVA TECHNOLOGIES. Not to be sold or copied to any other concern.

TITLE: HYDRAULIC CIRCUIT

NIHVA TECHNOLOGIES PVT. LTD.
NIHVA TECHNOLOGIES PVT. LTD. PUNE
Tel : 020 66304033
Website:- www.nihva.com
Email:- info@nihva.com

	NAME	SIGN	DATE
DRAWN	P.A		18.08.2020
CHECK	G.J		18.08.2020
APPRD.			

CLIENT - L&T HYDROCARBON
PROJECT - IOCL
SITE LOCATION - ODISHA
If any queries contact : design@nihva.com
DWG. NO. : NIHVA/20-21/0088
REV- 0
ALL DIMENSION ARE IN mm
SCALE: NTS
WT:
SHEET: 01 OF 01