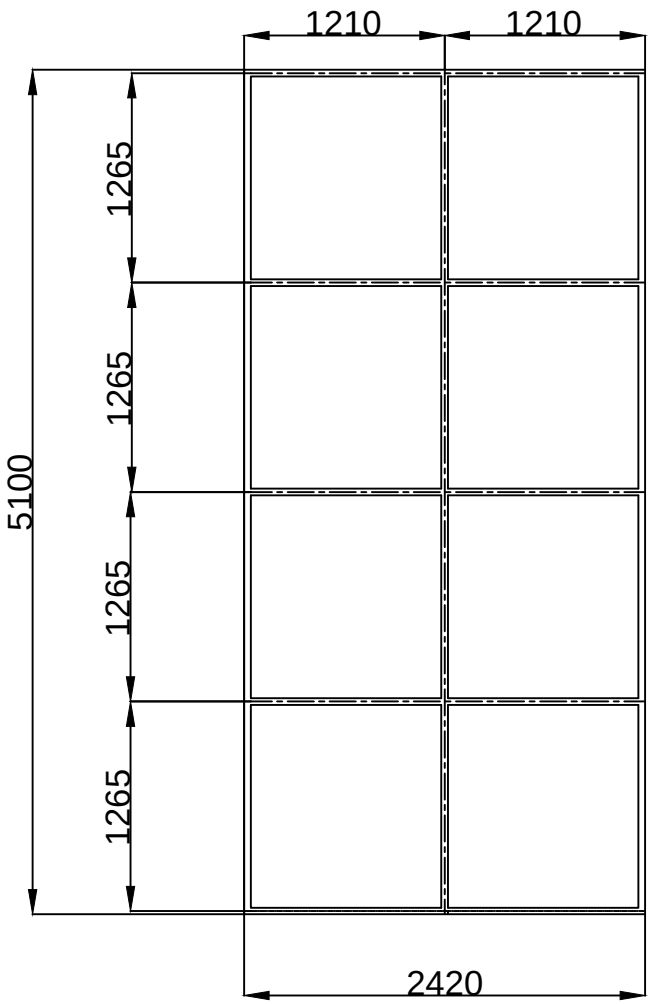

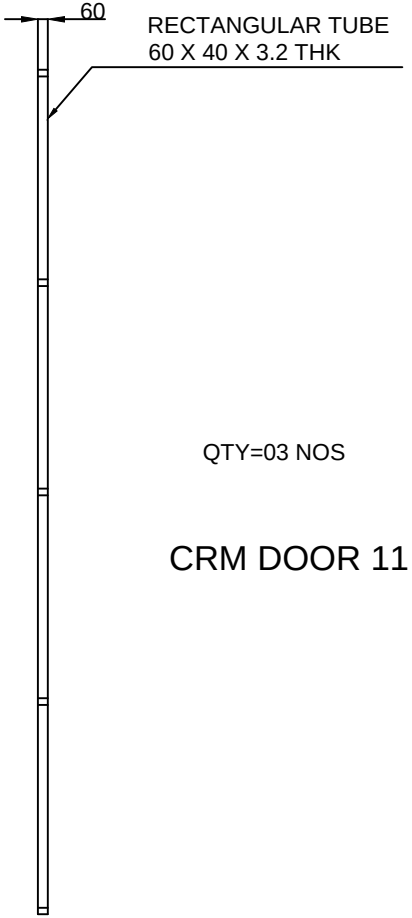

QTY=03 NOS

CRM DOOR 11

This drawing & design is the property of NIHVA TECHNOLOGIES. Not to be sold or copied to any other concern.

TITLE:- 3 LEAF CRM DOOR 11			NIHVA TECHNOLOGIES PVT. LTD. PUNE Tel : 020 66304033 Email:- info@nihva.com Website:- www.nihva.com
	NAME	DATE	SIGN
DRAWN	KISHAN	03/05/2022	
CHECK	M.SUTAR	03/05/2022	
APPRD.			
If any queries contact : design@nihva.com			CLIENT - LESTECH
ALL DIMENSION ARE IN mm			LOCATION - POSCO MANGAON
			PRODUCT - SLIDING DOOR
			DWG NO:-NIHVA/21-22/ REV- 0
			SCALE: NTS SCALE:-- 1:1 SHEET: 01 OF 01

	Date	Revised By