


OUTSIDE VIEW

SLIDING DIRECTION →

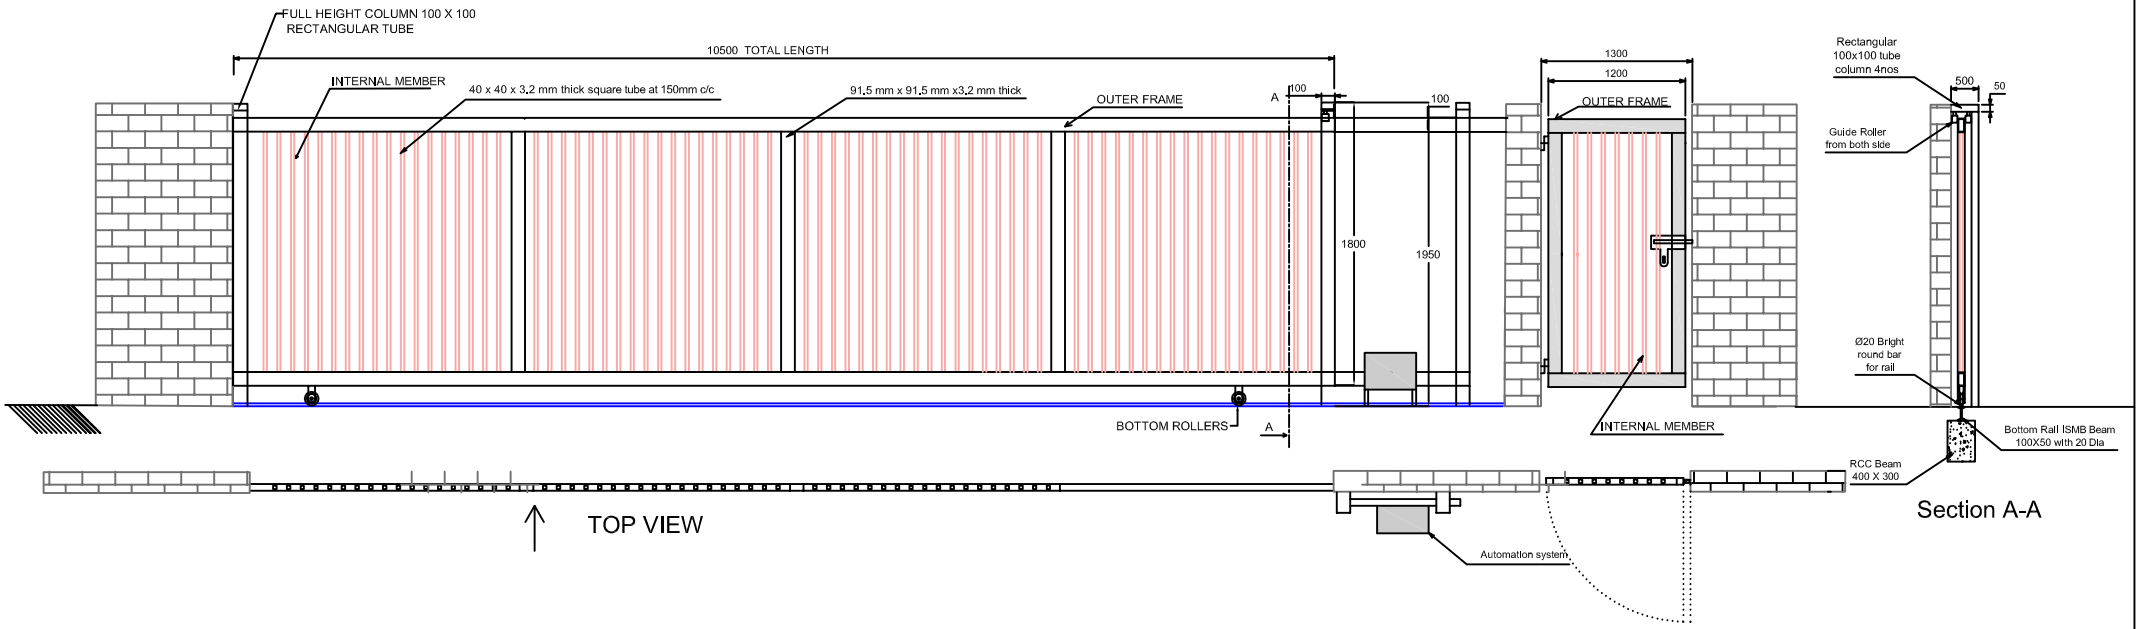

TOP VIEW

Section A-A

Sliding gate size - 9000X1800mm(Clear opening)
Total length of gate - 10500mm
Wicket gate size - 1200X1800mm
No. Of Column - 5 nos.
Factory paint finish - Red oxide primer coat
Final paint @ site - NIHVA scope (RAL-)

Drawn By:-Priyanka	Checked By	Approved By - Date		Date 20-12-13	Scale NTS
NIHVA TECHNOLOGIES PVT. LTD.			CLIENT — Sulzer India Ltd		
			DRG. No. NVA-Sulzer-D1	Revision 00	Sheet 1-1