

Weitergabe sowie Vervielfältigung dieses Dokuments, Verwertung und Mitteilung seines Inhalts sind nur nach vorheriger ausdrücklicher schriftlicher Zustimmung von SMS Meer GmbH gestattet. Das Dokument ist vor unberechtigtem Zugriff Dritter zu schützen. Zuwiderhandlungen verpflichten zu Schadensersatz. Alle Rechte aus Patent-/Gebrauchsmuster-/Markenschutz vorbehalten.

Schnitt (Section) S13-03 - S13-03

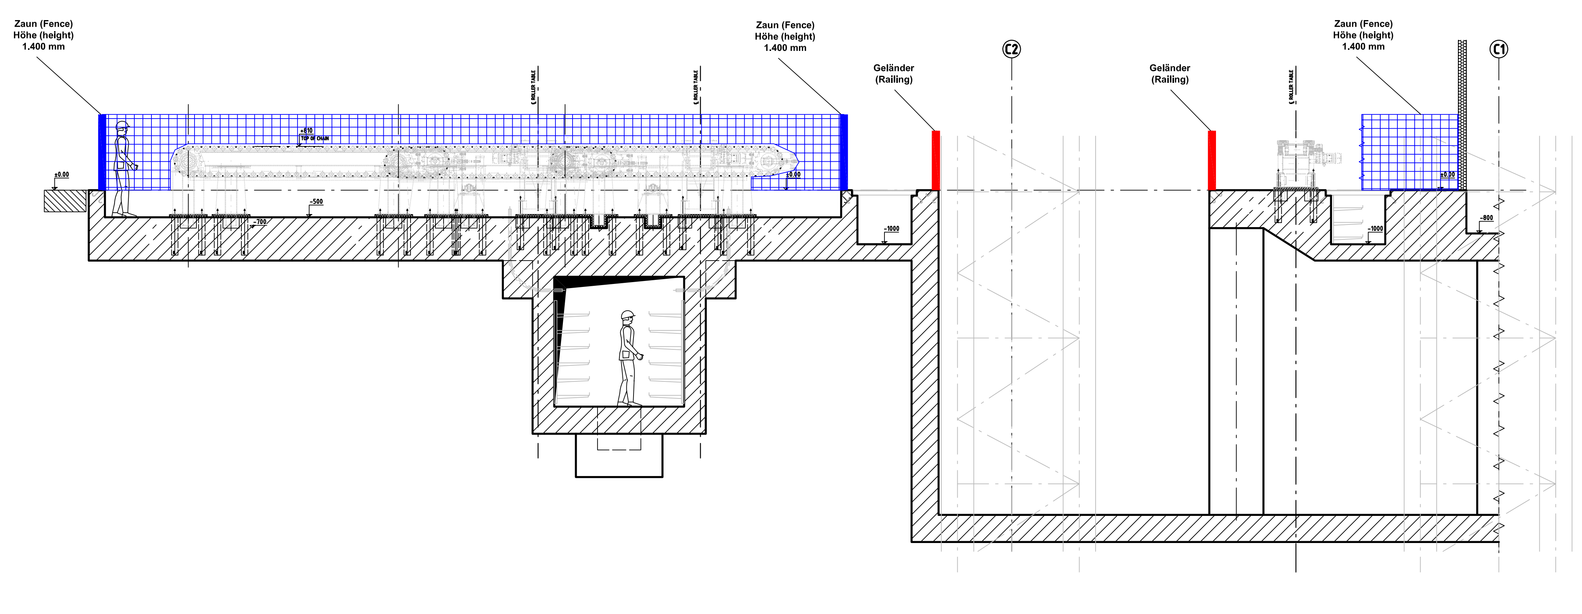

Schnitt (Section) S13-02 - S13-02

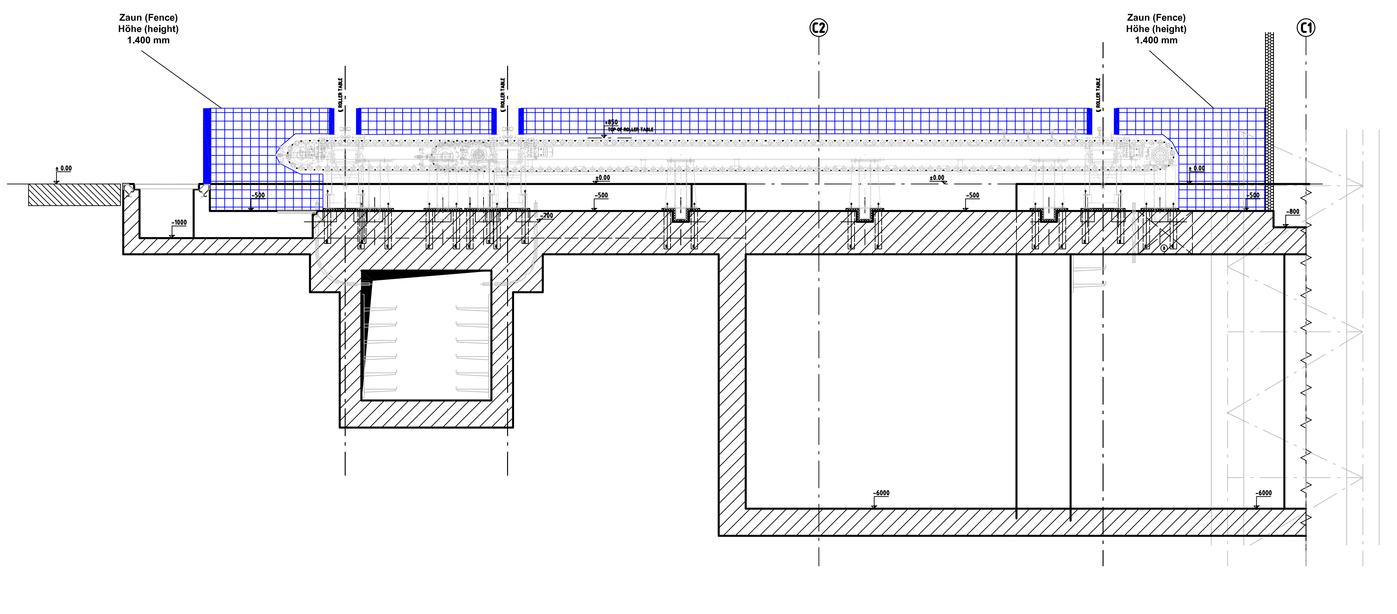

Schnitt (Section) S13-01 - S13-01

9463 0000 / RAILBHL

CATEGORY OF DRWG.	APPROVAL	INFORMATION	REFERENCE	RECORD CONSTRUCTION

BHILAI STEEL PLANT, BHILAI, CHATTISGARH
7,0 MTPA EXPANSION

मेकॉन लिमिटेड
MECON LIMITED

VENSDOR'S NAME: SMS Meer/SMS Meer India/ABB
PACKAGE DESCRIPTION: UNIVERSAL RAIL MILL (Pkg No-047)
TITLE OF DRAWING. PARTITION 13, Safety Layout
SCALE=
VENDOR'S DRG NO.=
PROJECT DRG. NO. BSP-SMS Meer-08-047-21-130-35-BE-06660 REV.

Fertigungsvorschriften / Manufacturing Instructions: SN 200
Ursprung / Origin:
Fertiggewicht / Finished weight: kg
Modell-Nr. / Pattern-No.
Werkstoff / Material
Projektionsmethode 1 / first angle projection method ISO 128

	Datum / Date	Name
bearb. / Drawn	19.10.11	Präzel
gepr. / Checked		-
Norm / Stand		

Typ / Type: Safety Layout
Benennung / Title: TEILBEREICH, 13
PARTITION 13
Maßstab / Scale: 1:50
Sach-Nr. / Drawing-No.: 0100133-00.660
Blatt / Sheet: 02
Blätter / Sheets: 02

Aus-gabe / Issue	Änderung / Revision	Datum / Date	Name

SMS MEER
SMS group

Ersatz für / Supersedes:
Ersetzt durch / Superseded by:

The reproduction, distribution and utilization of this document as well as the disclosure of its content to others without prior explicit written consent of SMS Meer GmbH is prohibited. Holder has to protect this document against unauthorized withdrawal of third parties. Offenders will be held liable for the payment of damages. All rights reserved in case of patent/utility model/tradeware protection.

Diese Zeichnung und alle darauf enthaltenen Informationen sind vertraulich. This drawing and all information on it is confidential.

A1