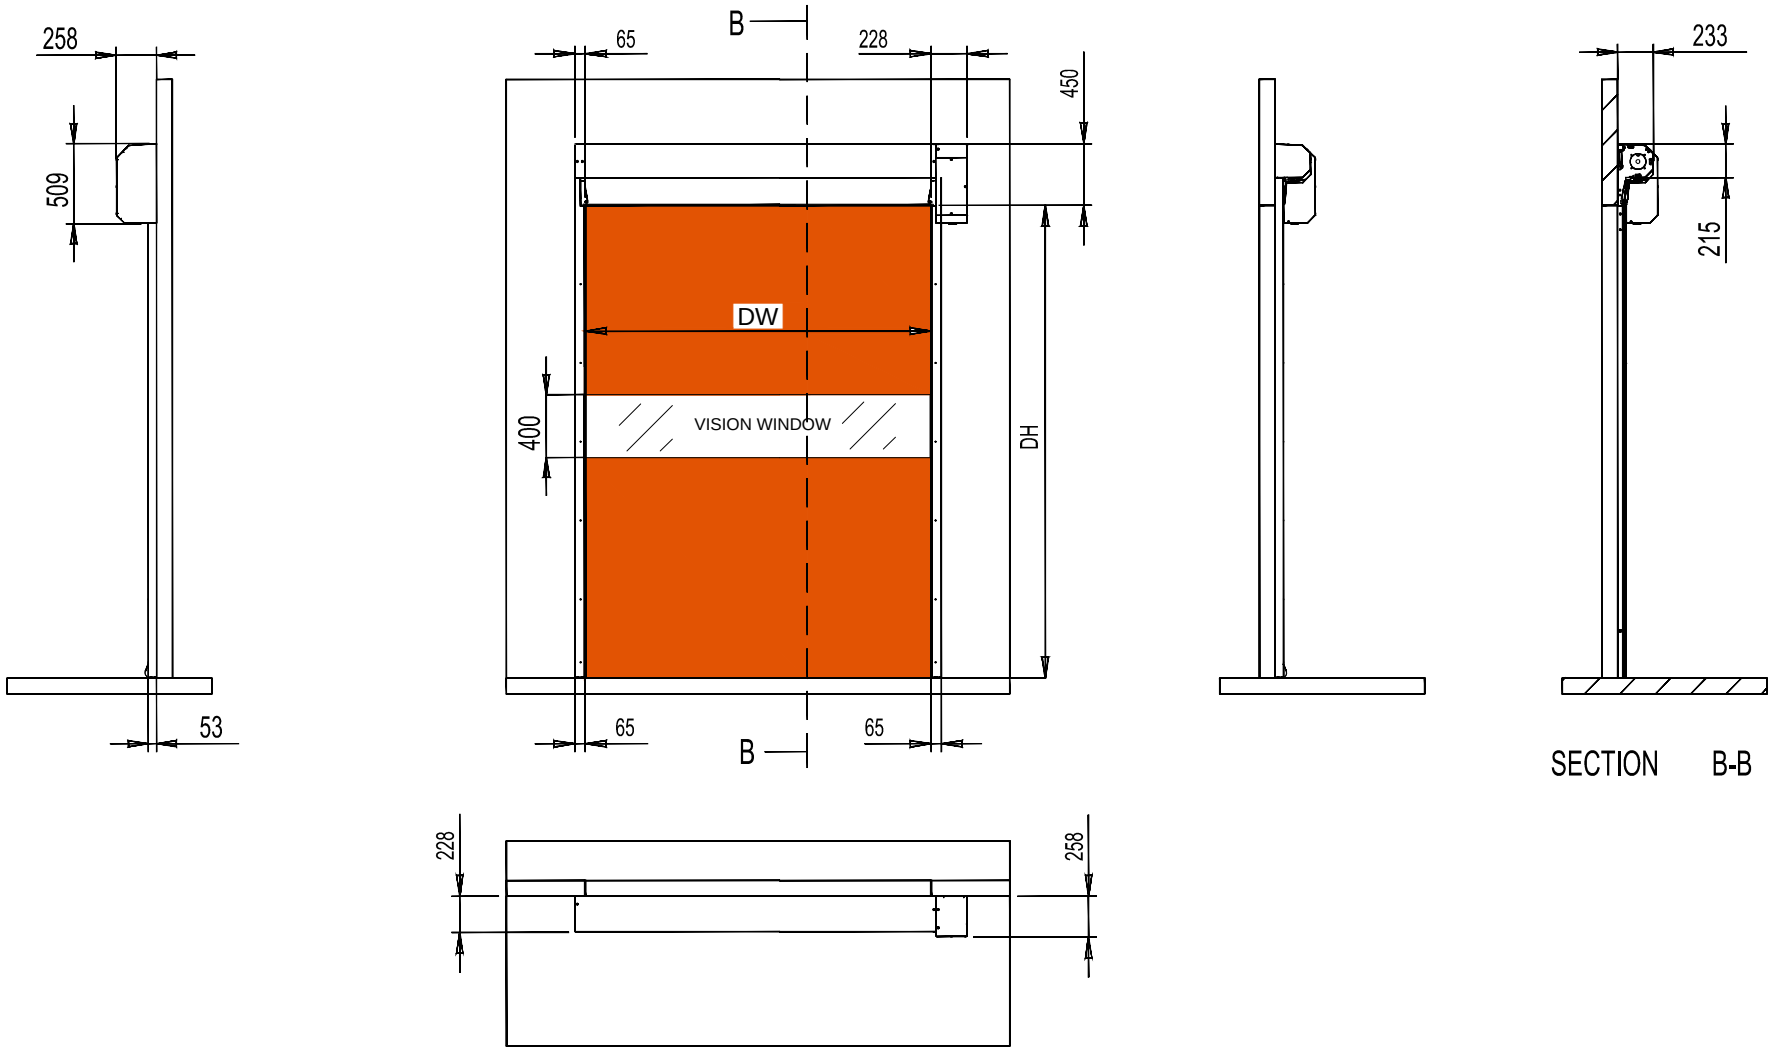


DOOR DIMENSION				
SR NO	DW	DH	MOTOR LOCATION	QUANTITY
1	2200	2100	RIGHT HAND SIDE	01

Color of Curtain- Orange RAL 2004

Note-
1. All Civil work & Structure required for high speed door will be in clients scope.
2. Client has to choose color for door curtain.
3. Client has to choose motor side (Right/left) according to the site conditions. Standard door comes with Right side Motor mounting.

This drawing & designing is the property of NIHVA TECHNOLOGIES. Not to be sold or copied to any other concern.

TITLE: HIGH SPEED DOOR HS9020G

NIHVA TECHNOLOGIES PVT. LTD. PUNE
Tel : 020 66304033
Email:- info@nihva.com
Website:- www.nihva.com

	NAME	SIGN	DATE
DRAWN	SURAJ		06/06/18
CHECK	PRADEEP		06/06/18
APPROVAL	PRADEEP		06/06/18

CLIENT - Fibro,India
PROJECT -
SITE - Chakan
If any queries contact : design@nihva.com
DWG. NO. : NIHVA/17-18/0054. REV- 0
ALL DIMENSION ARE IN mm
SCALE: NTS WT: SHEET: 01 OF 01