
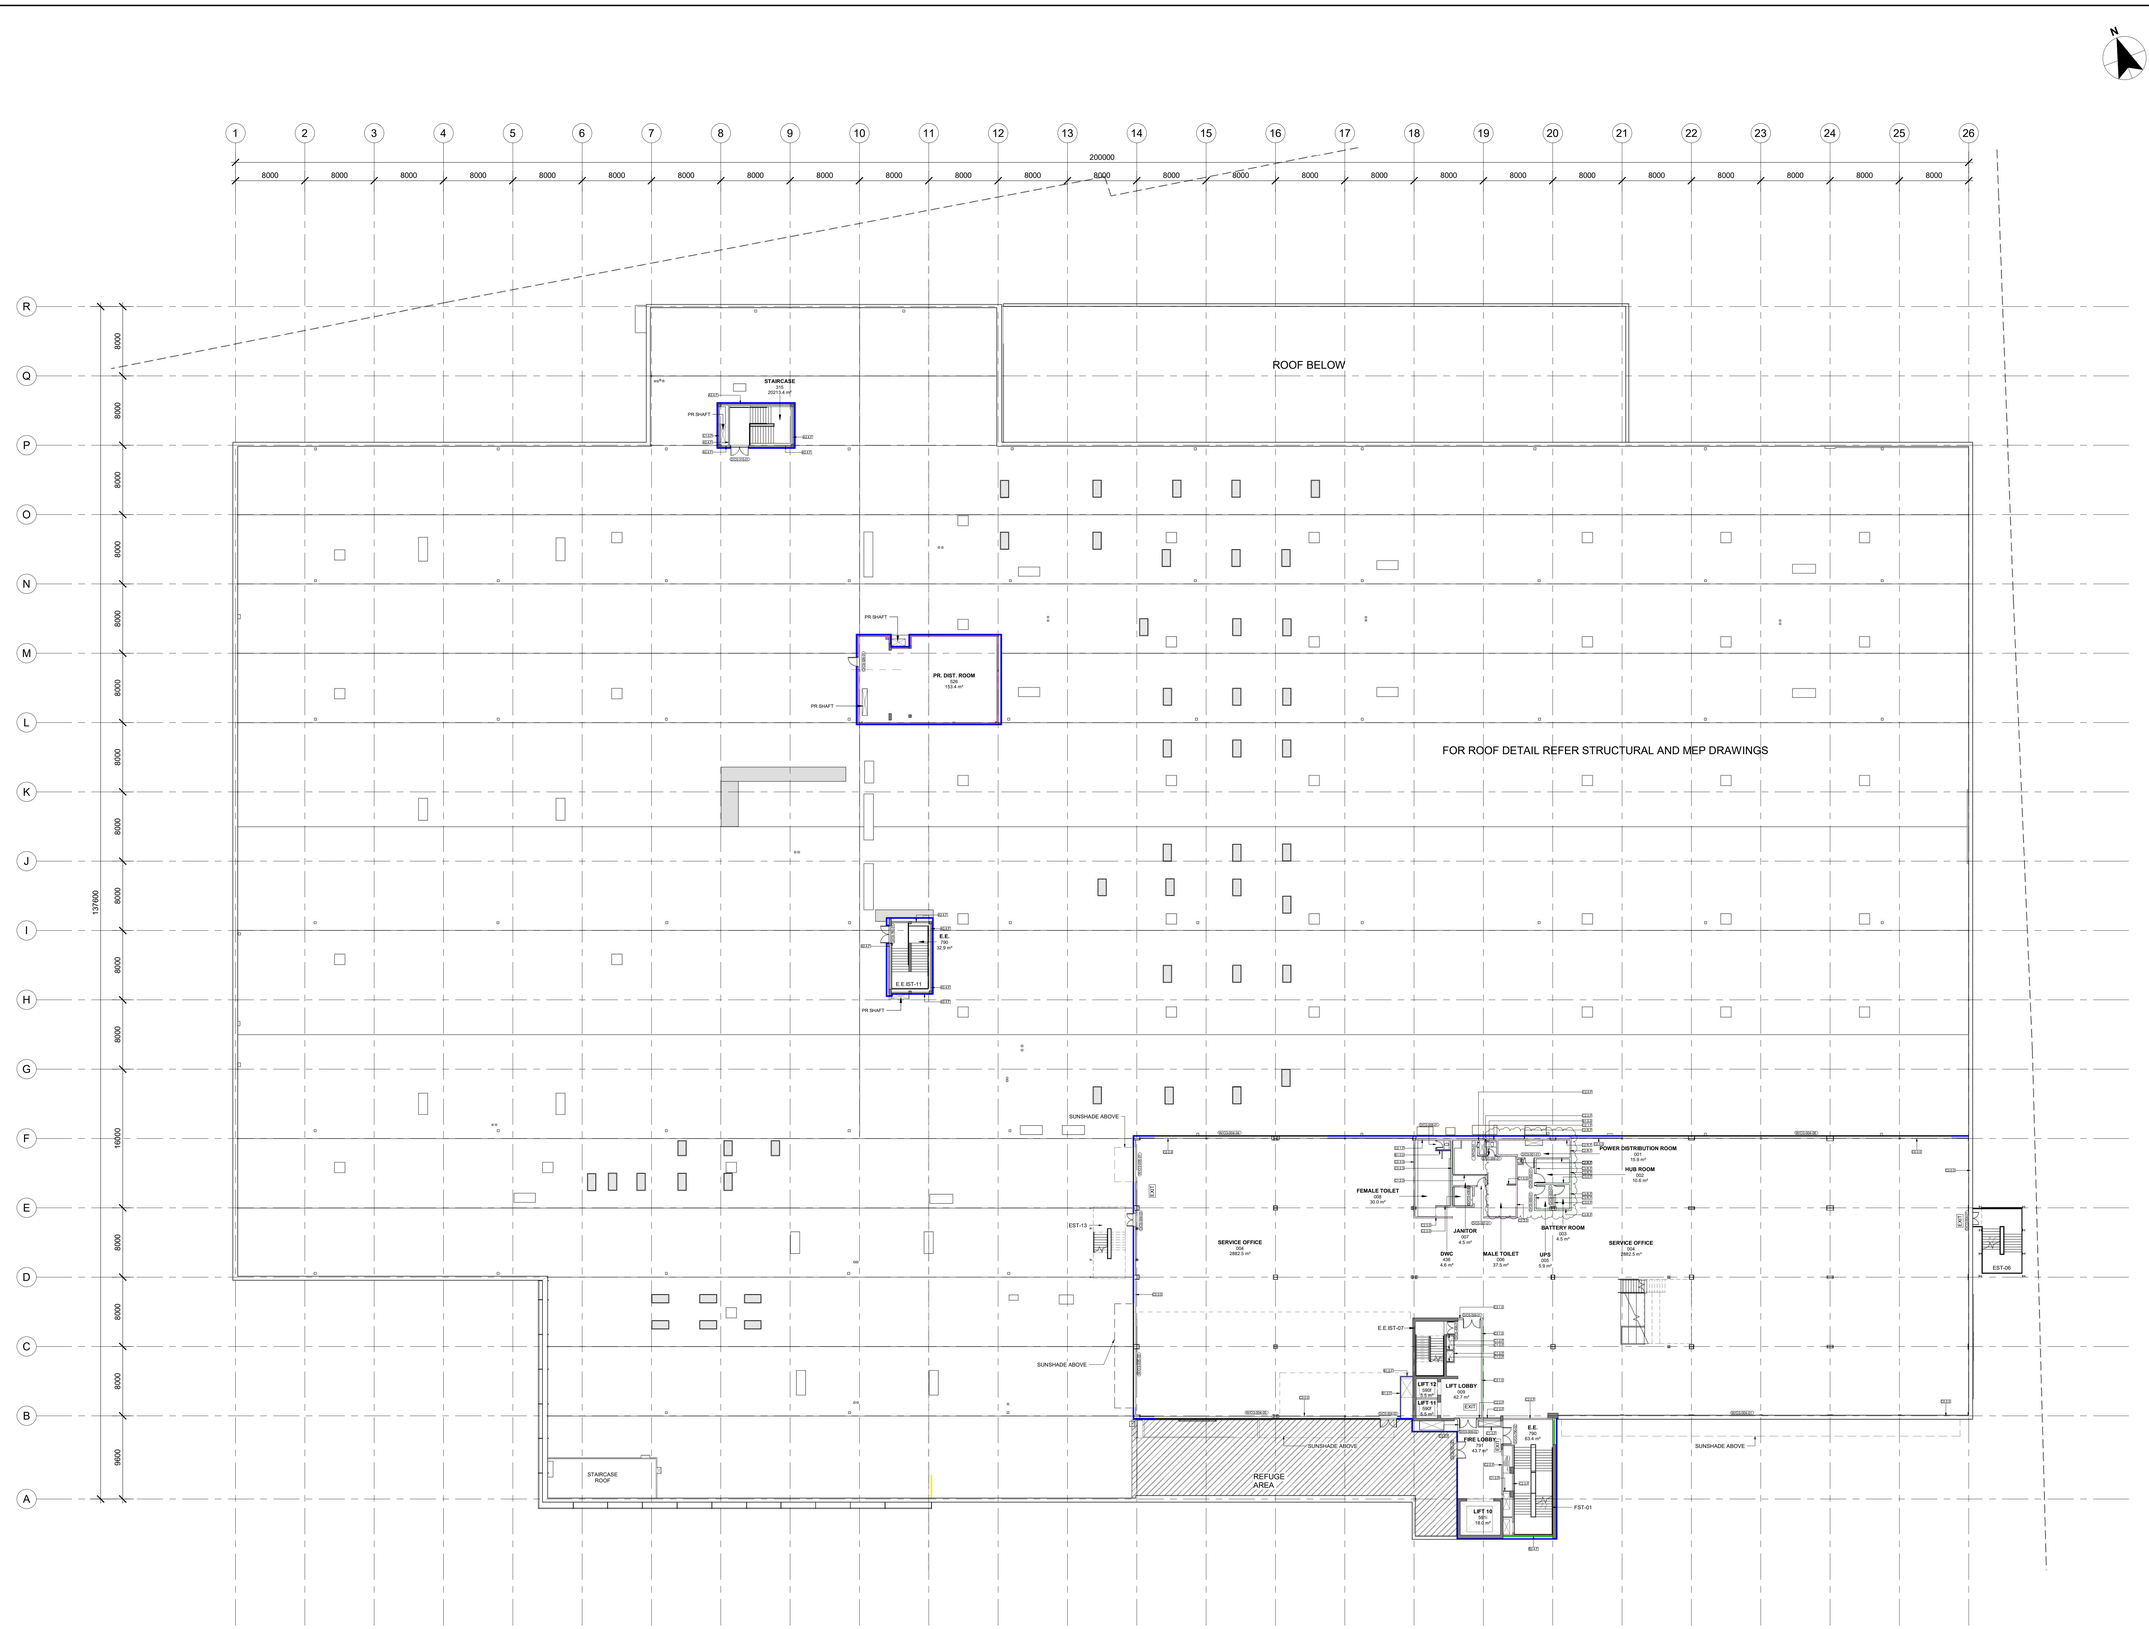


1 OFFICE LEVEL O3
0215 SCALE 1 : 250

DO NOT SCALE

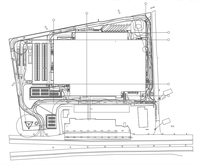

GENERAL NOTES:

ALL DIMENSIONS ARE IN MILLIMETERS & LEVELS ARE IN METERS.

DO NOT SCALE DRAWINGS: ALL DIMENSIONS SHALL HAVE PREFERENCE OVER SCALE AND BE FIELD VERIFIED AND COORDINATED WITH WORK OF ALL TRADES. IF NO DIMENSIONS ARE GIVEN OR DISCREPANCIES FOUND, THE CONTRACTOR SHALL NOTIFY THE ARCHITECT FOR CLARIFICATION BEFORE BIDDING OR COMMENCING THE WORK.

ALL WORKS TO BE CARRIED OUT IN STRICT ACCORDANCE WITH LOCAL AUTHORITY REQUIREMENTS, NATIONAL BUILDING REGULATIONS & RELEVANT STANDARDS.

ARCHITECTURAL DRAWINGS SHOULD BE READ IN CONJUNCTION WITH PROJECT SPECIFICATIONS, STRUCTURAL, MECHANICAL, ELECTRICAL, PLUMBING, FIRE & LANDSCAPE DRAWINGS AND ARCHITECTURE TECHNICAL SPECIFICATION DOCUMENT (PJNAB-ATK-ARC-SPC-NA-0001)

FOR ALL DETAILS OF CIVIL & STRUCTURAL WORKS, REFER STRUCTURAL DRAWINGS.

FOR ALL MECHANICAL EQUIPMENT, FIXTURES, SERVICES & RELATED WORKS, REFER MECHANICAL DRAWINGS.

FOR ALL ELECTRICAL EQUIPMENT, FIXTURES, SERVICES & RELATED WORKS, REFER ELECTRICAL DRAWINGS.

FOR ALL PLUMBING EQUIPMENT, FIXTURES, SERVICES & RELATED WORKS, REFER PLUMBING DRAWINGS.

FOR ALL FIRE EQUIPMENT, FIXTURES, SERVICES & RELATED WORKS, REFER FIRE DRAWINGS.

FOR ALL LANDSCAPE ELEMENTS, TREES LOCATION, MATERIALS & RELATED WORKS, REFER LANDSCAPE DRAWINGS.

FOR NOTES, SYMBOLS & LEGENDS REFER PJNAB-ATK-ARC-DWG-NA-0006.

THE CONTRACTOR SHALL COMPARE THE ARCHITECTURAL, STRUCTURAL, MECHANICAL, ELECTRICAL, PLUMBING, FIRE & LANDSCAPE DRAWINGS. THE CONTRACTOR MUST REPORT ANY DISCREPANCIES BETWEEN EACH SET OF DRAWINGS TO THE ARCHITECT BEFORE COMMENCEMENT OF WORK.

THE BUILDING SHALL BE CONSTRUCTED IN FULL COMPLIANCE WITH ALL APPLICABLE CODES, ORDINANCES AND REGULATIONS AS WELL AS THE DRAWINGS AND SPECIFICATIONS. ANY CODE DEFICIENCIES IN THE DRAWINGS RECOGNIZED BY THE CONTRACTOR SHOULD BE BROUGHT TO THE ATTENTION OF THE ARCHITECT FOR CLARIFICATION.

THE CONTRACTOR SHALL BE RESPONSIBLE FOR THE ACCURATE PLACEMENT OF THE BUILDING ON THE SITE AND VERIFY ALL DIMENSIONS AND EXISTING CONDITIONS. DISCREPANCIES BETWEEN DRAWINGS AND ACTUAL SITE CONDITIONS SHALL BE BROUGHT TO THE ATTENTION OF THE ARCHITECT BEFORE BIDDING THE PROJECT OR THE COMMENCEMENT OF WORK. THE OWNER SHALL NOT BE RESPONSIBLE FOR CHANGES TO THE WORK DUE TO THE FAILURE OF THE CONTRACTOR TO FAMILIARIZE HIMSELF WITH EXISTING CONDITIONS.

THE CONTRACTOR SHALL PROVIDE ALL PERMITS AND INSPECTION NECESSARY FOR THE PROPER EXECUTION OF THE WORK IN ACCORDANCE WITH APPLICABLE CODES AND GOVERNING REGULATIONS.

THE DRAWINGS HAVE BEEN PREPARED BASED ON THE APPROVED DESIGN FROM THE CLIENT, BASIS THE FOLLOWING STANDARDS & REGULATIONS:

- IKEA ENGINEERING & CONSTRUCTION MANUAL (IKEA Ind-TRANSMIT-000027)
- IKEA STANDARDS (IKEA Ind-TRANSMIT-000027)
- IKEA REFERENCES
- IKEA GROUP SAFETY & SECURITY MANUAL - RETAIL
- IKEA SHE MANUAL
- NATIONAL BUILDING CODE (NBC) 2016
- BANGALORE MAHANAGARA PALIKE BUILDING BYE-LAWS 2003
- REVISED MASTER PLAN 2015, BANGALORE, 2007 - VOLUME - III
- BUREAU OF INDIAN STANDARDS (BIS)

NOTE: ALL WET AREA DRYWALLS WILL HAVE 100 MM HIGH BLOCKWORK UPSTAND.

LEGEND

- IKEA BLUE PANEL CLADDING
- IKEA YELLOW PANEL CLADDING
- BLOCKWORK 100mm
- BLOCKWORK 200mm
- INTERNAL SANDWICH PANEL
- INTERNAL SANDWICH PANEL-BLUE
- INTERNAL SANDWICH PANEL-GREY
- STRUCTURAL WALL
- GYPSUM LINING 30mm
- GYPSUM 100mm
- GYPSUM 150mm
- GYPSUM 200mm
- GYPSUM 300mm
- GYPSUM 100mm Reinforced
- GYPSUM 150mm Reinforced
- GYPSUM 200mm Reinforced

WALL TYPES

DETAIL		AR	FR	KEY	DETAIL		AR	FR	KEY
BLOCKWORK	100mm 00dB		-	B1.0.0	GYPSUM	150mm 40dB	120		C2.2.F
BLOCKWORK	100mm 00dB	120		B1.0.F	GYPSUM	150mm 44dB	120		C2.3.F
BLOCKWORK	200mm 00dB	120		B3.0.F	GYPSUM	150mm 52dB	120		C2.4.F
BLOCKWORK	200mm 35dB	120		B3.1.F	GYPSUM Reinforced	150mm 40dB	120		C2.R.F
BLOCKWORK	200mm 40dB	120		B3.2.F	GYPSUM	200mm 00dB	-		C3.0.0
GYPSUM	30mm 00dB	-		C0.0.0	GYPSUM	200mm 35dB	-		C3.1.0
GYPSUM	100mm 00dB	-		C1.0.0	GYPSUM	200mm 40dB	-		C3.2.0
GYPSUM	100mm 35dB	-		C1.1.0	GYPSUM	200mm 44dB	-		C3.3.0
GYPSUM	100mm 40dB	-		C1.2.0	GYPSUM	200mm 00dB	120		C3.0.F
GYPSUM	100mm 44dB	-		C1.3.0	GYPSUM	200mm 35dB	120		C3.1.F
GYPSUM	100mm 00dB	120		C1.0.F	GYPSUM	200mm 40dB	120		C3.2.F
GYPSUM Reinforced	100mm 40dB	120		C1.R.F	GYPSUM	200mm 52dB	120		C3.4.F
GYPSUM	150mm 00dB	-		C2.0.0	GYPSUM Reinforced	200mm 40dB	120		C3.R.F
GYPSUM	150mm 35dB	-		C2.1.0	GYPSUM	300mm 00dB	120		C4.0.F
GYPSUM	150mm 40dB	-		C2.2.0	WAREHOUSE	150mm 52dB	120		A1.4.F
GYPSUM	150mm 44dB	-		C2.3.0	BLUE INTERNAL SANDWICH PANEL	150mm 52dB	120		A2.4.F
GYPSUM	150mm 52dB	-		C2.4.0					
GYPSUM	150mm 00dB	120		C2.0.F	GREY INTERNAL SANDWICH PANEL	150mm 52dB	120		A3.4.F
GYPSUM	150mm 35dB	120		C2.1.F					

WALLS/DOORS AS PER IFS/COMMERCIAL PLANNING - SHOWN IN GREY / HALFTONE

Drawing Status

ISSUED FOR CONSTRUCTION

Rev.	Date	Description	By	Chk'd	Appd
R1	29/03/2019	ISSUED FOR CONSTRUCTION	BS	CTK	SD
R0	27/02/2019	ISSUED FOR CONSTRUCTION	LH	CTK	SD

SAFETY, HEALTH AND ENVIRONMENTAL INFORMATION

In addition to the hazards/risks normally associated with the types of work detailed on this drawing, note the following:

CONSTRUCTION

REINFORCED DRYWALLS ADDED

MAINTENANCE/CLEANING

DECOMMISSIONING/DEMOLITION

It is assumed that all works will be carried out by a competent contractor working, where appropriate, to an approved method statement

Client

IKEA India Private Limited
DLF Infinity Tower- A,
8th Floor, Cyber City,Sector 25,
Gurgaon- 122002
Haryana, India

This document/drawing is the property of Inter IKEA Systems B.V. and may, in no way other than for the agreed purpose, be used, copied, reproduced, or in any other manner made known to a third party, and shall after its intended use be returned to Inter IKEA Systems B.V. © Inter IKEA Systems B.V., [2016]

ATKINS
18th and 19th Floor
Tower C, DLF Cyber Greens,
DLF Cyber City,
DLF Phase- III, Gurgaon,
Haryana- 122 002, India

Tel: +(91) 124 384 7199
Fax: +(91) 124 455 2475

www.atkinsglobal.com

Copyright © Atkins Limited (2013)

Project Title

IKEA
BENGALURU

Drawing Title

WALL AND DOOR TYPES
OFFICE (O3) LEVEL PLAN

Scale	Designed	Drawn	Checked	Authorised
1 : 250	BS	BS	AD	SD
Original Size	Date	Date	Date	Date
A0	22/12/2017	15/07/2018	11/10/2018	17/10/2018

Drawing Number: PJNAB-ATK-ARC-GFP-O3-0215

Revision: R1