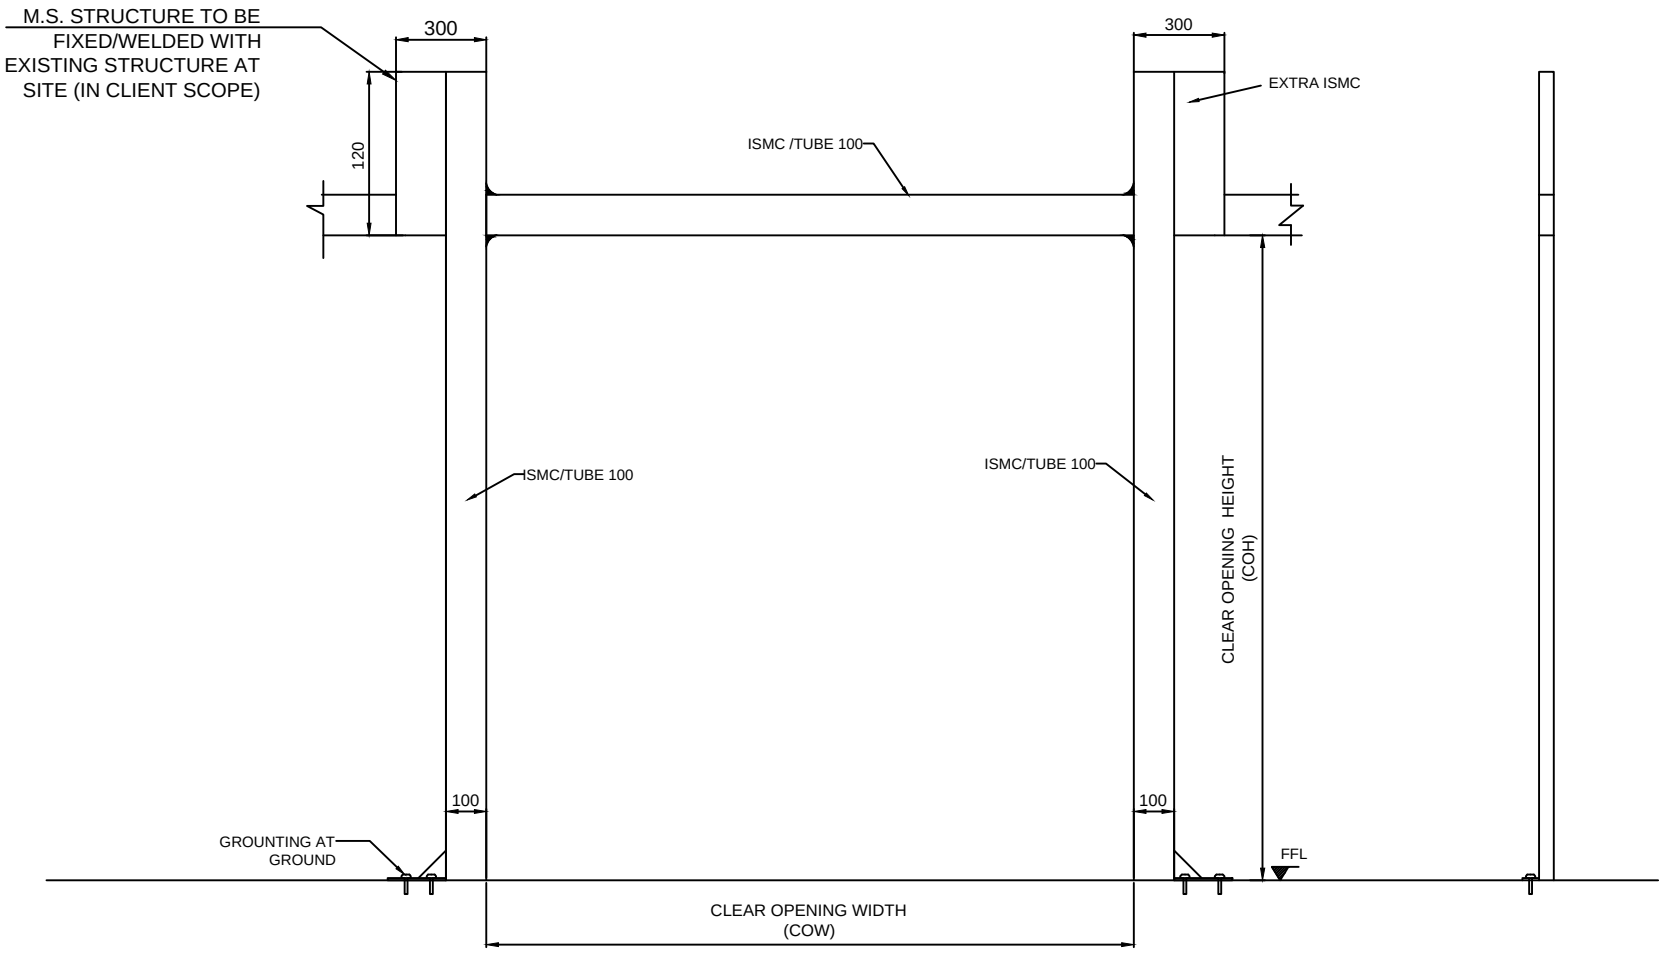


STRUCTURE

TOLERANCE - ±10mm

NOTES-
(1) MS STRUCTURE , FITTING & ALL CIVIL WORK IS IN CLIENT SCOPE.
(2) SHUTTER WILL BE ONLY INSTALLED AFTER READINESS OF STRUCTURE AS PER DRAWING PROVIDED.
(3) SPACE OF 700 mm ABOVE CLEAR HEIGHT IS REQUIRED FOR INSTALLATION OF GEAR OPERATED ROLLING SHUTTER.

This drawing & design is the property of NIHVA TECHNOLOGIES. Not to be sold or copied to any other concern.

TITLE	GEAR OPERATED ROLLING SHUTTER STRUCTURE			NIHVA TECHNOLOGIES PVT. LTD. PUNE Tel : 020 66304033 Email:- info@nihva.com
	NAME	SIGN	DATE	Website:- www.nihva.com
DRAWN	S.M.S.		11.1.2021	CLIENT - TRANS ENGG
CHECK	V.T.		11.1.2021	PROJECT -
APPRD.				SITE LOCATION -
If any queries contact : design@nihva.com				DWG. NO. : NIHVA/20-21/0129 REV- R00
ALL DIMENSION ARE IN mm				SHEET: 01 OF 01