

DRAWING

| REV DESCRIPTION | DATE | REV NO |
|---|---|---|
| | 17-06-2026 | REV 00 |
| 1. | | |

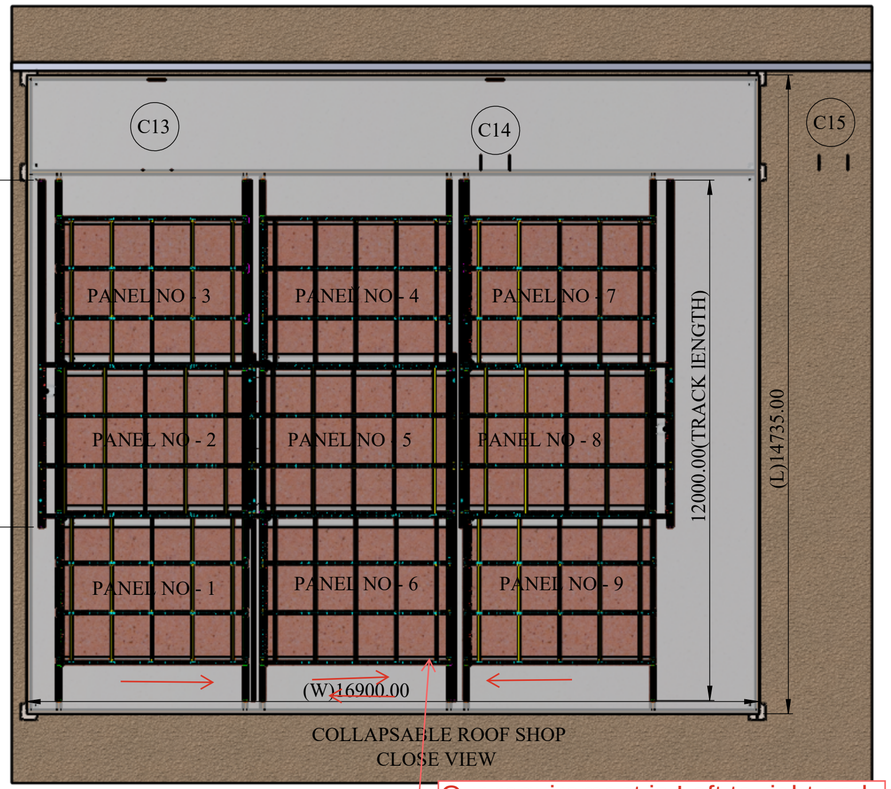



COLLAPSABLE ROOF SHOP
CLOSE VIEW

T.V.

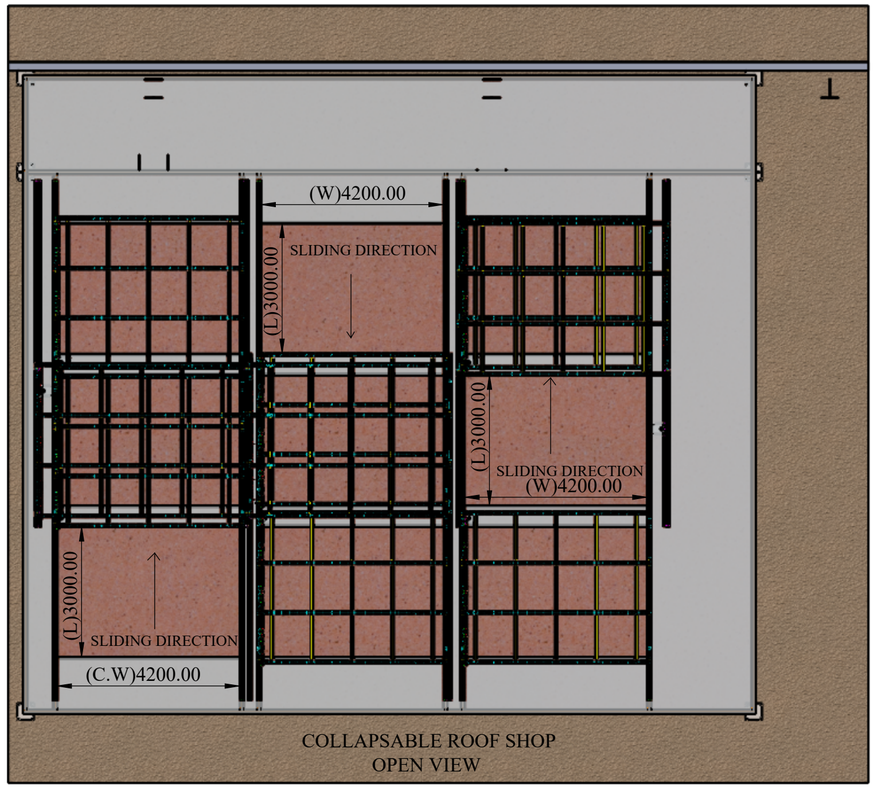



COLLAPSABLE ROOF SHOP
OPEN VIEW

Our requirement is Left to right and right to left . so please change this orientation

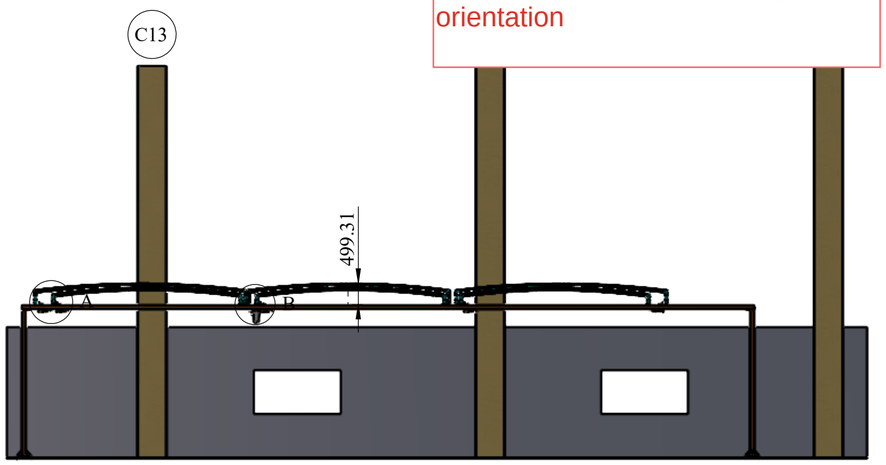


F.V.

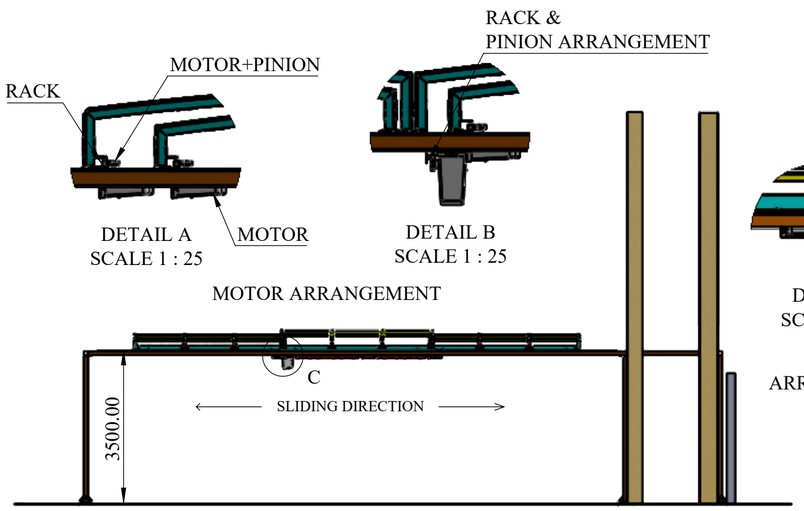


S.V.



DETAIL C
SCALE 1 : 30

MOTOR
ARRANGEMENT

NOTE :

THIS DRAWING IS FOR CLIENT APPROVAL
BASE STRUCTURE IN CLIENT SCOPE

SPECIAL INSTRUCTION'S :

This drawing & design is the property of NIHVA TECHONOLOGIES PVT. LTD. Not to be sold or copied to any other concern

TITLE - COLLAPSABLE CCA ROOF


DWG NO - NTPL-401-PM-04


NIHVA TECHNOLOGIES PVT.LTD.PUNE
Website - www.nihva.com

| | NAME | SIGNATURE | DATE |
|---|---|---|---|
| DRAWN | V.W. | | 17-06-2026 |
| CHK'D | S.P. | | 18-06-2026 |
| APPV'D | V.T. | | 18-06-2026 |

PRODUCT - RETRACTABLE ROOF
CLIENT NAME - NEOTRAFO SOLUTIONS
SITE LOCATION - HYDRABAD
MATRIAL - QTY - 1
If any queries contact - info@nihva.com
PROJECTION METHOD:
SCALE :
ALL DIMENSION ARE IN mm A2

DRAWING

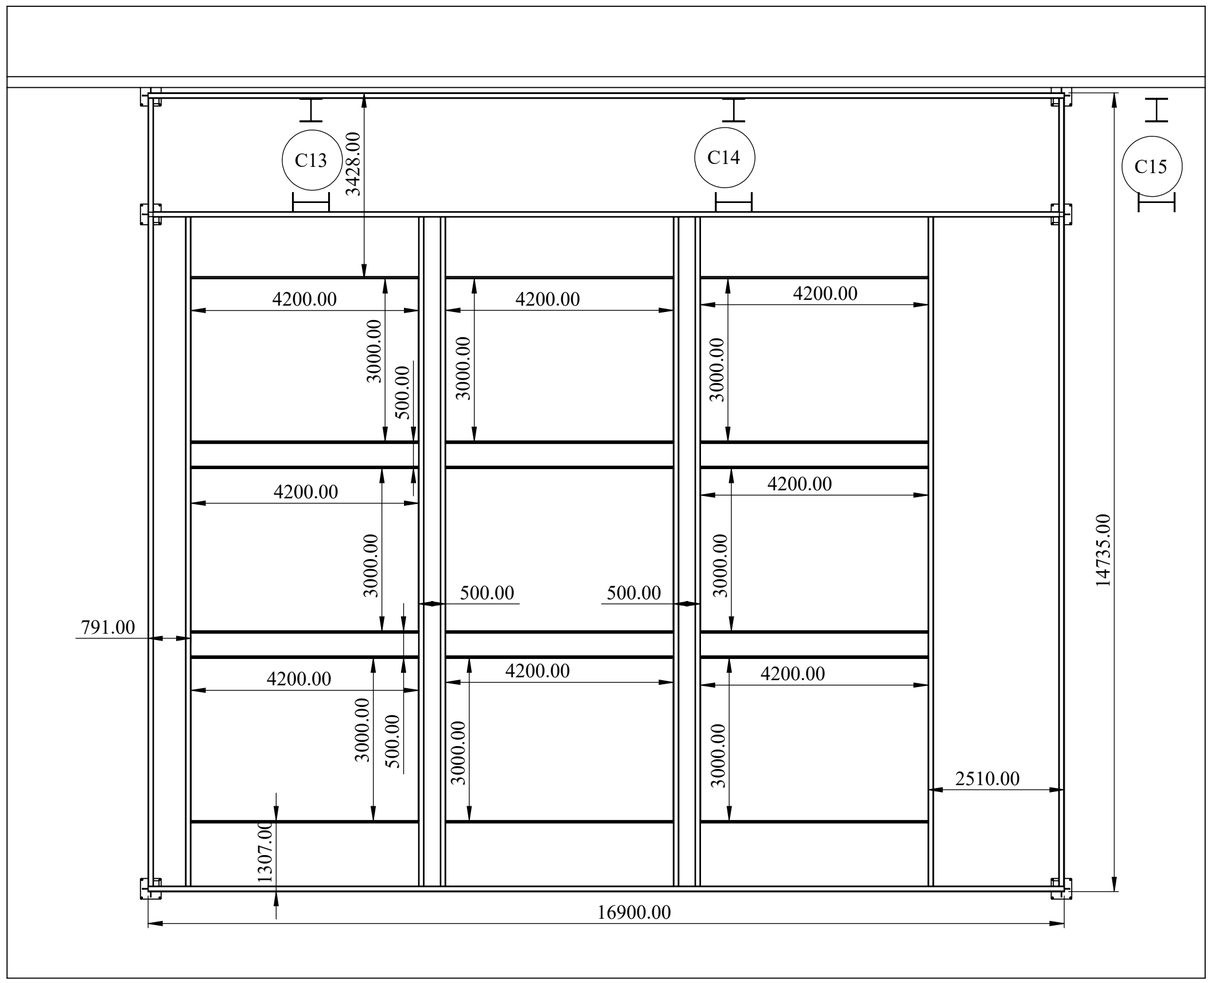

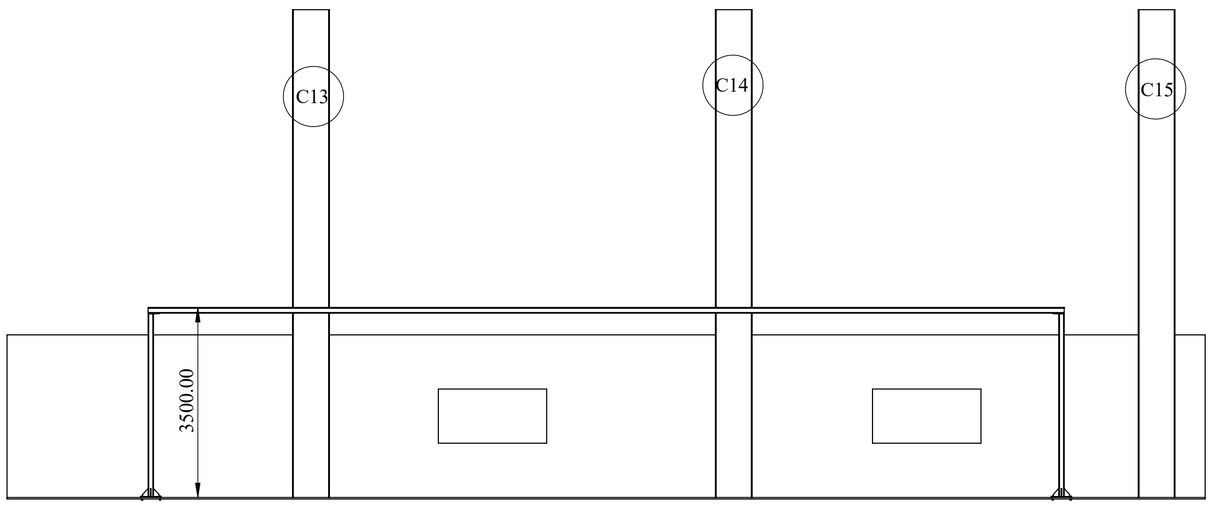
| REV DESCRIPTION | DATE | REV NO |
|---|---|---|
| | 17-06-2026 | REV 00 |
| 1. | | |

NOTE :

BASE STRUCTURE IN CLIENT SCOPE

SPECIAL INSTRUCTION'S :

This drawing & design is the property of NIHVA TECHONOLOGIES PVT. LTD. Not to be sold or copied to any other concern

TITLE - COLLAPSABLE CCA ROOF

DWG NO - NTPL-401-PM-04

NIHVA TECHNOLOGIES PVT.LTD.PUNE
Website - www.nihva.com

| | NAME | SIGNATURE | DATE |
|---|---|---|---|
| DRAWN | V.W. | | 17-06-2026 |
| CHK'D | S.P. | | 18-06-2026 |
| APPV'D | V.T. | | 18-06-2026 |

PRODUCT - RETRACTABLE ROOF

CLIENT NAME - NEOTRAFO SOLUTIONS

SITE LOCATION - HYDRABAD

MATRIAL -

QTY - 1

If any queries contact - info@nihva.com

ALL DIMENSION ARE IN mm

A2

PROJECTION METHOD:

SCALE :